

LỘC

Bản vẽ chi tiết bố cục từng vật trong nhà

Dự án game kinh dị 3D — môn Phát triển game nâng cao · căn nhà phố 8 × 25 m + tiệm tách riêng bên trái.

Toàn bộ số liệu đọc trực tiếp từ scene Assets/Scenes/LOC_NhaLoc.unity (bản dựng 30/09/2026 17:09, sau rà soát chạm mặt/chống lẩn).

Gồm 522 vật (đã tính cả biến thể Đêm 1/2/3), 14 cụm công tắc/ổ cắm, 29 nguồn sáng, 64 decal, hơn 874 khối kết cấu.

Mỗi vật có: mã, tên Việt + tên Unity, toạ độ tâm (X, Z), khung bao Rộng×Sâu×Cao, cao độ đáy → đỉnh (Y), hướng mặt trước.

Toạ độ dán thẳng được vào Unity: X = ngang (0 = mặt trong tường trái, đứng ngoài đường nhìn vào) · Z = chiều sâu (0 = mặt trong tường mặt tiền) · Y = cao độ (sàn tầng 1 = 0).

MỤC LỤC

Bìa & mục lục	1
Số chốt: cao độ, vỏ nhà, phòng, thang	2
Mặt bằng tổng thể (phố + sân + tiệm + nhà, tầng 1)	3
Mặt bằng tầng 1 — toàn bộ	4
Mặt bằng hầm	5
Mặt bằng tầng 2 — toàn bộ	6
Mặt bằng tầng 3 — toàn bộ	7
Sân trước — cổng, rạp tang, bàn phúng viếng (Đêm 1 / 2 / 3)	8
Tiệm vật liệu — khu bán hàng + kho	10
Phòng khách + bàn thờ vong	11
Sảnh sau + chân cầu thang + cửa hầm	13
Bếp + chỗ ăn	14
Giếng trời + khối sau (kho, WC, bể giặt)	16
Hầm	17
Phòng bố mẹ + WC khép kín + ban công	18
Sảnh, cầu thang, hành lang tầng 2	20
Góc làm việc (tầng 2)	21
Phòng Nhím	22
Phòng Khôi	23
Sân phơi + phòng thờ gia tiên (tầng 3)	24
Sảnh + góc kho mở (tầng 3)	26
Phụ lục A — công tắc & ổ cắm	27
Phụ lục B — nguồn sáng	28
Phụ lục C — decal bề mặt	29

CHÚ GIẢI

 Đồ đặt trên sàn	 Đồ đặt trên bàn / kệ / giường	 Treo tường / treo trần
 Điện - đèn - quạt	 Cửa, cổng, cửa sổ, rèm	 Kết cấu phụ / cố định
 Tường (cắt ở 1,5 m)	 Bậu / tường thấp	 Kính
 Công tắc / ổ cắm (CT..)	 Nguồn sáng (L..)	 ▲ mặt trước của vật
 Đ1: chỉ có ở Đêm 1	 Đ2: chỉ có ở Đêm 2	 Đ3: chỉ có ở Đêm 3

Các số này là số thật trong scene — đối chiếu được với LocHouseBuilder.cs

Cao độ (Y, mét)

Sàn hầm	−2,30 · trần hầm 2,10 (mặt dưới sàn T1 ở −0,20)
Sân trước / hiên	−0,15 (một bậc 0,15 lên sàn tiệm & nhà)
Sàn tầng 1	±0,00 · trần 3,20 · sàn dày 0,20
Sàn tầng 2	+3,40 · trần 3,00
Sàn tầng 3	+6,60 · trần 3,00
Mặt mái	+9,80 (giếng trời 1,90 × ... trên ô thang, lợp tấm nhựa)
Tấm mắt người chơi	1,65 m (cao 1,65 m)

Vỏ nhà

Bể ngang thông thủy nhà	7,60 m (X 0 → 7,60); tường bao 0,20 hai bên
Chiều sâu nhà (khối xây)	Z −0,20 → 24,80 (≈ 25 m); khối sau kết thúc ở Z 24,60
Sân trước	X −0,20 → 7,80 · Z −5,40 → −0,20; cổng sắt ở Z −5,25; cao độ −0,15
Tiệm (tách riêng, bên trái)	X −4,40 → −0,20 · Z −5,40 → 7,00; vách kho ở Z 1,80–1,90; mái tôn +3,60
Tường ngăn trong	0,10 m (T2 và T3); tường bao T1 0,20
Cửa sắt xếp mặt tiền tiệm	lỗ 3,60 × 2,40 (X −4,10 → −0,50)

Phòng theo từng tầng (khoảng Z, theo LocHouseBuilder.cs)

Tầng 1 — Phòng khách	Z 0 → 7,40 · 7,60 × 7,40
Tầng 1 — Sânh sau + chân thang	Z 7,50 → 10,90 · thang chữ U sát tường trái (X 0 → 1,90)
Tầng 1 — Bếp + ăn	Z 11,00 → 16,40 · 7,60 × 5,40
Tầng 1 — Giếng trời	Z 16,50 → 19,10 · lộ trời, sàn −0,05
Tầng 1 — Khối sau	Z 19,20 → 24,60 · kho (X 0 → 3,60), WC (X 4,70 → 7,60 · Z 19,20 → 21,80), bể giặt (Z 21,90 → 24,60)
Tầng 2 — Ban công	Z −1,20 → −0,20 (nhô 1,0 m), lan can 1,0–1,1 m
Tầng 2 — Phòng bố mẹ	Z 0 → 5,40 · 7,60 × 5,40 · WC khép kín góc phải (X 5,80 → 7,60 · Z 3,60 → 5,40)
Tầng 2 — Hành lang + thang	X 1,90 → 3,10 hành lang; thang X 0 → 1,90; Z 5,50 → 16,40
Tầng 2 — Góc làm việc	X 3,20 → 7,60 · Z 5,50 → 8,40 (ô mở không cánh Z 6,00 → 7,20)
Tầng 2 — Phòng Nhím	X 3,20 → 7,60 · Z 8,50 → 12,40 · 4,40 × 3,90 · cửa Z 8,95 → 9,85
Tầng 2 — Phòng Khôi	X 3,20 → 7,60 · Z 12,50 → 16,40 · 4,40 × 3,90 · cửa Z 13,40 → 14,20
Tầng 3 — Sân phơi	Z 0 → 3,00 · 7,60 × 3,00 (cửa ra sân phơi Z 3,00)
Tầng 3 — Phòng thờ	Z 3,10 → 6,40 · 7,60 × 3,30
Tầng 3 — Sânh + góc kho mở	Z 6,50 → 10,80 (ô thang X 1,90 → 7,60; góc kho không cửa)



Cầu thang (bậc lấy thẳng từ scene)

Thang chính T1 → T2	vế 1: X 1,00 → 1,90 từ Z 7,60, 10 bậc cao 0,17 · chiều nghỉ +1,70 (Z 9,85 → 10,85) · vế 2: X 0 → 0,90 đi ra Z 9,85
Thang chính T2 → T3	vế 1 từ Z 7,60, 9 bậc cao 0,178 · chiều nghỉ +1,60 so với sàn T2 · vế 2 đi ra Z 9,60
Bậc thang	mặt bậc sâu 0,25 · rộng vế 0,90 · bậc granito
Thang hầm	dưới vế 2 của thang chính; dốc hơn thang chính (0,19 × 0,24) — cố ý, xem kịch bản


Bảng số vật theo phòng

ST — Sân trước + cổng + rạp tang	79 vật	TB — Tiệm — khu bán hàng	16 vật
TK — Tiệm — kho	16 vật	PK — Phòng khách + bàn thờ vong	68 vật
SS — Sânh sau + chân thang + cửa hầm	27 vật	BA — Bếp + chỗ ăn	56 vật
GT — Giếng trời	5 vật	KS — Khối sau: kho, WC, bể giặt	25 vật
H — Hầm	8 vật	BM — Phòng bố mẹ + WC + ban công	70 vật
S2 — Sânh, thang, hành lang tầng 2	32 vật	LV — Góc làm việc	9 vật
NH — Phòng Nhím	22 vật	KH — Phòng Khôi	25 vật
SP — Sân phơi	16 vật	PT — Phòng thờ gia tiên	41 vật
GK — Sânh + góc kho mở	7 vật		



Mặt bằng tầng 1 kèm khu phố xung quanh · chỉ vẽ kết cấu, đường, nhà hàng xóm và khung chiếm chỗ của vật trong nhà

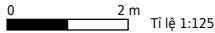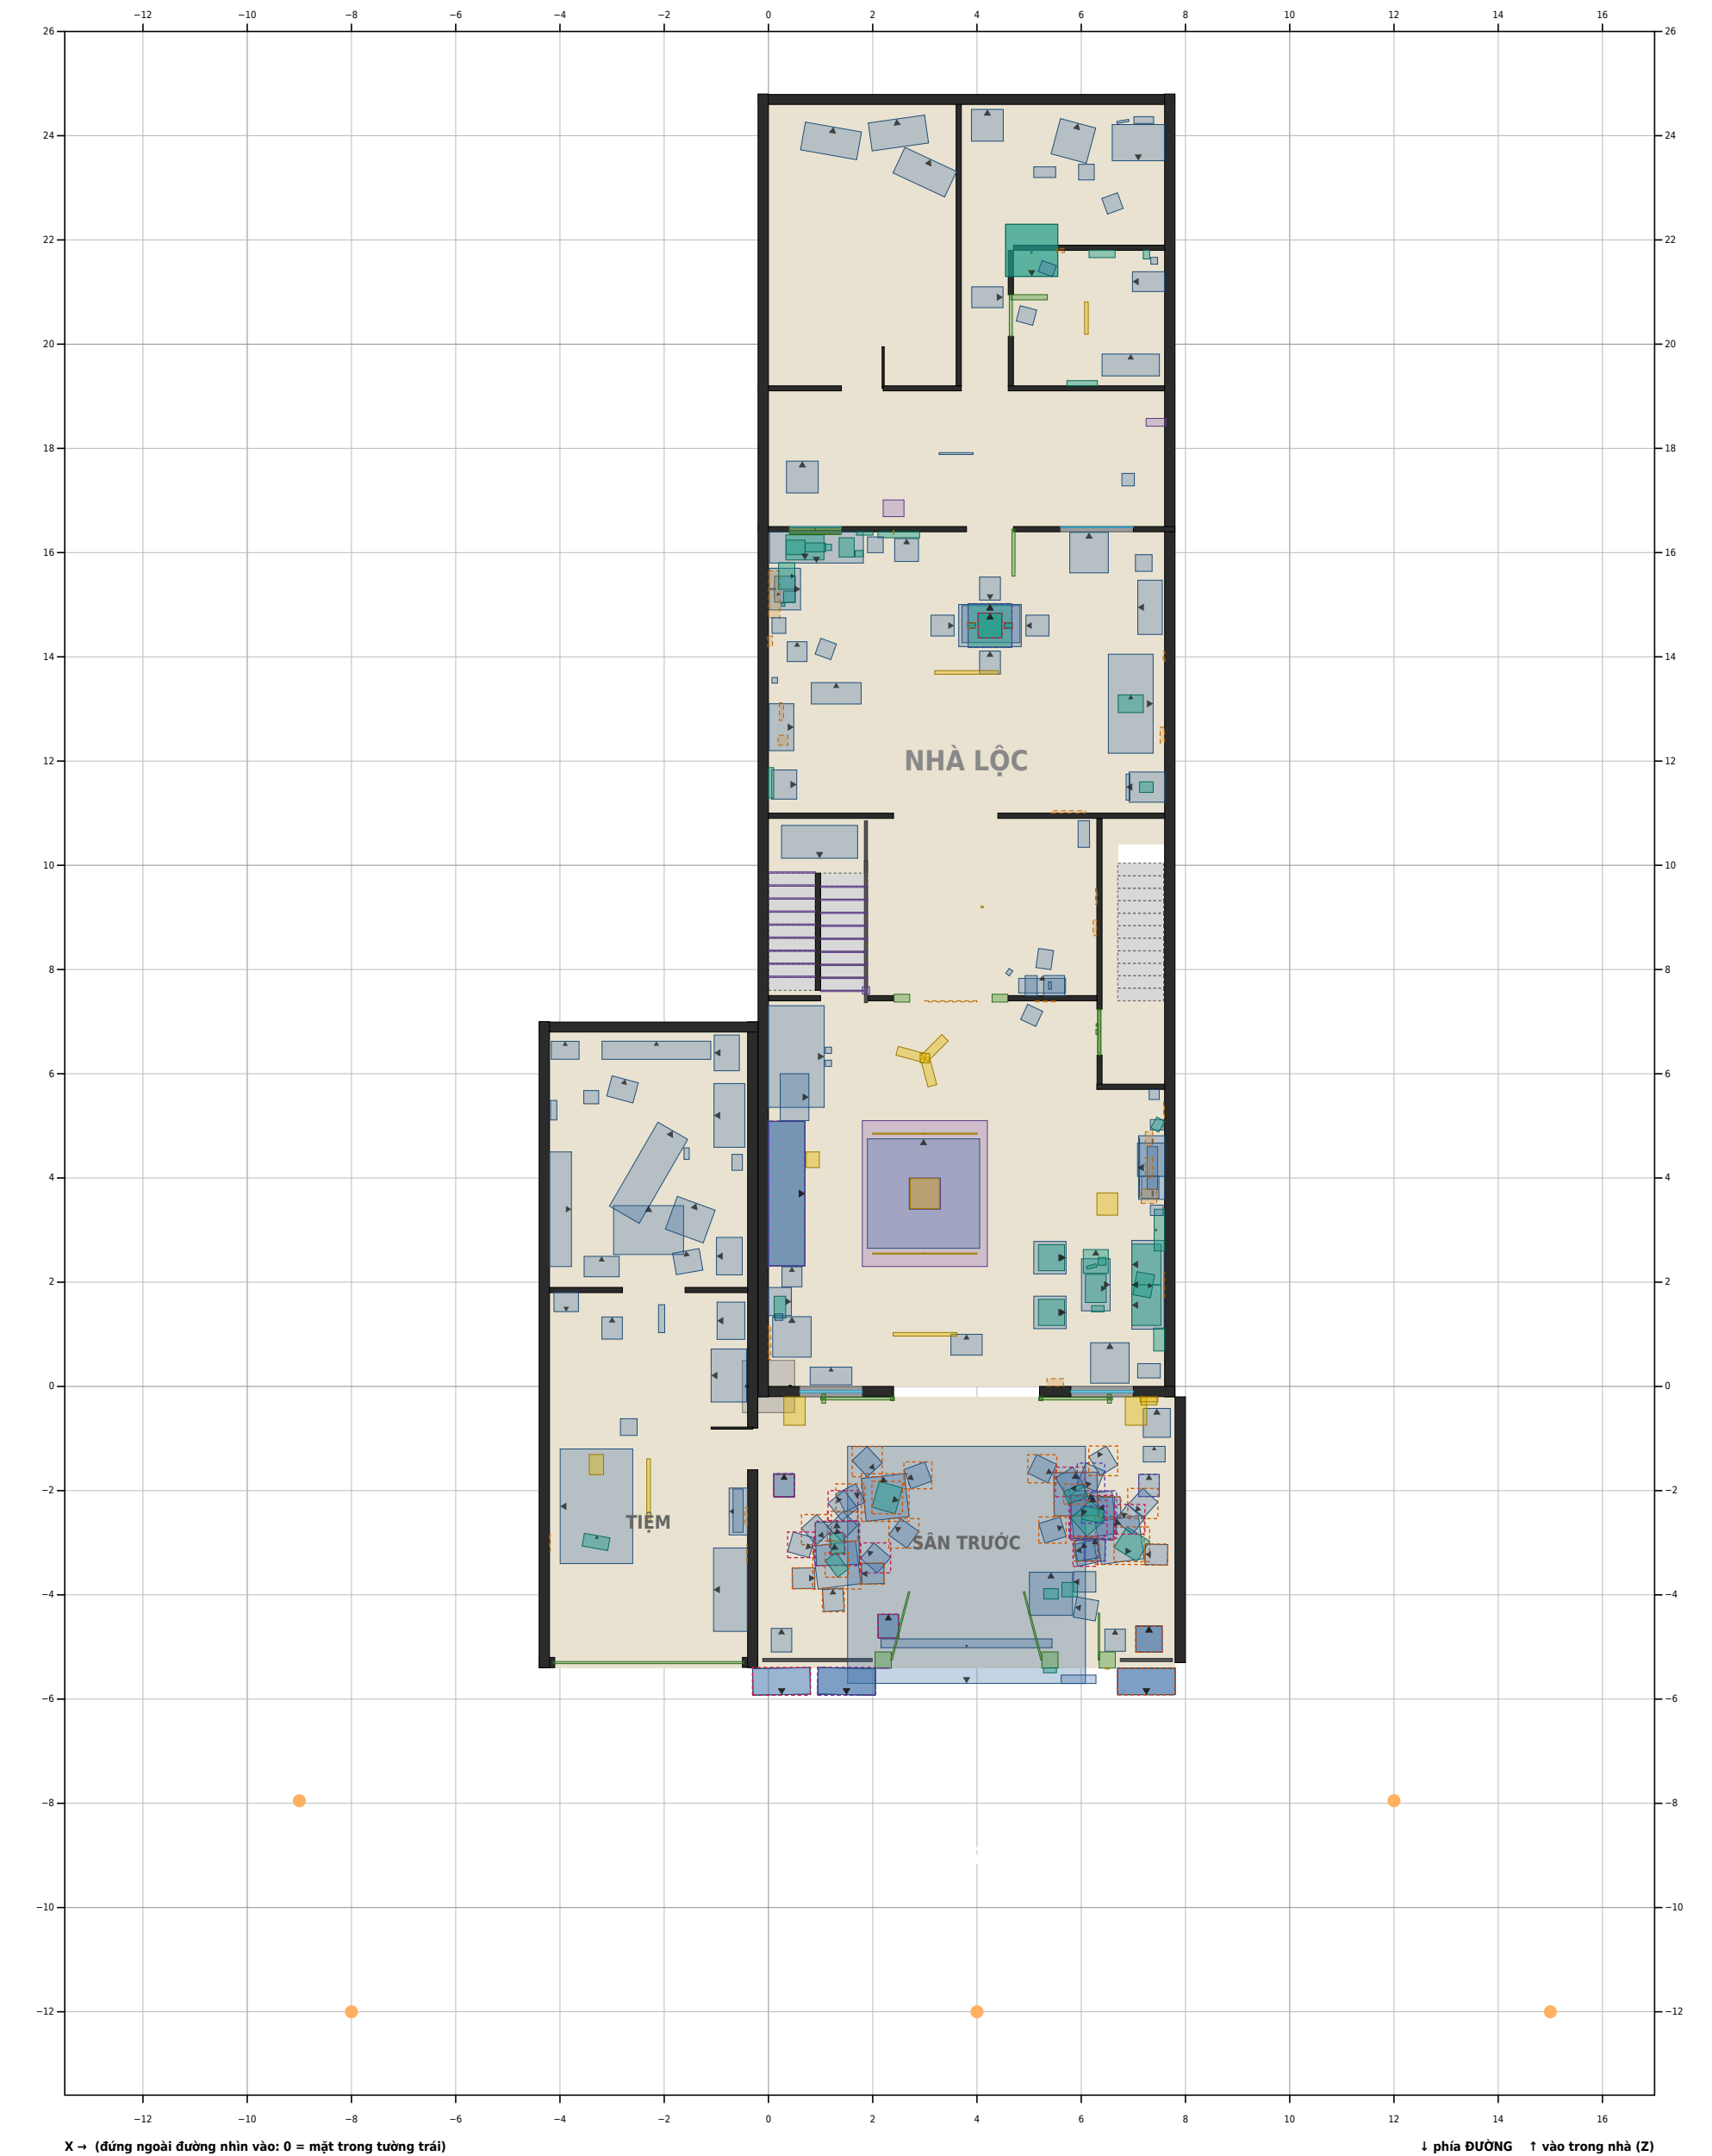

Tầng 1 (±0,00) · mỗi vật vẽ bằng khung bao thật; nhãn = mã vật (tra bảng ở các trang phòng) — chỉ gắn nhãn cho vật ≥ 0,25 m²

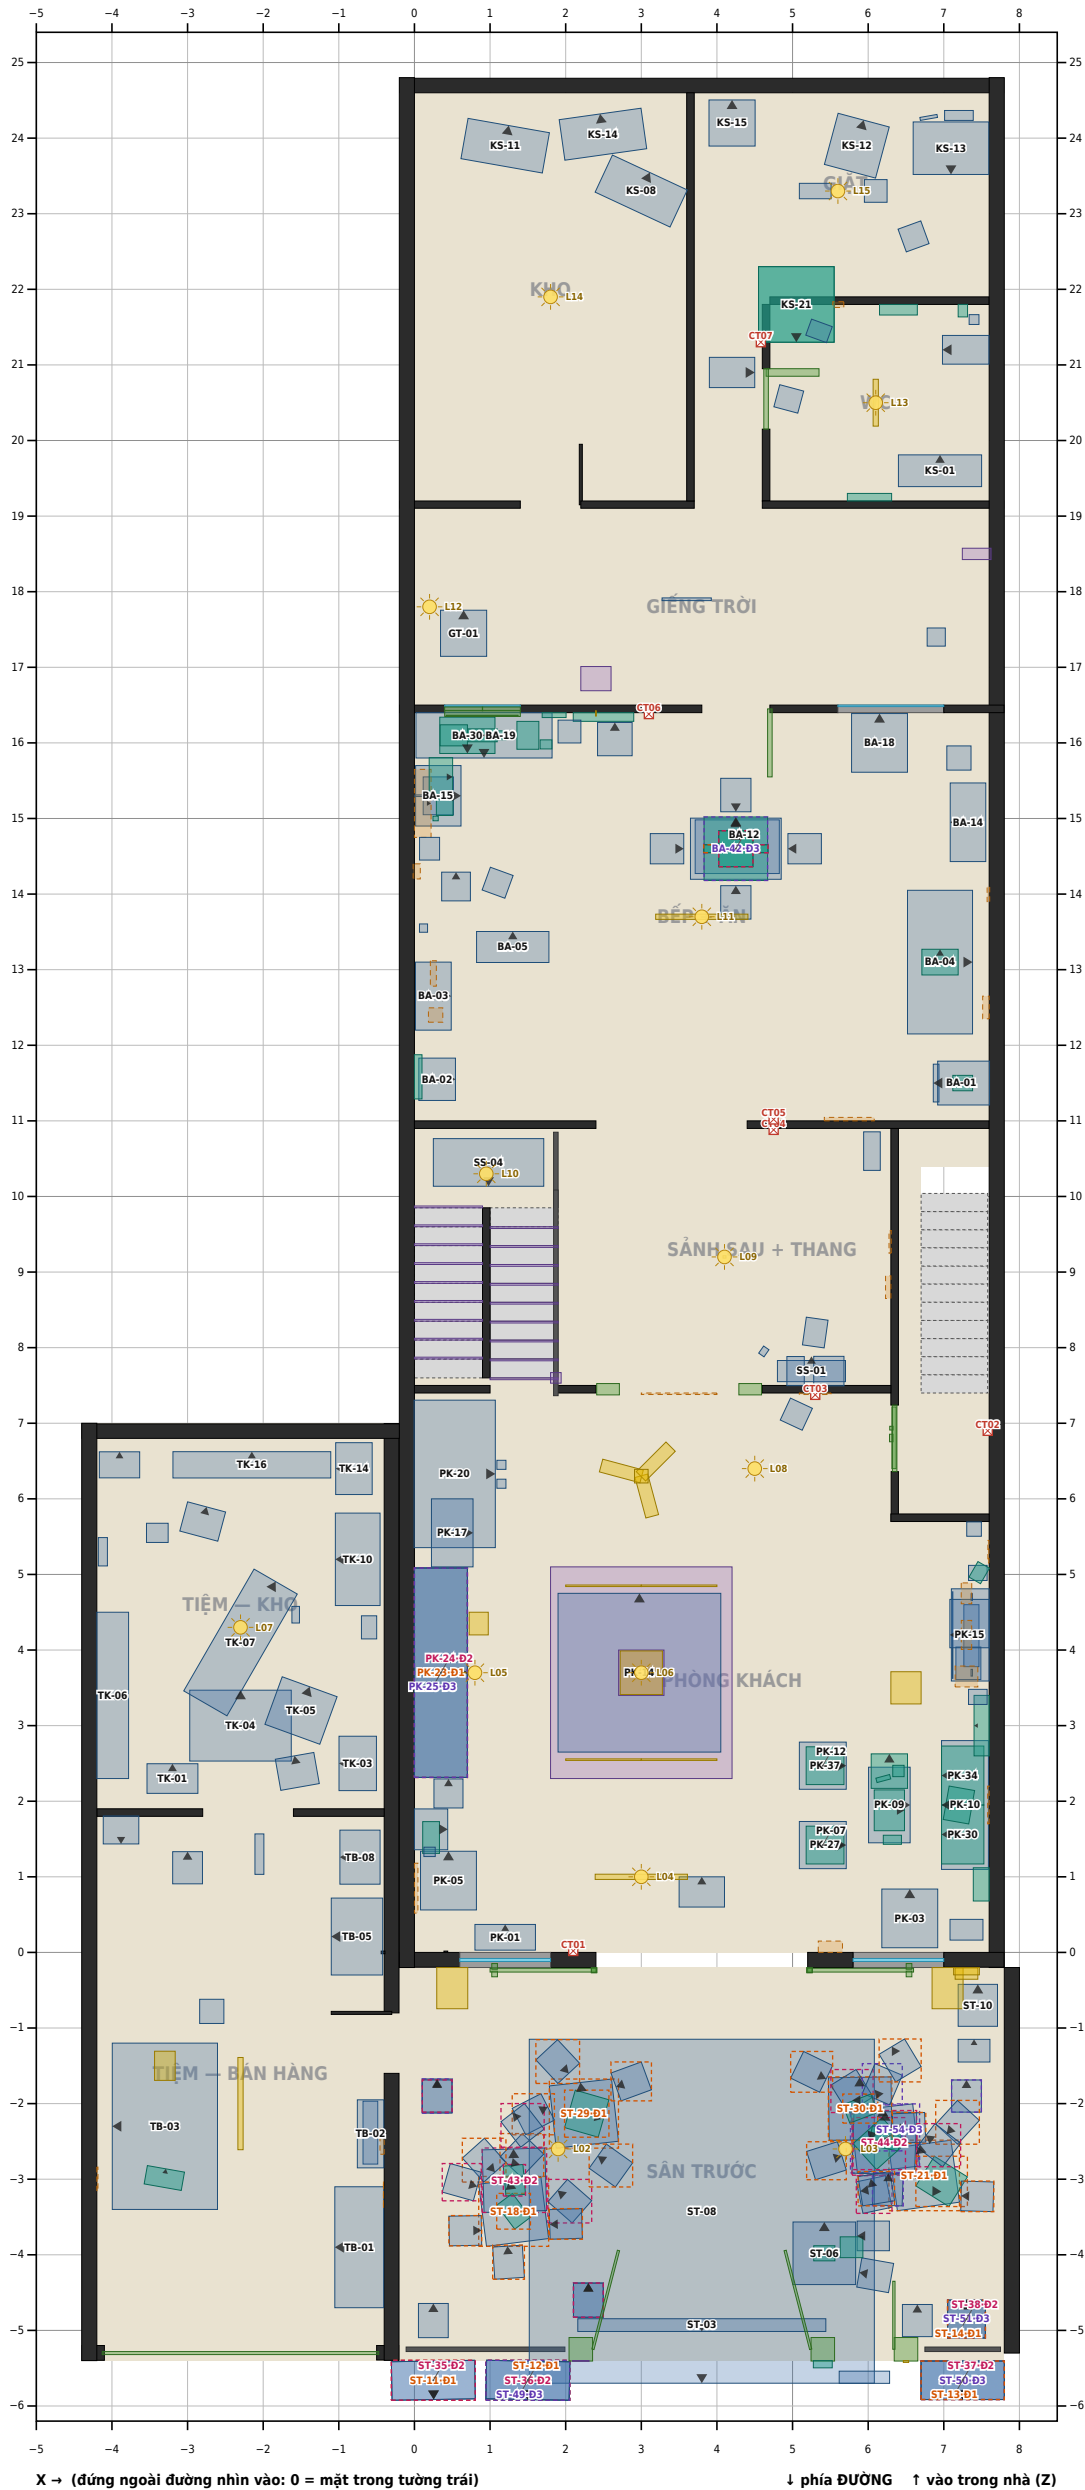


Hầm (-2,30) · mỗi vật vẽ bằng khung bao thật; nhãn = mã vật (tra bảng ở các trang phòng) — chỉ gắn nhãn cho vật $\geq 0,25 \text{ m}^2$

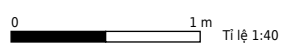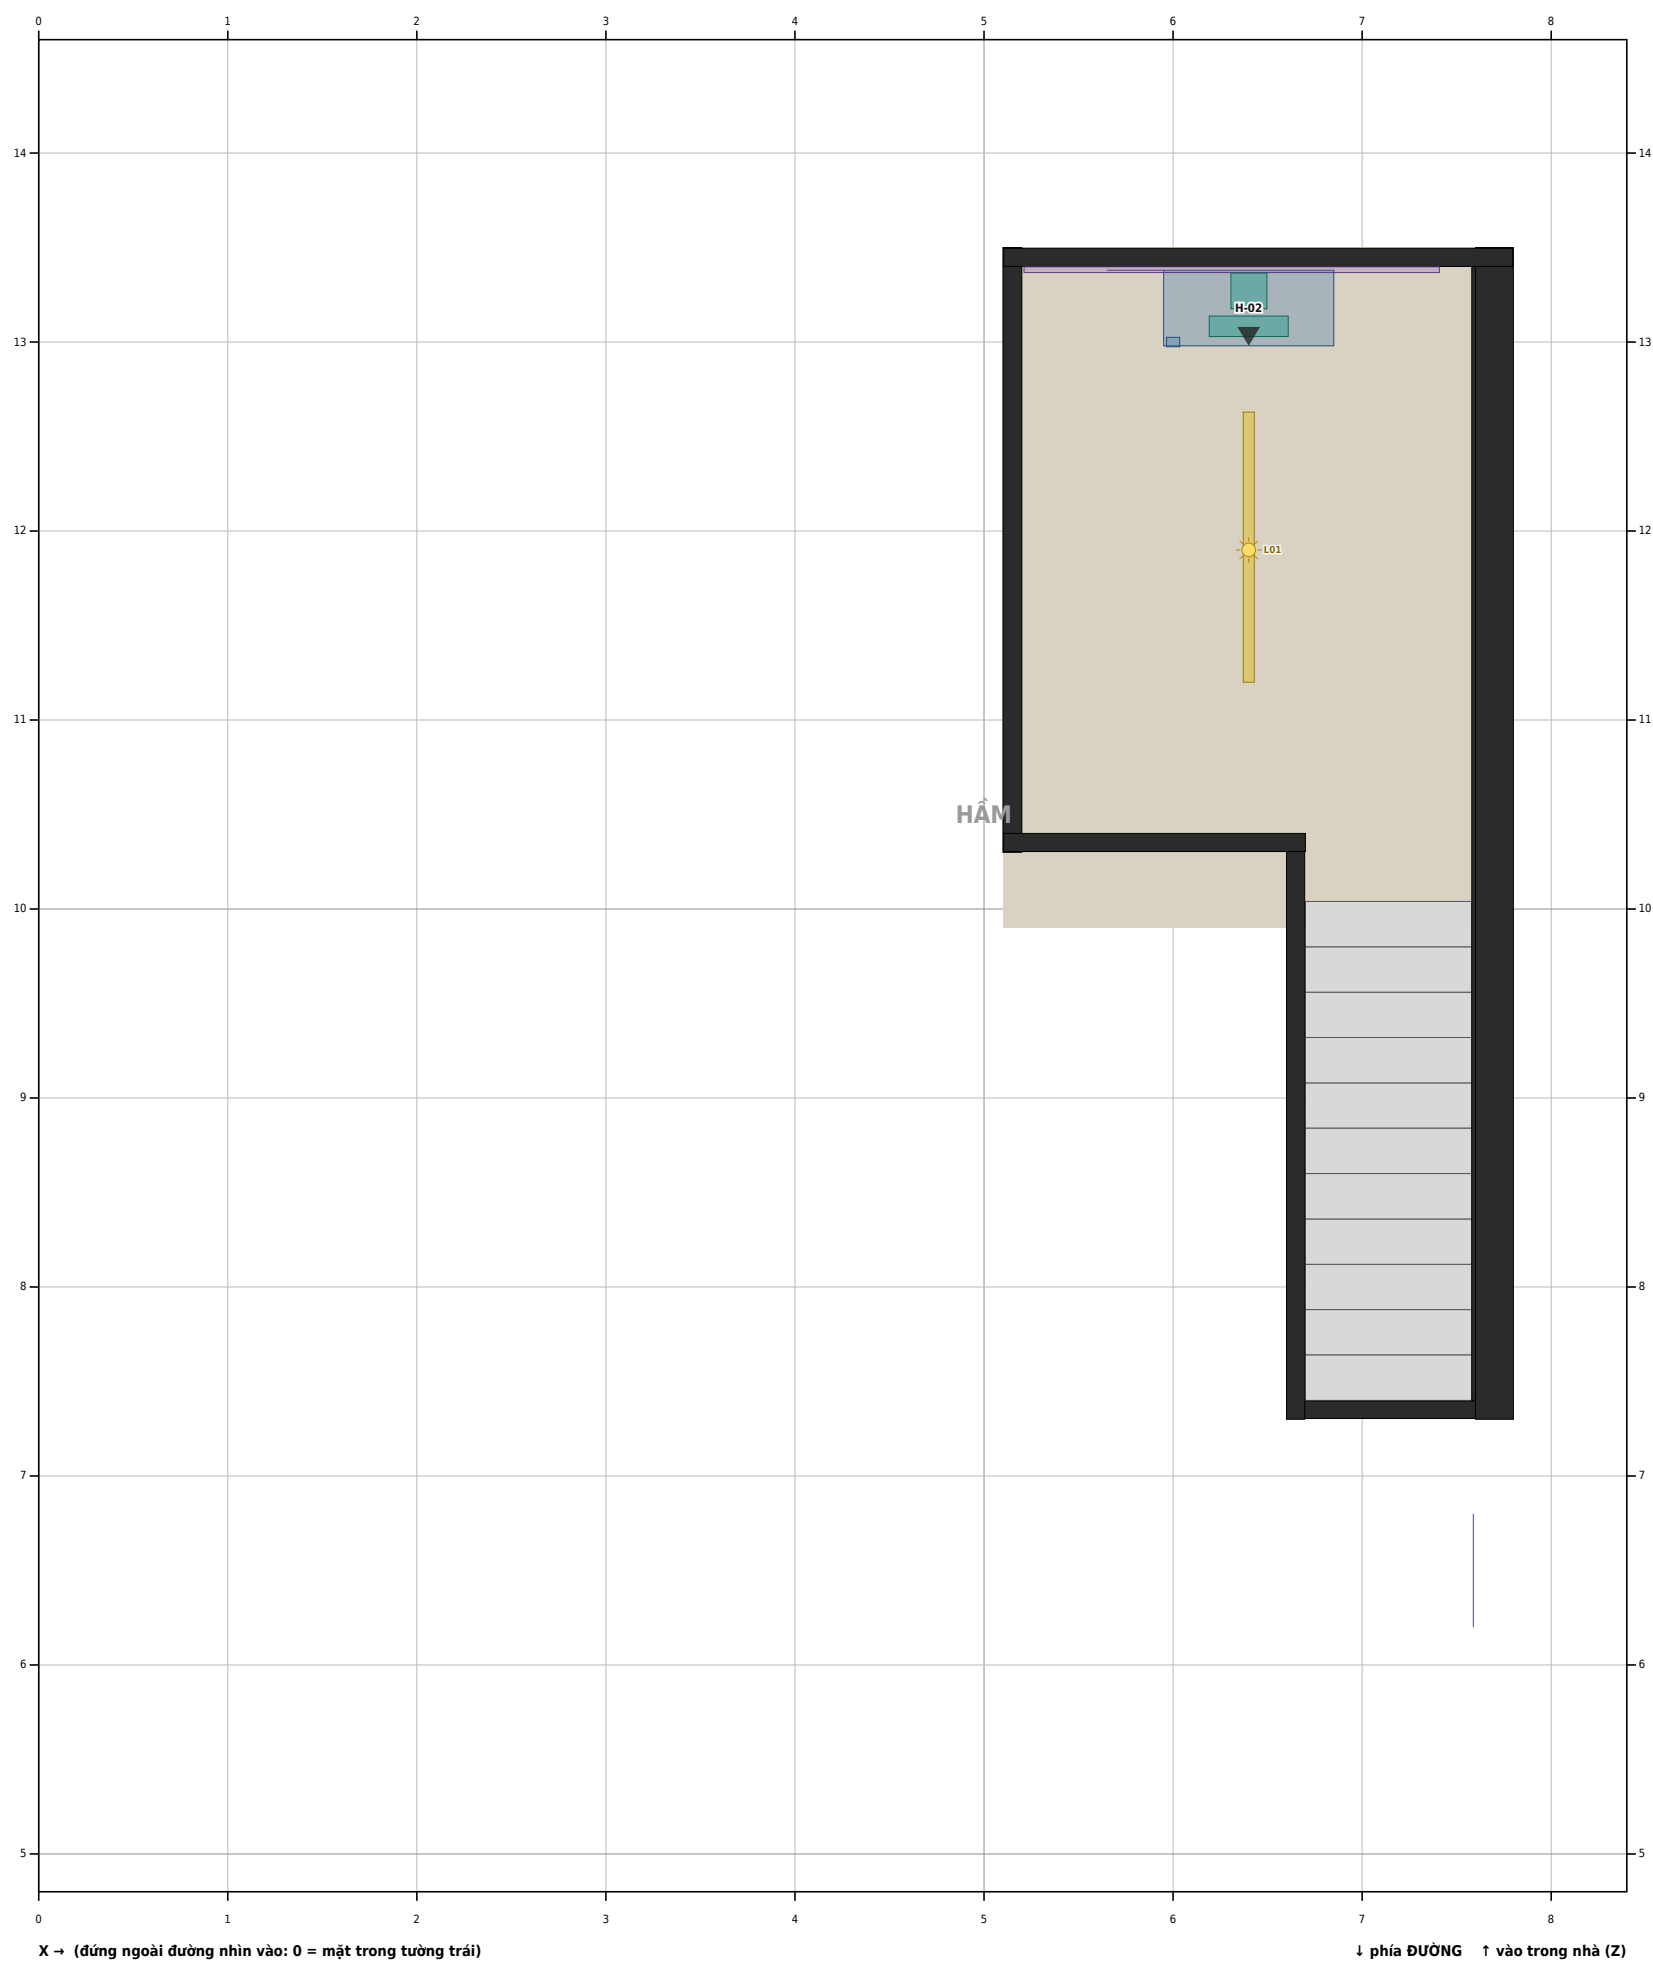


CHÚ GIẢI

- | | | |
|---|---|--|
|  Đò đặt trên sàn |  Đò đặt trên bàn / kệ / giường |  Treo tường / treo trần |
|  Điện - đèn - quạt |  Cửa, cổng, cửa sổ, rèm |  Kết cấu phụ / cố định |
|  Tường (cắt ở 1,5 m) |  Bậu / tường thấp |  Kính |
|  Công tác / ổ cắm (CT..) |  Nguồn sáng (L..) |  Mặt trước của vật |
|  D1: chỉ có ổ Điện 1 |  D2: chỉ có ổ Điện 2 |  D3: chỉ có ổ Điện 3 |

Tầng 2 (+3,40) · mỗi vật vẽ bằng khung bao thật; nhãn = mã vật (tra bảng ở các trang phòng) — chỉ gắn nhãn cho vật ≥ 0,25 m²

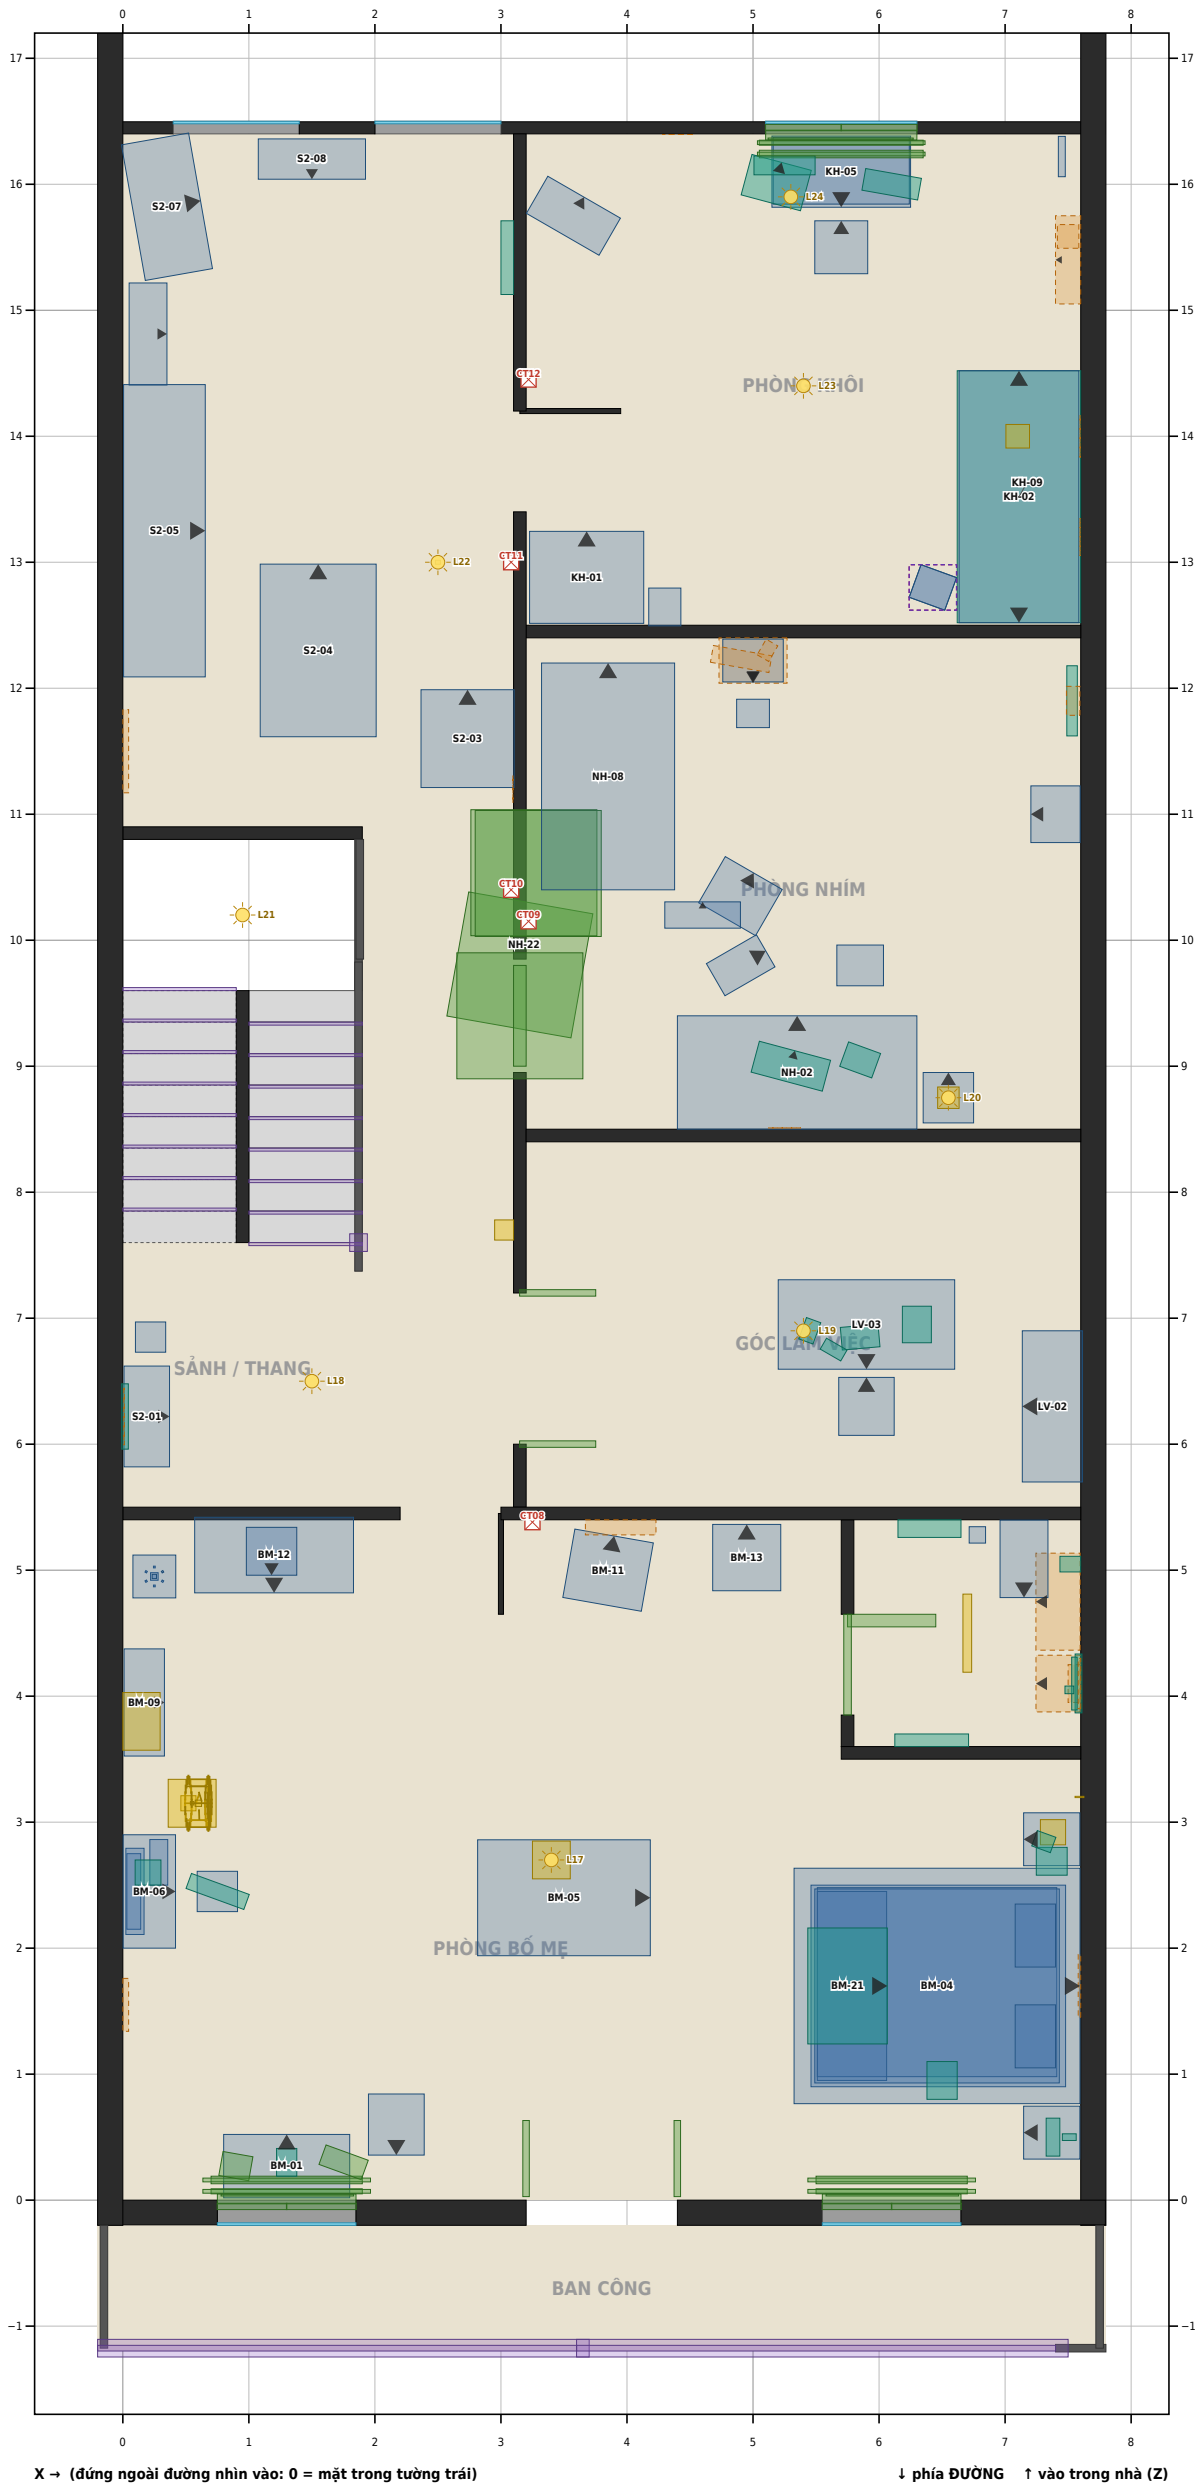

Tầng 3 (+6,60) · mỗi vật vẽ bằng khung bao thật; nhãn = mã vật (tra bảng ở các trang phòng) — chỉ gắn nhãn cho vật ≥ 0,25 m²

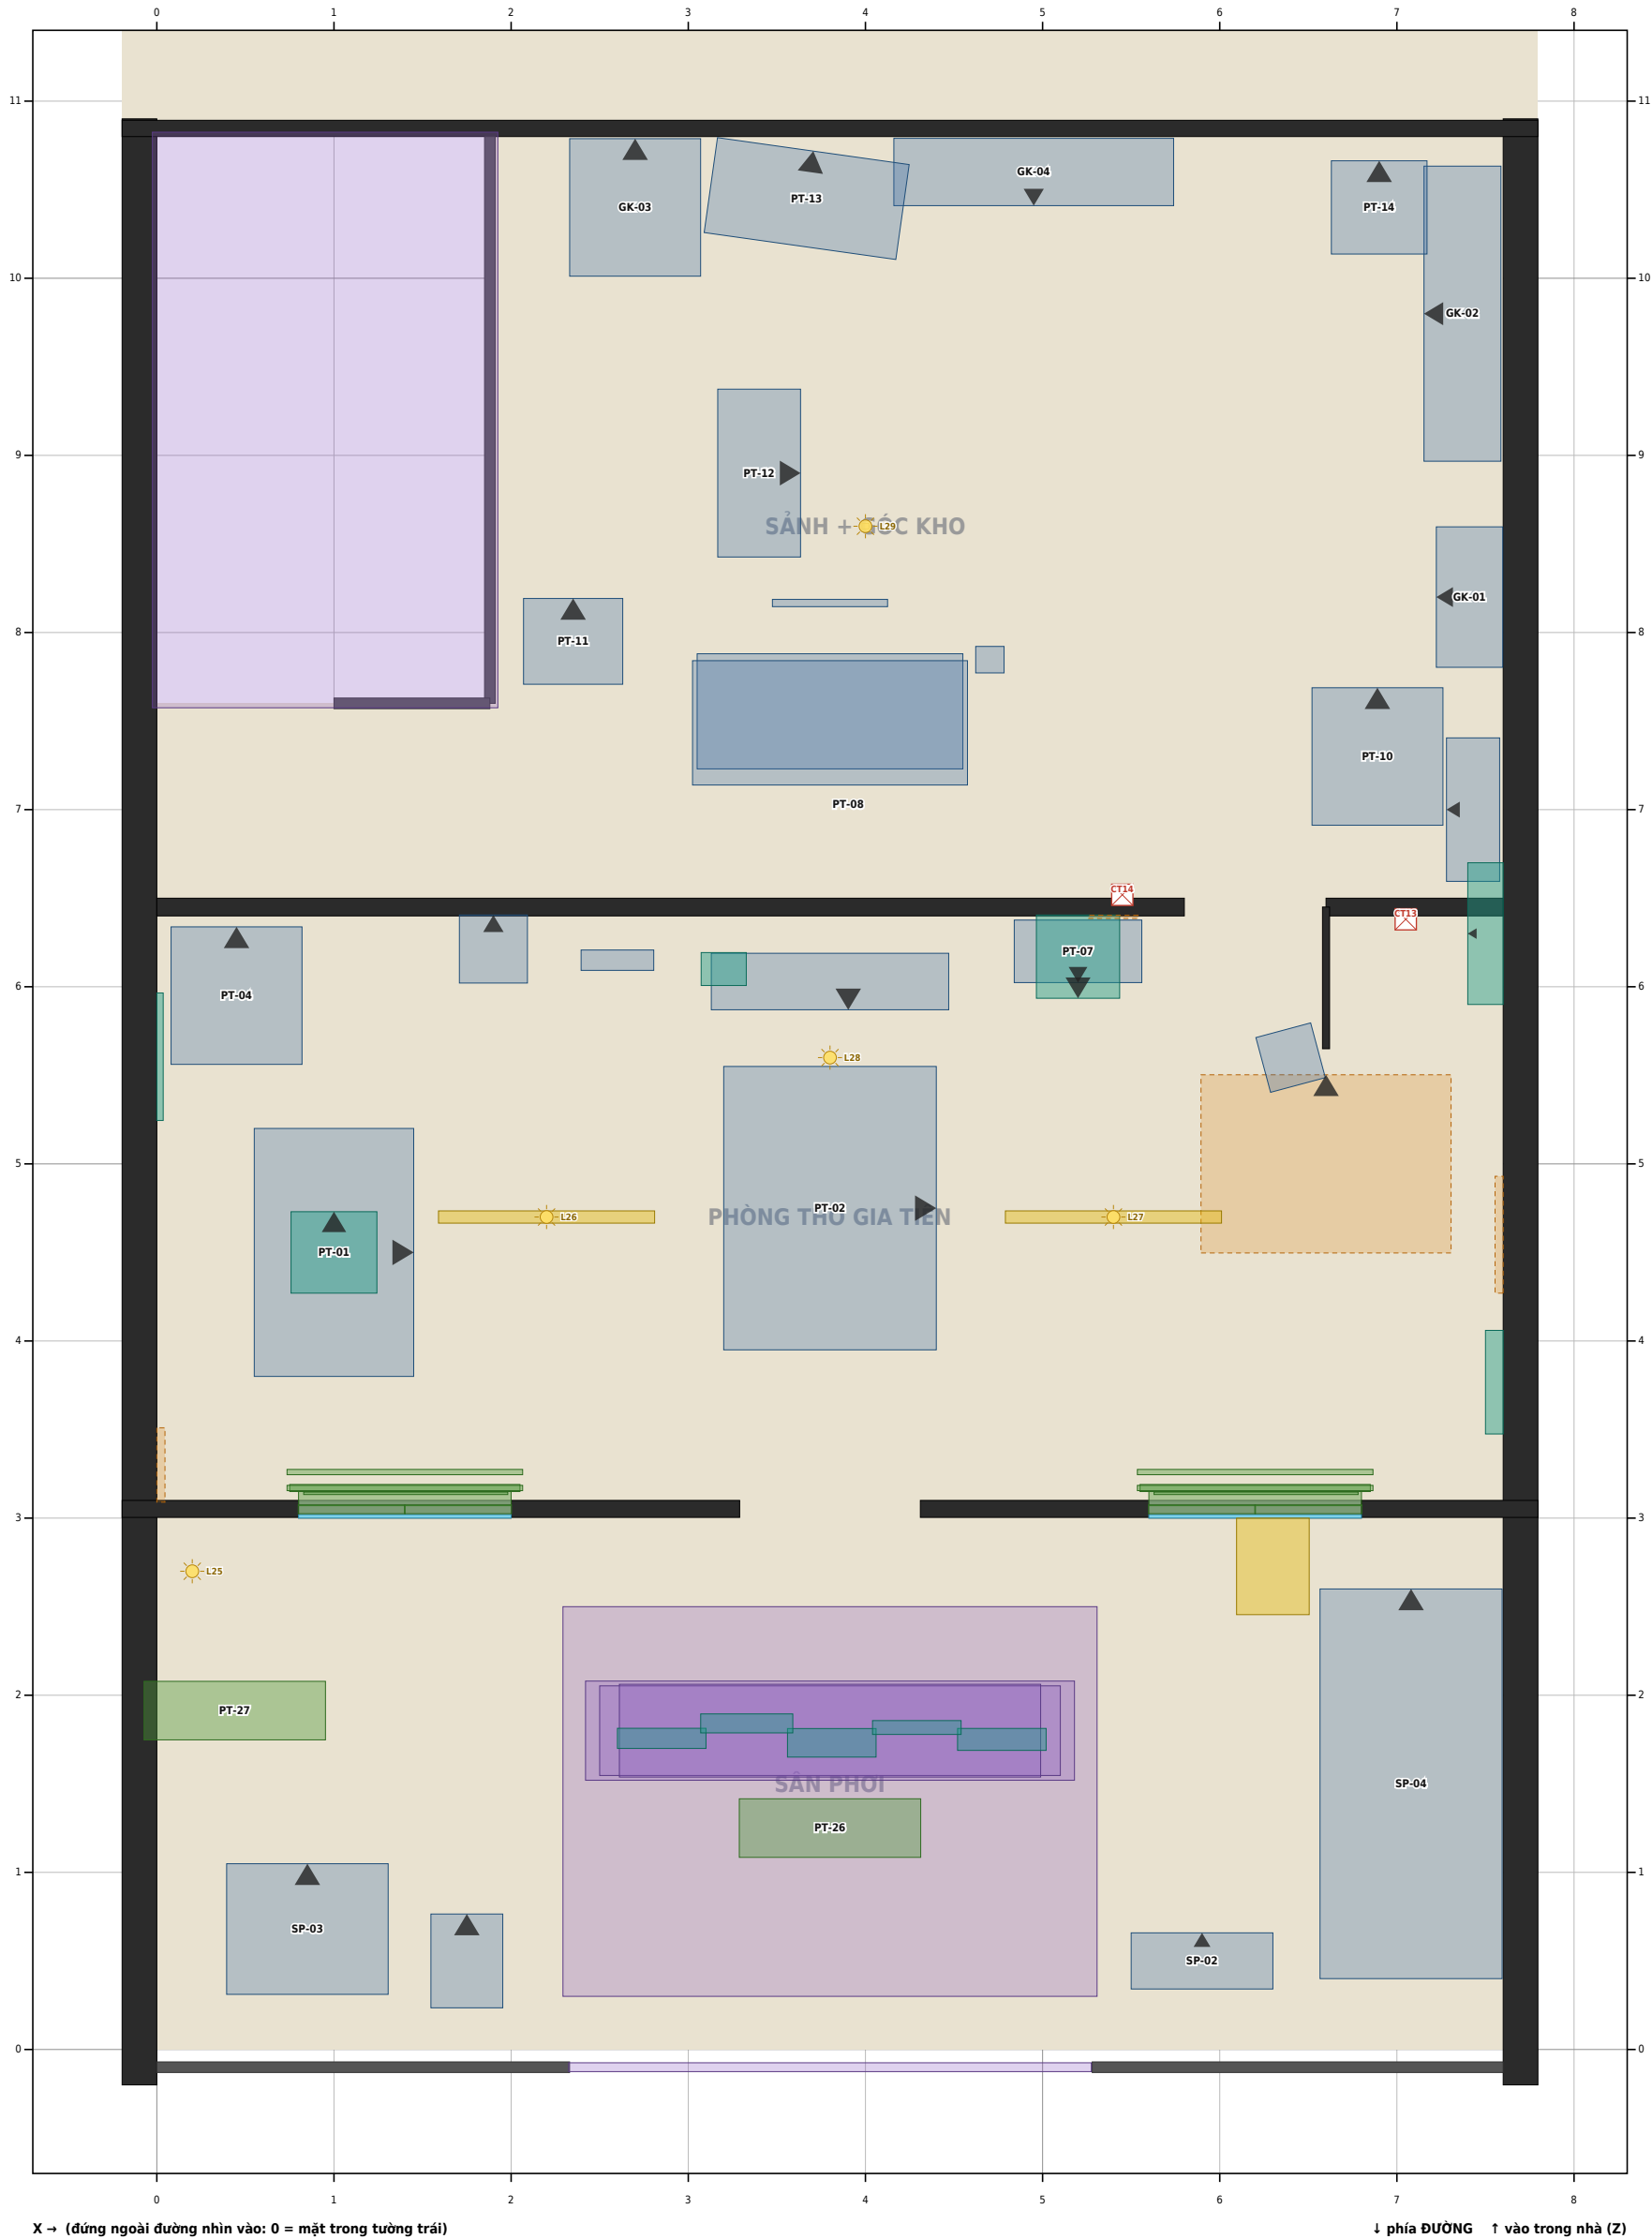

01 m

Tỉ lệ 1:40

CHÚ GIẢI

Đồ đặt trên sàn

Điện - đèn - quạt

Tường (cắt ở 1,5 m)

Công tắc / ổ cắm (CT..)

Đ1: chỉ có ở Đêm 1

Đồ đặt trên bàn / kệ / giường

Cửa, cổng, cửa sổ, rèm

Bậu / tường thấp

Nguồn sáng (L..)

Đ2: chỉ có ở Đêm 2

Treo tường / treo trần

Kết cấu phụ / cố định

Kính

▲ mặt trước của vật

Đ3: chỉ có ở Đêm 3

Nguồn: scene Assets/Scenes/LOC_NhaLoc.unity (dựng 30/09/2026 17:09) — toạ độ Unity thế giới, đơn vị mét. X: ngang - Z: chiều sâu - Y: cao độ (sàn T1 = 0). Mã vật = mã phòng + số thứ tự (PK-07...). Đ1/Đ2/Đ3 = vật chỉ có ở Đêm 1/2/3. Kích thước = khung bao của mesh thật (.glb).

Tầng 1 (±0,00) · 79 vật trong ST



Mã	Tên (tên trong Unity)	Đêm	Tâm X	Tâm Z	Rộng×Sâu×Cao (m)	Y đáy → đỉnh	Hướng
ĐỒ ĐẶT TRÊN SÀN							
ST-01	Bảng cáo phó SM_ObituaryBoard		5,95	-5,62	0,67×0,16×0,83	-0,15 → 0,68	ra đường
ST-02	Chống 8 ghế nhựa SM_PlasticChairStack_8		0,25	-4,87	0,39×0,45×1,24	-0,15 → 1,09	trong
ST-03	Cổng rạp tang SM_FuneralGate		3,80	-4,93	3,28×0,17×2,42	-0,15 → 2,27	ra đường
ST-04	Chống 4 ghế nhựa SM_PlasticChairStack_4		6,65	-4,87	0,39×0,43×0,99	-0,15 → 0,84	trong
ST-05	Ghế nhựa xanh SM_PlasticChair_Green		6,09	-4,27	0,39×0,43×0,81	-0,15 → 0,66	-80°
ST-06	Bàn nhựa trải khăn (nhận phúng vi...		5,42	-3,98	0,83×0,83×0,72	-0,15 → 0,57	trong
ST-07	Ghế nhựa đỏ SM_PlasticChair_Red		6,07	-3,75	0,39×0,43×0,81	-0,15 → 0,66	← trái
ST-08	Rạp tang (khung bạt) SM_FuneralTent_300		3,80	-3,42	4,56×4,55×2,93	-0,16 → 2,77	ra đường
ST-09	Thùng nước ngọt phục vụ khách ThungNuocNgot_Khach		7,40	-1,30	0,42×0,30×0,34	-0,15 → 0,19	trong
ST-10	Thùng rác nhựa + bao đen ThungRacNhua		7,45	-0,70	0,52×0,56×0,94	-0,15 → 0,79	trong
ST-11	Vòng hoa (tươi) VongHoa_Tuoi	Đ1	0,25	-5,66	1,10×0,51×1,35	-0,15 → 1,20	179°
ST-12	Vòng hoa (tươi) VongHoa_Tuoi	Đ1	1,50	-5,66	1,10×0,51×1,35	-0,15 → 1,20	-179°
ST-13	Vòng hoa (tươi) VongHoa_Tuoi	Đ1	7,25	-5,66	1,10×0,51×1,35	-0,15 → 1,20	ra đường
ST-14	Chậu đốt vàng mã (đang cháy) SM_BurnBasin_Burning	Đ1	7,30	-4,85	0,50×0,50×0,39	0,18 → 0,57	trong
ST-15	Ghế nhựa đỏ SM_PlasticChair_Red	Đ1	1,25	-4,10	0,39×0,43×0,81	-0,15 → 0,66	-4°
ST-16	Ghế nhựa xanh SM_PlasticChair_Green	Đ1	0,67	-3,68	0,39×0,43×0,81	-0,15 → 0,66	89°
ST-17	Ghế nhựa xanh SM_PlasticChair_Green	Đ1	2,00	-3,59	0,39×0,43×0,81	-0,15 → 0,66	-92°
ST-18	Bàn nhựa trải khăn (nhận phúng vi...	Đ1	1,31	-3,43	0,83×0,83×0,72	-0,15 → 0,57	-7°
ST-19	Ghế nhựa xanh SM_PlasticChair_Green	Đ1	7,44	-3,23	0,39×0,43×0,81	-0,15 → 0,66	-88°
ST-20	Ghế nhựa đỏ SM_PlasticChair_Red	Đ1	6,11	-3,13	0,39×0,43×0,81	-0,15 → 0,66	-99°
ST-21	Bàn nhựa trải khăn (nhận phúng vi...	Đ1	6,74	-2,95	0,83×0,83×0,72	-0,15 → 0,57	-8°
ST-22	Ghế nhựa đỏ SM_PlasticChair_Red	Đ1	2,60	-2,82	0,39×0,43×0,81	-0,15 → 0,66	-54°
ST-23	Ghế nhựa đỏ SM_PlasticChair_Red	Đ1	5,45	-2,76	0,39×0,43×0,81	-0,15 → 0,66	72°
ST-24	Ghế nhựa đỏ SM_PlasticChair_Red	Đ1	0,92	-2,75	0,39×0,43×0,81	-0,15 → 0,66	138°
ST-25	Ghế nhựa đỏ SM_PlasticChair_Red	Đ1	1,42	-2,69	0,39×0,43×0,81	-0,15 → 0,66	-136°
ST-26	Ghế nhựa xanh SM_PlasticChair_Green	Đ1	6,54	-2,32	0,39×0,43×0,81	-0,15 → 0,66	-92°
ST-27	Ghế nhựa đỏ SM_PlasticChair_Red	Đ1	7,18	-2,25	0,39×0,43×0,81	-0,15 → 0,66	-138°
ST-28	Ghế nhựa xanh SM_PlasticChair_Green	Đ1	1,57	-2,14	0,39×0,43×0,81	-0,15 → 0,66	63°
ST-29	Bàn nhựa trải khăn (nhận phúng vi...	Đ1	2,24	-2,13	0,83×0,83×0,72	-0,15 → 0,57	-6°
ST-30	Bàn nhựa trải khăn (nhận phúng vi...	Đ1	5,89	-2,07	0,83×0,83×0,72	-0,15 → 0,57	-1°
ST-31	Ghế nhựa xanh SM_PlasticChair_Green	Đ1	2,87	-1,71	0,39×0,43×0,81	-0,15 → 0,66	-110°
ST-32	Ghế nhựa xanh SM_PlasticChair_Green	Đ1	5,25	-1,58	0,39×0,43×0,81	-0,15 → 0,66	116°
ST-33	Ghế nhựa đỏ SM_PlasticChair_Red	Đ1	1,90	-1,44	0,39×0,43×0,81	-0,15 → 0,66	137°
ST-34	Ghế nhựa đỏ SM_PlasticChair_Red	Đ1	6,42	-1,43	0,39×0,43×0,81	-0,15 → 0,66	-31°
ST-35	Vòng hoa (héo) VongHoa_Heo	Đ2	0,25	-5,66	1,10×0,51×1,35	-0,15 → 1,20	179°

Vật thứ 36 → 79 / 79

Mã	Tên (tên trong Unity)	Đêm	Tâm X	Tâm Z	Rộng×Sâu×Cao (m)	Y đáy → đỉnh	Hướng
ST-36	Vòng hoa (héo) VongHoa_Heo	Đ2	1,50	−5,66	1,10×0,51×1,35	−0,15 → 1,20	-179°
ST-37	Vòng hoa (héo) VongHoa_Heo	Đ2	7,25	−5,66	1,10×0,51×1,35	−0,15 → 1,20	ra đường
ST-38	Chậu đốt vàng mã (tro) SM_BurnBasin_Ash	Đ2	7,30	−4,85	0,50×0,50×0,25	−0,15 → 0,10	trong
ST-39	Chống 8 ghế nhựa SM_PlasticChairStack_8	Đ2	2,30	−4,60	0,39×0,45×1,24	−0,15 → 1,09	trong
ST-40	Ghế nhựa xanh SM_PlasticChair_Green	Đ2	2,05	−3,29	0,39×0,43×0,81	−0,15 → 0,66	-49°
ST-41	Ghế nhựa đỏ SM_PlasticChair_Red	Đ2	6,08	−3,20	0,39×0,43×0,81	−0,15 → 0,66	-12°
ST-42	Ghế nhựa đỏ SM_PlasticChair_Red	Đ2	0,63	−3,04	0,39×0,43×0,81	−0,15 → 0,66	106°
ST-43	Bàn nhựa trái khân (nhận phúng viếng) SM_PlasticTable_TableCover	Đ2	1,32	−3,01	0,83×0,83×0,72	−0,15 → 0,57	-2°
ST-44	Bàn nhựa trái khân (nhận phúng viếng) SM_PlasticTable_TableCover	Đ2	6,21	−2,52	0,83×0,83×0,72	−0,06 → 0,66	2°
ST-45	Ghế nhựa xanh SM_PlasticChair_Green	Đ2	6,93	−2,55	0,39×0,43×0,81	−0,15 → 0,66	-53°
ST-46	Ghế nhựa đỏ SM_PlasticChair_Red	Đ2	1,43	−2,29	0,39×0,43×0,81	−0,15 → 0,66	-38°
ST-47	Chống 4 ghế nhựa SM_PlasticChairStack_4	Đ2	0,30	−1,90	0,39×0,43×0,99	−0,15 → 0,84	trong
ST-48	Ghế nhựa đỏ SM_PlasticChair_Red	Đ2	5,79	−1,83	0,39×0,43×0,81	−0,15 → 0,66	148°
ST-49	Vòng hoa (héo) VongHoa_Heo	Đ3	1,50	−5,66	1,10×0,51×1,35	−0,15 → 1,20	-179°
ST-50	Vòng hoa (héo) VongHoa_Heo	Đ3	7,25	−5,66	1,10×0,51×1,35	−0,15 → 1,20	ra đường
ST-51	Chậu đốt vàng mã (tro) SM_BurnBasin_Ash	Đ3	7,30	−4,85	0,50×0,50×0,25	0,05 → 0,30	trong
ST-52	Chống 8 ghế nhựa SM_PlasticChairStack_8	Đ3	2,30	−4,60	0,39×0,45×1,24	−0,15 → 1,09	trong
ST-53	Ghế nhựa xanh SM_PlasticChair_Green	Đ3	6,26	−3,13	0,39×0,43×0,81	−0,15 → 0,66	2°
ST-54	Bàn nhựa trái khân (nhận phúng viếng) SM_PlasticTable_TableCover	Đ3	6,22	−2,46	0,83×0,83×0,72	−0,09 → 0,63	-6°
ST-55	Chống 8 ghế nhựa SM_PlasticChairStack_8	Đ3	0,30	−1,90	0,39×0,45×1,24	−0,15 → 1,09	trong
ST-56	Chống 4 ghế nhựa SM_PlasticChairStack_4	Đ3	7,30	−1,90	0,39×0,43×0,99	−0,15 → 0,84	trong
ST-57	Ghế nhựa đỏ SM_PlasticChair_Red	Đ3	6,19	−1,74	0,39×0,43×0,81	−0,15 → 0,66	-157°
ĐỒ ĐẶT TRÊN BÀN / KỆ / GIƯỜNG							
ST-58	Hộp thư ở cổng HopThu_Cong		5,40	−5,45	0,25×0,10×0,12	1,09 → 1,21	ra đường
ST-59	Khay phong bì phúng viếng SM_EnvelopeTray_day		5,42	−3,98	0,28×0,20×0,06	0,57 → 0,63	trong
ST-60	Sổ phúng viếng SoPhungViengTang		5,78	−3,90	0,28×0,30×0,04	0,57 → 0,61	→ phải
ST-61	Khay trà ly thủy tinh KhayTra_LyThuyTinh	Đ1	1,31	−3,42	0,40×0,26×0,17	0,57 → 0,74	53°
ST-62	Đĩa kẹo bánh hạt dưa DiaKeoBanh_HatDua	Đ1	6,97	−3,03	0,52×0,46×0,07	0,57 → 0,64	-148°
ST-63	Đĩa kẹo bánh hạt dưa DiaKeoBanh_HatDua	Đ1	2,28	−2,13	0,52×0,46×0,07	0,57 → 0,64	106°
ST-64	Khay trà ly thủy tinh KhayTra_LyThuyTinh	Đ1	5,89	−2,07	0,40×0,26×0,17	0,57 → 0,74	159°
ST-65	Khay trà ly thủy tinh KhayTra_LyThuyTinh	Đ2	1,32	−3,01	0,40×0,26×0,17	0,57 → 0,74	-95°
ST-66	Đĩa kẹo bánh hạt dưa DiaKeoBanh_HatDua	Đ2	6,15	−2,53	0,52×0,46×0,07	0,66 → 0,73	-42°
ST-67	Khay trà ly thủy tinh KhayTra_LyThuyTinh	Đ3	6,23	−2,46	0,40×0,26×0,17	0,70 → 0,88	11°
ĐIỆN - ĐÈN - QUẠT							
ST-68	Chuông điện (nút bấm) ChuongDien_Nut		6,50	−5,41	0,07×0,02×0,11	1,34 → 1,46	ra đường


Mã	Tên (tên trong Unity)	Đêm	Tâm X	Tâm Z	Rộng×Sâu×Cao (m)	Y đáy → đỉnh	Hướng
ST-69	Đèn cổng chao tôn DenCong_ChaoTon		0,50	−0,47	0,41×0,54×0,22	2,56 → 2,78	ra đường
ST-70	Đèn cổng chao tôn DenCong_ChaoTon		7,05	−0,47	0,41×0,54×0,22	2,56 → 2,78	ra đường
ST-71	Hộp công tơ điện HopCongTo		7,30	−0,28	0,30×0,15×0,40	1,50 → 1,90	ra đường
ST-72	Đồng hồ nước (dưới hộp công tơ) DongHolNuoc_HopCong		7,30	−0,25	0,34×0,10×0,16	1,02 → 1,18	ra đường
CỬA, CỔNG, CỬA SỔ, RÈM							
ST-73	Trụ gạch cổng sắt CongSat_TruGach		2,20	−5,25	0,31×0,31×2,10	−0,15 → 1,95	trong
ST-74	Trụ gạch cổng sắt CongSat_TruGach		5,40	−5,25	0,31×0,31×2,10	−0,15 → 1,95	trong
ST-75	Trụ gạch cổng sắt CongSat_TruGach		6,50	−5,25	0,31×0,31×2,10	−0,15 → 1,95	trong
ST-76	Cửa ngách ở cổng CuaNgachCong (m[])		6,34	−4,80	0,90×0,03×1,80	−0,15 → 1,65	← trái
ST-77	Cánh cổng sắt trái (mở) CanhCong_Trai (m[])		2,53	−4,60	1,35×0,03×1,80	−0,15 → 1,65	104°
ST-78	Cánh cổng sắt phải (mở) CanhCong_Phai (m[])		5,07	−4,60	1,35×0,03×1,80	−0,15 → 1,65	-104°
KẾT CẤU PHỤ / CỐ ĐỊNH							
ST-79	Biển số nhà trắng men BienSoNha		2,20	−5,40	0,22×0,01×0,14	1,48 → 1,62	ra đường

Tầng 1 (±0,00) · 32 vật trong TB, TK



Mã	Tên (tên trong Unity)	Đềm	Tâm X	Tâm Z	Rộng×Sâu×Cao (m)	Y đáy → đỉnh	Hướng
ĐỒ ĐẶT TRÊN SÀN							
TB-01	Tủ kính 3 tầng (tiệm) TuKinh		-0,73	-3,90	1,60×0,65×1,20	0,00 → 1,20	← trái
TB-02	Kệ sắt V lỗ + đồ kệ KeVLo_DoKe		-0,58	-2,40	0,90×0,35×1,60	0,00 → 1,60	← trái
TB-03	Quầy hàng + ngăn kéo (lọ keo) LOC_CanhQuayHang		-3,30	-2,30	2,20×1,39×0,96	0,00 → 0,96	← trái
TB-04	Cân bàn (bán hàng) CanBanHang		-2,68	-0,78	0,32×0,32×0,45	0,00 → 0,45	trong
TB-05	Cụm thùng sơn ThungSon_Cum2		-0,76	0,21	1,02×0,68×0,73	-0,00 → 0,73	← trái
TB-06	Chống 4 ghế nhựa SM_PlasticChairStack_4		-3,00	1,12	0,39×0,43×0,99	0,00 → 0,99	trong
TB-07	Cuộn dây điện CuonDayDien		-2,05	1,30	0,12×0,53×0,42	0,00 → 0,42	trong
TB-08	Chống bao xi măng BaoXiHang_Chong		-0,72	1,26	0,71×0,53×0,74	0,00 → 0,74	← trái
TB-09	Bàn thờ Thần Tài BanThoThanTai		-3,88	1,62	0,47×0,37×1,08	0,00 → 1,08	ra đường
TK-01	Cuộn dây điện (2) CuonDayDien_2		-3,20	2,30	0,67×0,39×0,44	0,00 → 0,44	trong
TK-02	Bao tải rộng BaoTaiRong		-1,55	2,39	0,52×0,42×0,23	0,00 → 0,23	-10°
TK-03	Chống bao xi măng (2) BaoXiHang_Chong2		-0,75	2,50	0,72×0,50×0,48	0,00 → 0,48	← trái
TK-04	Bụi xi măng trên sàn BuiXiHang_San		-2,30	3,00	1,34×0,94×0,00	0,00 → 0,00	trong
TK-05	Bao xi măng lẻ BaoXiHang_Le		-1,50	3,20	0,77×0,67×0,11	-0,00 → 0,11	20°
TK-06	Kệ gỗ dài (kho) KeGoDai		-3,99	3,40	2,20×0,42×1,20	0,00 → 1,20	→ phải
TK-07	Xe rửa XeRua		-2,30	4,10	0,66×1,86×0,84	-0,00 → 0,84	30°
TK-08	Bó thanh sắt ThanhSat_Bo		-0,60	4,30	0,31×0,20×2,40	-0,00 → 2,40	← trái
TK-09	Cây chổi CayChoi		-1,57	4,47	0,10×0,22×1,38	0,00 → 1,38	trong
TK-10	Cuộn lưới thép CuonLuoiTiep		-0,75	5,20	1,22×0,59×0,97	-0,00 → 0,97	← trái
TK-11	Thang nhôm ThangNhom		-4,12	5,30	0,38×0,12×1,80	0,00 → 1,80	→ phải
TK-12	Chống gạch mẫu GachMau_Chong		-3,40	5,55	0,29×0,25×0,16	0,00 → 0,16	trong
TK-13	Thùng gỗ ThungGo		-2,80	5,70	0,52×0,40×0,43	0,00 → 0,43	15°
TK-14	Thùng sơn ThungSon		-0,80	6,40	0,69×0,48×0,73	0,00 → 0,73	← trái
TK-15	Bó ống nước (kho) ongNuoc_Bo		-3,90	6,45	0,53×0,34×2,00	0,00 → 2,00	trong
TK-16	Ống nước nằm (kho) ongNuoc_Nam		-2,15	6,45	2,09×0,35×0,13	0,00 → 0,13	trong
ĐỒ ĐẶT TRÊN BÀN / KỆ / GIƯỜNG							
TB-10	Sổ hoá đơn trên quầy SoHoaDon_Quay		-3,31	-2,98	0,50×0,25×0,08	0,95 → 1,03	10°
TREO TƯỜNG / TREO TRẦN							
TB-11	Bảng giá viết tay BangGia		-0,41	-3,20	0,36×0,00×0,26	1,64 → 1,90	← trái
TB-12	Lịch bloc công ty vật liệu LichBloc_CongTy		-4,19	-3,00	0,32×0,02×0,54	1,77 → 2,31	→ phải
TB-13	Đồng hồ treo tường (tiệm) DongHoTreo_Tiem		-0,43	-2,50	0,34×0,06×0,34	2,18 → 2,52	← trái
ĐIỆN - ĐÈN - QUẠT							
TB-14	Đèn tuýp máng 1,2 m DenTuyt_120		-2,30	-2,00	1,22×0,07×0,06	3,54 → 3,60	→ phải
TB-15	Quạt bàn sắt cũ QuatBan_SatCu		-3,30	-1,50	0,39×0,27×0,55	0,95 → 1,50	→ phải
CỬA, CỔNG, CỬA SỔ, RÈM							
TB-16	Cửa sắt xếp mặt tiền tiệm CuaSatXep_Dong		-2,30	-5,30	3,66×0,04×2,41	0,00 → 2,41	trong

Tầng 1 (±0,00) · 68 vật trong PK

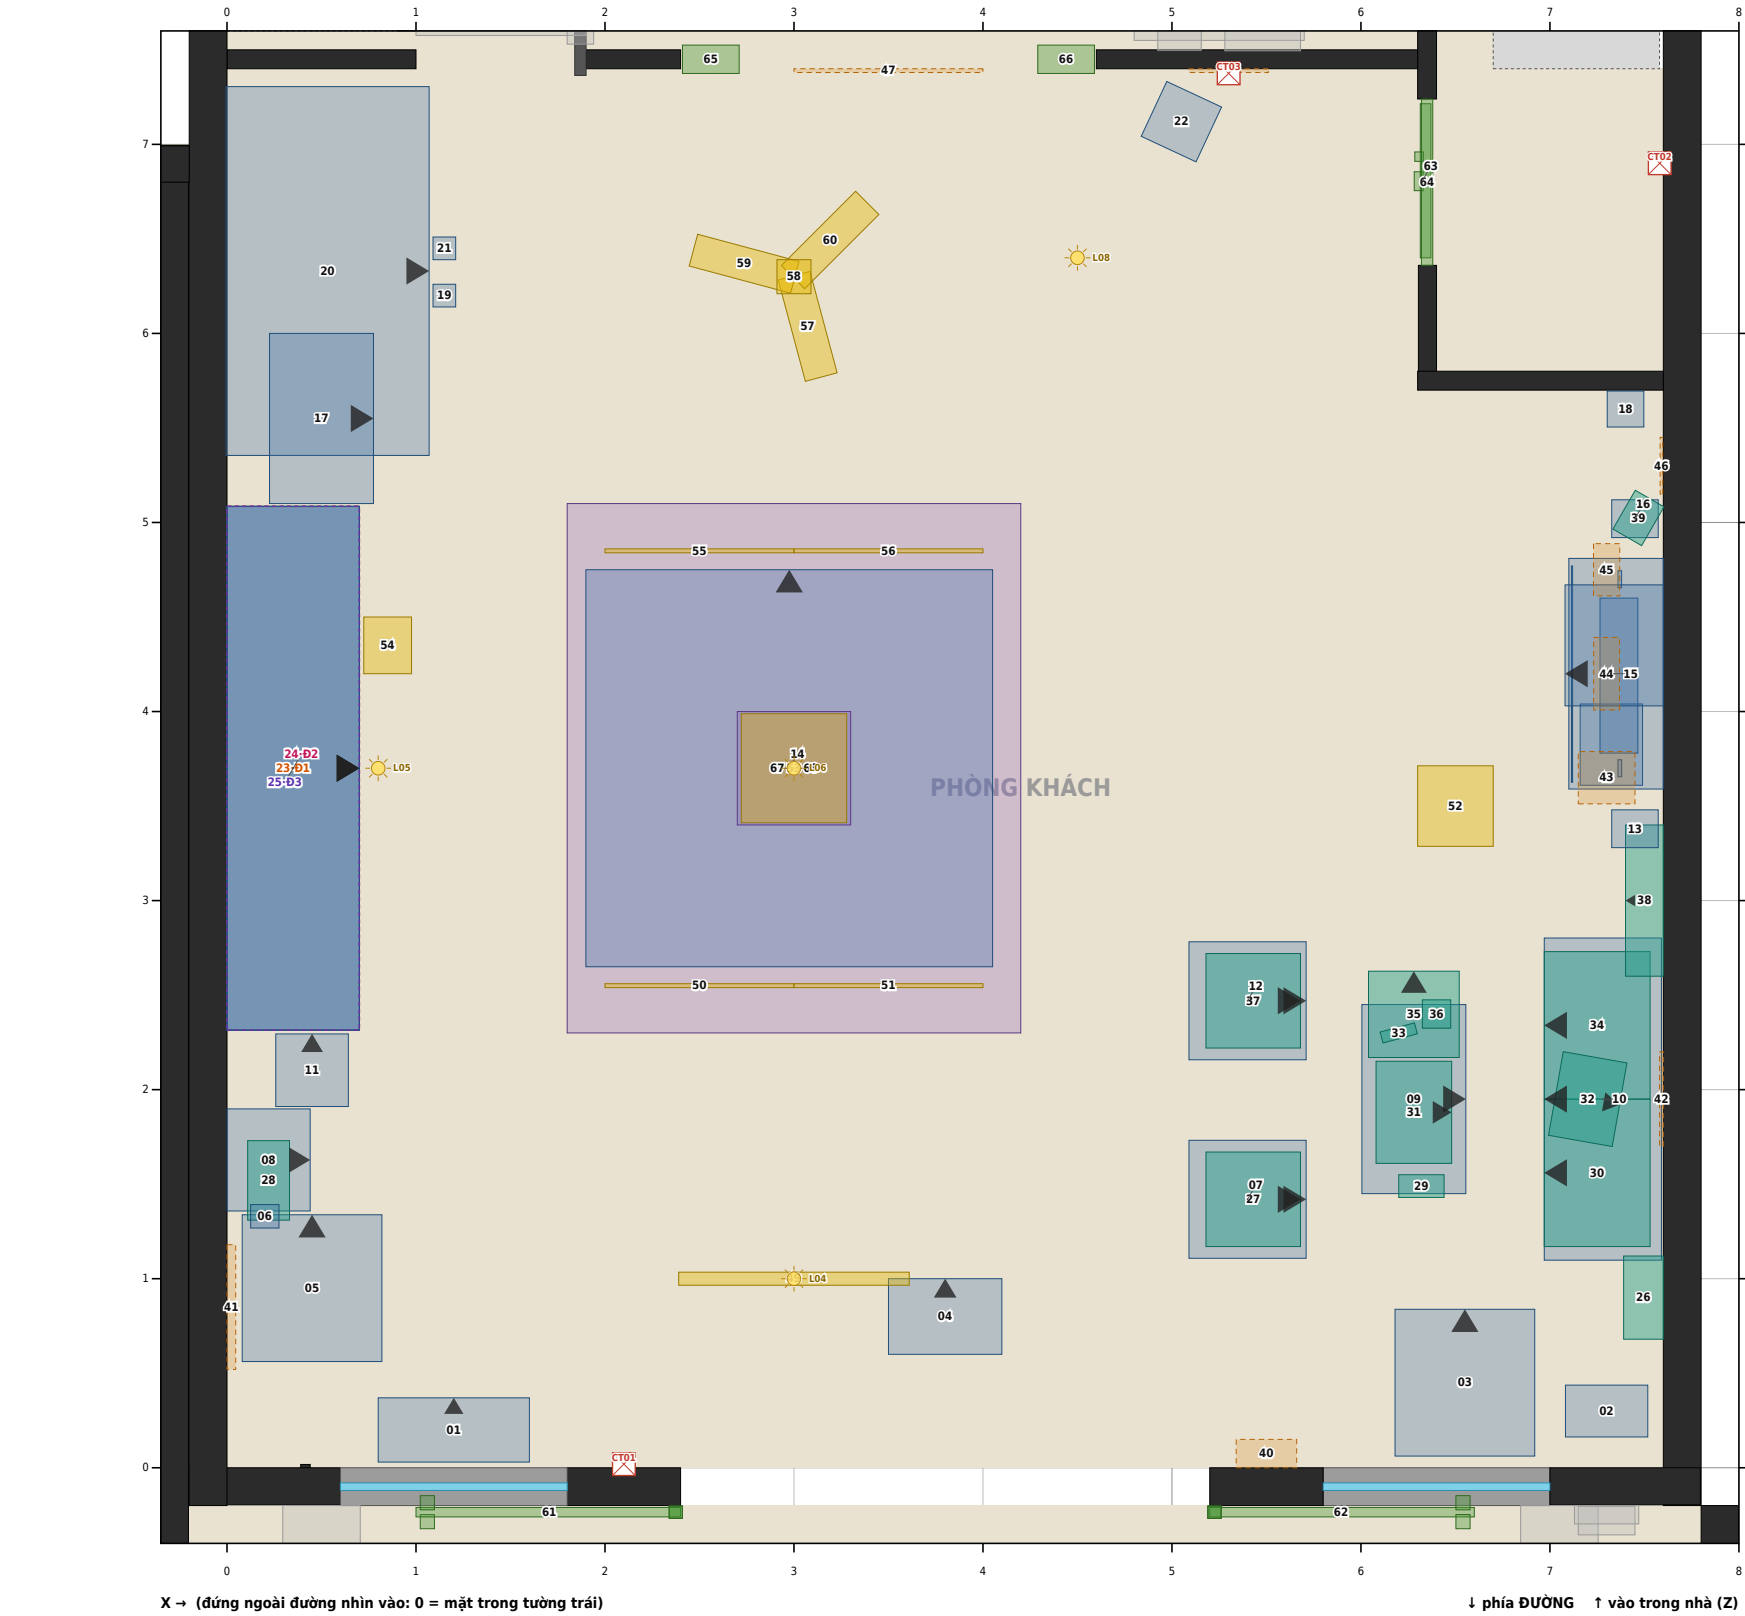

CHÚ GIẢI

- Đồ đặt trên sàn

Điện - đèn - quạt

Tường (cắt ở 1,5 m)

Cổng tắc / ổ cắm (CT..)

Đ1: chỉ có ở Đệm 1

Đồ đặt trên bàn / kệ / giường

Cửa, cổng, cửa sổ, rèm

Bậu / tường thấp

Nguồn sáng (L..)

Đ2: chỉ có ở Đệm 2

Treo tường / treo trần

Kết cấu phụ / cố định

Kính

mặt trước của vật


Đ3: chỉ có ở Đệm 3
- | Mã | Tên (tên trong Unity) | Đềm | Tâm X | Tâm Z | Rộng×Sâu×Cao (m) | Y đáy → đỉnh | Hướng |
|-------------------------------|--|-----|-------|-------|------------------|--------------|--------|
| ĐỒ ĐẶT TRÊN SÀN | | | | | | | |
| PK-01 | Kệ giày chân cầu thang
KeGiay_ChanCau | | 1,20 | 0,20 | 0,80×0,34×0,62 | 0,00 → 0,62 | trong |
| PK-02 | Chổi quét + ky hốt rác
ChoiQuet_Ky | | 7,30 | 0,30 | 0,44×0,27×1,30 | 0,00 → 1,30 | trong |
| PK-03 | Chậu cây kiếng lá to
ChauCayKieng_LaTo | | 6,55 | 0,45 | 0,74×0,78×1,17 | 0,00 → 1,17 | trong |
| PK-04 | Thảm chùi chân (cửa)
ThamChuiChan_Cua | | 3,80 | 0,80 | 0,60×0,40×0,02 | 0,00 → 0,02 | trong |
| PK-05 | Chậu cây kiếng lá to
ChauCayKieng_LaTo | | 0,45 | 0,95 | 0,74×0,78×1,17 | 0,00 → 1,17 | trong |
| PK-06 | Tập giấy + bút bi
LOC_TapGiay_ButBi | | 0,20 | 1,33 | 0,12×0,15×0,02 | 0,00 → 0,02 | → phải |
| PK-07 | Ghế salon đơn
Salon_GheDon | | 5,40 | 1,42 | 0,62×0,62×0,90 | 0,00 → 0,90 | → phải |
| PK-08 | Bàn nhỏ đặt máy điện thoại
LOC_BanNhoBatMay | | 0,22 | 1,63 | 0,54×0,44×0,72 | -0,00 → 0,72 | → phải |
| PK-09 | Bàn nước salon
Salon_BanNuoc | | 6,28 | 1,95 | 1,00×0,55×0,46 | 0,00 → 0,46 | → phải |
| PK-10 | Ghế salon dài
Salon_GheDai | | 7,28 | 1,95 | 1,70×0,62×0,90 | 0,00 → 0,90 | ← trái |
| PK-11 | Bình hoa gốm lớn
BinhHoaLon_Gom | | 0,45 | 2,10 | 0,38×0,38×0,80 | 0,00 → 0,80 | trong |
| PK-12 | Ghế salon đơn
Salon_GheDon | | 5,40 | 2,47 | 0,62×0,62×0,90 | 0,00 → 0,90 | → phải |
| PK-13 | Loa thùng
Loa_Thung | | 7,45 | 3,38 | 0,20×0,25×0,34 | 0,00 → 0,34 | ← trái |
| PK-14 | Quan tài (LỘC) — đầu về phía bàn t...
QuanTai_LOC | | 2,98 | 3,70 | 2,15×2,10×1,30 | 0,00 → 1,30 | trong |
| PK-15 | Tủ TV đứng + TV, VCD, loa
TuTV_Dung_Bo | | 7,34 | 4,20 | 1,22×0,52×1,90 | 0,00 → 1,90 | ← trái |
| PK-16 | Loa thùng
Loa_Thung | | 7,45 | 5,02 | 0,20×0,25×0,34 | 0,00 → 0,34 | ← trái |
| PK-17 | Chiếu + mền khách ngủ lại
ChieuMen_Khach0 | | 0,50 | 5,55 | 0,90×0,55×0,31 | 0,15 → 0,46 | → phải |
| PK-18 | Chổi lông gà
CayChoiLongGa | | 7,40 | 5,60 | 0,19×0,19×0,64 | 0,00 → 0,64 | trong |
| PK-19 | Bát gạo (đồ cúng)
LOC_BatGao | | 1,15 | 6,20 | 0,12×0,12×0,08 | -0,00 → 0,08 | trong |
| PK-20 | Đồng đồ cúng đám tang
LOC_DongDoCungTang | | 0,53 | 6,33 | 1,95×1,07×0,52 | 0,00 → 0,52 | → phải |
| PK-21 | Bát muối (đồ cúng)
LOC_BatMuoi | | 1,15 | 6,45 | 0,12×0,12×0,07 | -0,00 → 0,07 | trong |
| PK-22 | Ghế đầu gỗ
GheDau_Go | | 5,05 | 7,12 | 0,32×0,32×0,44 | 0,00 → 0,44 | 25° |
| PK-23 | Bàn thờ vong — Đềm 1
BanThoVong_Dem1 | Đ1 | 0,35 | 3,70 | 2,77×0,70×1,70 | 0,00 → 1,70 | → phải |
| PK-24 | Bàn thờ vong — Đềm 2
BanThoVong_Dem2 | Đ2 | 0,35 | 3,70 | 2,77×0,70×1,70 | 0,00 → 1,70 | → phải |
| PK-25 | Bàn thờ vong — Đềm 3
BanThoVong_Dem3 | Đ3 | 0,35 | 3,70 | 2,77×0,70×1,70 | 0,00 → 1,70 | → phải |
| ĐỒ ĐẶT TRÊN BÀN / KỆ / GIƯỜNG | | | | | | | |
| PK-26 | Nón lá treo tường
NonLa_TreoTuong | | 7,50 | 0,90 | 0,44×0,21×0,44 | 1,33 → 1,77 | ← trái |
| PK-27 | Đệm ghế đơn
Salon_Dem_NgoiDon | | 5,43 | 1,42 | 0,50×0,50×0,07 | 0,42 → 0,49 | → phải |
| PK-28 | Điện thoại bàn (trọn bộ)
LOC_DienThoai_TronBo | | 0,22 | 1,52 | 0,42×0,22×0,07 | 0,72 → 0,79 | → phải |
| PK-29 | Hộp khăn giấy nhưa
HopKhanGiay_Nhua | | 6,32 | 1,49 | 0,24×0,12×0,14 | 0,46 → 0,60 | trong |
| PK-30 | Đệm ghế dài (phía kia)
Salon_Dem_NgoiDai_Kia | | 7,25 | 1,56 | 0,78×0,56×0,07 | 0,42 → 0,49 | ← trái |
| PK-31 | Khay ấm chén
KhayAmChen | | 6,28 | 1,88 | 0,54×0,40×0,30 | 0,46 → 0,76 | → phải |
| PK-32 | Bảo củ trên bàn
BaoCu_TrenBan | | 7,20 | 1,95 | 0,45×0,34×0,03 | 0,42 → 0,45 | 100° |
| PK-33 | Điều khiển bọc nilon
DieuKien | | 6,20 | 2,30 | 0,06×0,19×0,03 | 0,47 → 0,50 | 75° |
| PK-34 | Đệm ghế dài (gắn TV)
Salon_Dem_NgoiDai_GanTV | | 7,25 | 2,34 | 0,78×0,56×0,07 | 0,42 → 0,49 | ← trái |
- Nguồn: scene Assets/Scenes/LOC_NhaLoc.unity (dựng 30/09/2026 17:09) — tọa độ Unity thế giới, đơn vị mét. X: ngang · Z: chiều sâu · Y: cao độ (sàn T1 = 0).
- Mã vật = mã phòng + số thứ tự (PK-07...). Đ1/Đ2/Đ3 = vật chỉ có ở Đềm 1/2/3. Kích thước = khung bao của mesh thật (.glb).

Vật thứ 35 → 68 / 68

Mã	Tên (tên trong Unity)	Đêm	Tâm X	Tâm Z	Rộng×Sâu×Cao (m)	Y đáy → đỉnh	Hướng
PK-35	Khay hoa quả nhựa KhayHoaQua_Nhua		6,28	2,40	0,48×0,46×0,12	0,46 → 0,58	trong
PK-36	Gạt tàn thủy tinh GatTan_ThuyTinh		6,40	2,40	0,15×0,15×0,05	0,53 → 0,58	trong
PK-37	Đệm ghế đơn Salon_Dem_NgoiDon		5,43	2,47	0,50×0,50×0,07	0,42 → 0,49	→ phải
PK-38	Kệ gỗ treo tường KeGo_TreoTuong		7,50	3,00	0,80×0,20×0,67	1,38 → 2,05	← trái
PK-39	Hộp băng cassette BangCassette_Hop		7,47	5,02	0,24×0,18×0,02	0,34 → 0,36	-60°
TREO TƯỜNG / TREO TRẦN							
PK-40	Đồng hồ quả lắc DongHoQuaLac		5,50	0,07	0,32×0,15×0,79	1,60 → 2,40	trong
PK-41	Tranh sơn thủy (khung) TranhSonThuy_Khung		0,02	0,85	0,66×0,05×0,46	1,55 → 2,01	→ phải
PK-42	Ảnh gia đình 1997 (khung treo) AnhGiaDinh_Tex		7,59	1,95	0,50×0,02×0,40	1,60 → 2,00	← trái
PK-43	Lọ hoa giả nhựa LoHoaGia_Nhua		7,30	3,65	0,30×0,28×0,80	1,90 → 2,70	trong
PK-44	Radio cassette 2 loa RadioCassette_2Loa		7,30	4,20	0,38×0,14×0,49	1,90 → 2,39	← trái
PK-45	Đĩa VCD xếp chồng DiaVCD_XepChong		7,30	4,75	0,28×0,14×0,07	1,90 → 1,97	→ phải
PK-46	Lịch tháng 8/2002 LichThang8_2002		7,59	5,30	0,30×0,01×0,47	1,39 → 1,85	← trái
PK-47	Tranh thêu thuyền buồm TranhTheu_Tex		3,50	7,39	1,00×0,02×0,50	2,45 → 2,95	ra đường
PK-48	Bằng "Gia đình văn hoá" BangGDVH_Tex		5,30	7,39	0,42×0,02×0,30	1,95 → 2,25	ra đường
ĐIỆN - ĐÈN - QUẠT							
PK-49	Đèn tuýp máng 1,2 m DenTuyp_120		3,00	1,00	1,22×0,07×0,06	3,14 → 3,20	trong
PK-50	Đèn hắt trần (ống) DenHat_Ong		2,50	2,55	1,00×0,02×0,02	3,14 → 3,16	trong
PK-51	Đèn hắt trần (ống) DenHat_Ong		3,50	2,55	1,00×0,02×0,02	3,14 → 3,16	trong
PK-52	Quạt cây (nguyên bộ) QuatCay_NguyenBo		6,50	3,50	0,40×0,43×1,27	0,00 → 1,27	trong
PK-53	Đèn chùm 5 tay DenChum_5Tay		3,00	3,70	0,56×0,58×0,60	2,60 → 3,20	trong
PK-54	Ổ cắm kéo dài OCamKeoDai		0,85	4,35	0,25×0,30×0,06	−0,00 → 0,06	trong
PK-55	Đèn hắt trần (ống) DenHat_Ong		2,50	4,85	1,00×0,02×0,02	3,14 → 3,16	trong
PK-56	Đèn hắt trần (ống) DenHat_Ong		3,50	4,85	1,00×0,02×0,02	3,14 → 3,16	trong
PK-57	Quạt trần — cánh QuatTran_Canh		3,07	6,04	0,56×0,17×0,01	3,02 → 3,04	-105°
PK-58	Quạt trần — thân QuatTran_Than		3,00	6,30	0,18×0,18×0,22	2,98 → 3,20	trong
PK-59	Quạt trần — cánh QuatTran_Canh		2,74	6,37	0,56×0,17×0,01	3,02 → 3,04	15°
PK-60	Quạt trần — cánh QuatTran_Canh		3,19	6,49	0,56×0,17×0,01	3,02 → 3,04	135°
CỬA, CỔNG, CỬA SỔ, RÈM							
PK-61	Cửa chính — cánh trái (mở ra ngoài) CuaChinh_Trai (mở ra ngoài)		1,71	−0,23	1,41×0,18×2,60	0,00 → 2,60	ra đường
PK-62	Cửa chính — cánh phải (mở ra ngoài) CuaChinh_Phai (mở ra ngoài)		5,89	−0,23	1,41×0,18×2,60	0,00 → 2,60	trong
PK-63	Cửa sắt hầm CuaSatHam (mở)		6,33	6,81	0,81×0,09×1,90	0,00 → 1,90	← trái
PK-64	Khung cửa sắt hầm KhungCuaSatHam		6,35	6,80	0,88×0,06×1,96	0,00 → 1,96	→ phải
PK-65	Rèm hạt nhựa Rem_Hat		2,56	7,45	0,30×0,15×2,10	0,10 → 2,20	trong
PK-66	Rèm hạt nhựa Rem_Hat		4,44	7,45	0,30×0,15×2,10	0,10 → 2,20	trong

Mã	Tên (tên trong Unity)	Đêm	Tâm X	Tâm Z	Rộng×Sâu×Cao (m)	Y đáy → đỉnh	Hướng
KẾT CẤU PHỤ / CỐ ĐỊNH							
PK-67	Trần thạch cao giật cấp TranGiatCap_Khung		3,00	3,70	2,40×2,80×0,15	3,05 → 3,20	trong
PK-68	Hoa trần (phào trang trí) HoaTran		3,00	3,70	0,60×0,60×0,01	3,19 → 3,20	trong

Tầng 1 (±0,00) · 27 vật trong SS

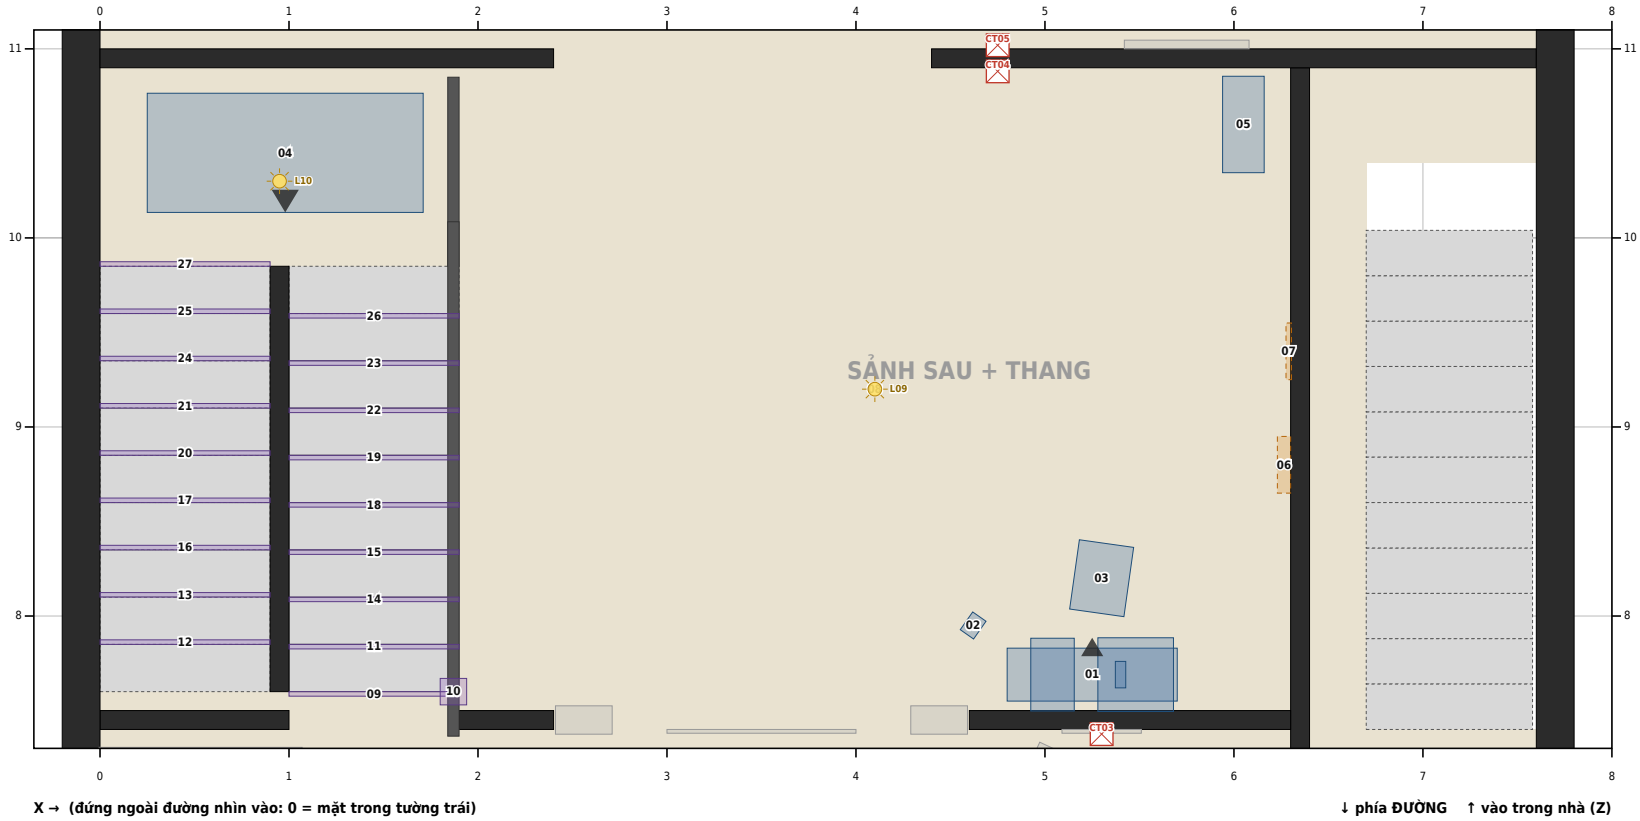

CHÚ GIẢI

- Đồ đặt trên sàn

Điện - đèn - quạt

Tường (cắt ở 1,5 m)

Cổng tắc / ổ cắm (CT..)

Đ1: chỉ có ở Đệm 1

Đồ đặt trên bàn / kệ / giường

Cửa, cổng, cửa sổ, rèm

Bậu / tường thấp

Nguồn sáng (L..)

Đ2: chỉ có ở Đệm 2

Treo tường / treo trần

Kết cấu phụ / cố định

Kính

▲ mặt trước của vật

Đ3: chỉ có ở Đệm 3
- | Mã | Tên (tên trong Unity) | Đêm | Tâm X | Tâm Z | Rộng×Sâu×Cao (m) | Y đáy → đỉnh | Hướng |
|------------------------|---|-----|-------|-------|------------------|--------------|----------|
| ĐỒ ĐẶT TRÊN SÀN | | | | | | | |
| SS-01 | Giá dép
GiaDep_Bo | | 5,25 | 7,69 | 0,90×0,39×0,56 | 0,00 → 0,56 | trong |
| SS-02 | Dép của Nhím (roi)
Dep_Nhim_Roi | | 4,62 | 7,95 | 0,09×0,11×0,02 | 0,00 → 0,02 | 35° |
| SS-03 | Dép khách
Dep_Khach | | 5,30 | 8,20 | 0,29×0,37×0,05 | 0,00 → 0,05 | 8° |
| SS-04 | Xe đạp cũ của Khôi
XeDap_Khoi | | 0,98 | 10,45 | 1,46×0,63×0,95 | 0,00 → 0,95 | ra đường |
| SS-05 | Chổi lau nhà + xô
ChoiLau_Gop | | 6,05 | 10,60 | 0,51×0,22×1,10 | -0,00 → 1,10 | ← trái |
| TREO TƯỜNG / TREO TRẦN | | | | | | | |
| SS-06 | Bảng điện chính (cầu dao, cầu chì)
BangDienChinh | | 6,26 | 8,80 | 0,30×0,07×0,45 | 1,59 → 2,05 | → phải |
| SS-07 | Móc chìa khoá (thiếu một chùm)
MocChiaKhoa | | 6,29 | 9,40 | 0,30×0,03×0,10 | 1,45 → 1,55 | ← trái |
| DIỆN - ĐÈN - QUẠT | | | | | | | |
| SS-08 | Bóng đèn compact
BongCompact | | 4,10 | 9,20 | 0,04×0,03×0,13 | 3,07 → 3,20 | trong |
| KẾT CẤU PHỤ / CỐ ĐỊNH | | | | | | | |
| SS-09 | Mũi bậc bo tròn (mòn)
MuiBac_Mon | | 1,45 | 7,59 | 0,90×0,02×0,02 | 0,15 → 0,17 | trong |
| SS-10 | Trụ đầu thang gỗ tiện
TruDauThang | | 1,87 | 7,60 | 0,14×0,14×0,95 | 0,00 → 0,95 | trong |
| SS-11 | Mũi bậc bo tròn (mòn)
MuiBac_Mon | | 1,45 | 7,84 | 0,90×0,02×0,02 | 0,32 → 0,34 | trong |
| SS-12 | Mũi bậc bo tròn (mòn)
MuiBac_Mon | | 0,45 | 7,86 | 0,90×0,02×0,02 | 3,21 → 3,23 | ra đường |
| SS-13 | Mũi bậc bo tròn (mòn)
MuiBac_Mon | | 0,45 | 8,11 | 0,90×0,02×0,02 | 3,04 → 3,06 | ra đường |
| SS-14 | Mũi bậc bo tròn (mòn)
MuiBac_Mon | | 1,45 | 8,09 | 0,90×0,02×0,02 | 0,49 → 0,51 | trong |
| SS-15 | Mũi bậc bo tròn (mòn)
MuiBac_Mon | | 1,45 | 8,34 | 0,90×0,02×0,02 | 0,66 → 0,68 | trong |
| SS-16 | Mũi bậc bo tròn (mòn)
MuiBac_Mon | | 0,45 | 8,36 | 0,90×0,02×0,02 | 2,87 → 2,89 | ra đường |
| SS-17 | Mũi bậc bo tròn (mòn)
MuiBac_Mon | | 0,45 | 8,61 | 0,90×0,02×0,02 | 2,70 → 2,72 | ra đường |
| SS-18 | Mũi bậc bo tròn (mòn)
MuiBac_Mon | | 1,45 | 8,59 | 0,90×0,02×0,02 | 0,83 → 0,85 | trong |
| SS-19 | Mũi bậc bo tròn (mòn)
MuiBac_Mon | | 1,45 | 8,84 | 0,90×0,02×0,02 | 1,00 → 1,02 | trong |
| SS-20 | Mũi bậc bo tròn (mòn)
MuiBac_Mon | | 0,45 | 8,86 | 0,90×0,02×0,02 | 2,53 → 2,55 | ra đường |
| SS-21 | Mũi bậc bo tròn (mòn)
MuiBac_Mon | | 0,45 | 9,11 | 0,90×0,02×0,02 | 2,36 → 2,38 | ra đường |
| SS-22 | Mũi bậc bo tròn (mòn)
MuiBac_Mon | | 1,45 | 9,09 | 0,90×0,02×0,02 | 1,17 → 1,19 | trong |
| SS-23 | Mũi bậc bo tròn (mòn)
MuiBac_Mon | | 1,45 | 9,34 | 0,90×0,02×0,02 | 1,34 → 1,36 | trong |
| SS-24 | Mũi bậc bo tròn (mòn)
MuiBac_Mon | | 0,45 | 9,36 | 0,90×0,02×0,02 | 2,19 → 2,21 | ra đường |
| SS-25 | Mũi bậc bo tròn (mòn)
MuiBac_Mon | | 0,45 | 9,61 | 0,90×0,02×0,02 | 2,02 → 2,04 | ra đường |
| SS-26 | Mũi bậc bo tròn (mòn)
MuiBac_Mon | | 1,45 | 9,59 | 0,90×0,02×0,02 | 1,51 → 1,53 | trong |
| SS-27 | Mũi bậc bo tròn (mòn)
MuiBac_Mon | | 0,45 | 9,86 | 0,90×0,02×0,02 | 1,85 → 1,87 | ra đường |
- Nguồn: scene Assets/Scenes/LOC_NhaLoc.unity (dựng 30/09/2026 17:09) — toạ độ Unity thế giới, đơn vị mét. X: ngang · Z: chiều sâu · Y: cao độ (sàn T1 = 0).
- Mã vật = mã phòng + số thứ tự (PK-07...). Đ1/Đ2/Đ3 = vật chỉ có ở Đệm 1/2/3. Kích thước = khung bao của mesh thật (.glb).

Tầng 1 (±0,00) · 56 vật trong BA



Mã	Tên (tên trong Unity)	Đềm	Tâm X	Tâm Z	Rộng×Sâu×Cao (m)	Y đáy → đỉnh	Hướng
ĐỒ ĐẶT TRÊN SÀN							
BA-01	Tủ lạnh một cánh TuLanh_Bo		7,23	11,50	0,58×0,74×1,45	0,00 → 1,45	← trái
BA-02	Hũ / bình ngâm rượu HuBinhNgamRuou		0,30	11,55	0,56×0,48×0,48	0,00 → 0,48	→ phải
BA-03	Bát đĩa trong chạn Chan_BatĐĩaTrongChan		0,25	12,65	0,90×0,47×1,60	−0,00 → 1,60	→ phải
BA-04	Chống (bó) tre ChongTre		6,95	13,10	1,90×0,86×0,48	0,00 → 0,48	→ phải
BA-05	Rổ rá + thớt RoRaThit		1,30	13,30	0,96×0,41×0,32	0,00 → 0,32	trong
BA-06	Bộ mĩa BoMia		0,12	13,55	0,11×0,11×1,10	−0,00 → 1,10	trong
BA-07	Ghế ăn (bố) GheAn_bo		4,25	13,89	0,40×0,44×0,85	0,00 → 0,85	trong
BA-08	Rổ rau quả RauQua_Ro		0,55	14,10	0,38×0,38×0,17	0,00 → 0,17	trong
BA-09	Ghế đầu gỗ GheDau_Go		1,10	14,15	0,32×0,32×0,44	0,00 → 0,44	20°
BA-10	Thùng rác ThungRac		0,20	14,60	0,30×0,27×0,32	0,00 → 0,32	→ phải
BA-11	Ghế ăn (mẹ) GheAn_me		3,34	14,60	0,40×0,44×0,85	0,00 → 0,85	→ phải
BA-12	Bộ bàn ăn + ghế BanAn_Bo		4,25	14,60	1,20×0,81×0,76	0,00 → 0,76	trong
BA-13	Ghế ăn (Khôi) GheAn_khoi		5,16	14,60	0,40×0,44×0,85	0,00 → 0,85	← trái
BA-14	Tủ chạn chén bát TuBuffet_ChenBat		7,32	14,95	1,04×0,47×1,78	0,00 → 1,78	← trái
BA-15	Bệ rửa xây + chậu inox + vòi BeRua_Bo		0,31	15,30	0,80×0,61×0,97	0,00 → 0,97	→ phải
BA-16	Ghế ăn (Nhím) GheAn_nhim		4,25	15,31	0,40×0,44×0,85	0,00 → 0,85	ra đường
BA-17	Xô chậu khăn lau XoChauKhauLau		7,20	15,80	0,32×0,32×0,33	0,00 → 0,33	trong
BA-18	Chậu cây kiếng lá to ChauCayKieng_LaTo		6,15	16,00	0,74×0,78×1,17	0,00 → 1,17	trong
BA-19	Mặt bếp xây 1,80 m MatBepXay_180		0,92	16,10	1,80×0,60×0,80	−0,00 → 0,80	ra đường
BA-20	Bình gas BinhGas		2,05	16,15	0,30×0,30×0,60	0,00 → 0,60	trong
BA-21	Thùng gạo nhựa ThungGao_Nhua		2,65	16,05	0,46×0,44×0,60	0,00 → 0,60	trong
ĐỒ ĐẶT TRÊN BÀN / KỆ / GIƯỜNG							
BA-22	Phích (bình thủy) nước BinhThuy_Phich		7,25	11,50	0,26×0,20×0,42	1,30 → 1,72	trong
BA-23	Móc áo + khăn tắm MocAo_KhanTam		0,05	11,58	0,59×0,10×0,41	1,23 → 1,64	→ phải
BA-24	Bát đĩa úp trên bàn BatDia_DangUp_Ban		6,95	13,10	0,48×0,34×0,12	0,43 → 0,55	trong
BA-25	Cốc bàn chải (trẻ em) CocBanChai_TreEm		0,28	15,00	0,07×0,06×0,22	0,80 → 1,02	trong
BA-26	Bát đĩa trong chậu BatDia_TrongChau		0,40	15,15	0,22×0,22×0,09	0,80 → 0,89	→ phải
BA-27	Giá bát úp GiaBatUp		0,35	15,55	0,51×0,31×0,20	0,80 → 1,00	→ phải
BA-28	Phích vô sắt hoa PhichHoa		1,74	15,98	0,16×0,12×0,34	0,77 → 1,10	ra đường
BA-29	Nồi cháo NoiChao_Rong		0,52	16,10	0,36×0,28×0,15	0,83 → 0,98	ra đường
BA-30	Bếp gas đôi BepGas_Doi		0,70	16,10	0,73×0,48×0,07	0,77 → 0,83	ra đường
BA-31	Ấm nhôm AmNhom		0,90	16,10	0,39×0,17×0,18	0,82 → 0,99	trong
BA-32	Lon sữa đặc đựng bút LonSuaDac_DungBut		1,15	16,10	0,12×0,12×0,26	0,80 → 1,06	trong
BA-33	Nồi cơm điện NoiComDien		1,50	16,10	0,29×0,37×0,23	0,77 → 0,99	ra đường
BA-34	Thanh treo dụng cụ bếp ThanhTreoDungCu_Bep		2,50	16,34	0,80×0,11×0,39	1,37 → 1,76	ra đường

Vật thứ 35 → 56 / 56


Mã	Tên (tên trong Unity)	Đêm	Tâm X	Tâm Z	Rộng×Sâu×Cao (m)	Y đáy → đỉnh	Hướng
BA-35	Túi gia vị treo TuiGiaVi_Treo		1,85	16,37	0,32×0,06×0,36	1,20 → 1,56	ra đường
BA-36	Bát cháo ăn BatChao_An	Đ1	3,90	14,60	0,15×0,10×0,06	0,84 → 0,90	trong
BA-37	Lồng bàn nhựa LongBan	Đ1	4,25	14,60	0,45×0,48×0,26	0,79 → 1,05	trong
BA-38	Bát cháo ăn BatChao_An	Đ1	4,60	14,60	0,15×0,10×0,05	0,79 → 0,85	trong
BA-39	Bát cháo ăn BatChao_An	Đ2	3,90	14,60	0,15×0,10×0,05	0,79 → 0,84	trong
BA-40	Lồng bàn nhựa LongBan	Đ2	4,25	14,60	0,45×0,48×0,26	0,79 → 1,05	trong
BA-41	Bát cháo ăn BatChao_An	Đ2	4,60	14,60	0,15×0,10×0,06	0,84 → 0,90	trong
BA-42	Mâm đồ cúng mặn (Đêm 3) MamDoCungMan	Đ3	4,25	14,60	0,84×0,84×0,30	0,76 → 1,05	trong
TREO TƯỜNG / TREO TRẦN							
BA-43	Tranh hoa sen (khung) TranhHoaSen_Khung		5,75	11,02	0,66×0,05×0,46	1,55 → 2,01	trong
BA-44	Hộp bánh quy thiếc (tái dụng) HopBanhQuy_ThiecTaiDung		0,28	12,40	0,19×0,19×0,11	1,60 → 1,71	trong
BA-45	Đồng hồ treo vuông DongHoTreo_Vuong		7,56	12,50	0,30×0,09×0,30	2,05 → 2,35	← trái
BA-46	Chai nước mắm, lọ gia vị ChaiNuocMam_Lo		0,25	12,95	0,34×0,08×0,27	1,60 → 1,87	→ phải
BA-47	Lịch bloc (5/8) LichBloc		7,59	14,00	0,20×0,03×0,28	1,32 → 1,60	← trái
BA-48	Túi nilon treo TuiNilon_Treo		0,03	14,30	0,20×0,10×0,31	1,49 → 1,80	→ phải
BA-49	Kệ chén treo tường KeChenTreoTuong		0,11	15,20	0,90×0,22×0,59	1,59 → 2,18	→ phải
ĐIỆN - ĐÈN - QUẠT							
BA-50	Đèn tuýp máng 1,2 m DenTuyp_120		3,80	13,70	1,22×0,07×0,06	3,14 → 3,20	trong
BA-51	Ổ cắm đôi OCam_Doi		2,40	16,39	0,01×0,07×0,07	1,05 → 1,12	ra đường
CỬA, CỔNG, CỬA SỔ, RÈM							
BA-52	Cửa sắt kính sau bếp CuaSatKinh (m[])		4,70	16,00	0,90×0,06×2,20	0,00 → 2,20	← trái
BA-53	Cửa sổ bếp (cánh phải) CuaSo_Bep_Phai		0,65	16,45	0,50×0,05×1,00	1,10 → 2,10	ra đường
BA-54	Song sắt hoa cửa sổ bếp SongSatHoa_Bep		0,90	16,36	0,95×0,01×0,95	1,12 → 2,07	ra đường
BA-55	Bậu cửa sổ granite — bếp BauCuaSo_Granito_Bep		0,90	16,39	1,00×0,08×0,03	1,07 → 1,10	ra đường
BA-56	Cửa sổ bếp (cánh trái) CuaSo_Bep_Trai		1,15	16,45	0,50×0,05×1,00	1,10 → 2,10	trong

Tầng 1 (±0,00) · 30 vật trong GT, KS



Mã	Tên (tên trong Unity)	Đêm	Tâm X	Tâm Z	Rộng×Sâu×Cao (m)	Y đáy → đỉnh	Hướng
ĐỒ ĐẶT TRÊN SÀN							
GT-01	Thùng nước có nắp ThungNuoc_Nap		0,65	17,45	0,61×0,61×0,82	−0,05 → 0,77	trong
GT-02	Chậu trâu bà ChauTrauBa		6,90	17,40	0,24×0,24×0,26	−0,05 → 0,21	trong
GT-03	Giàn phơi gấp GianPhoi_Gap		3,60	17,90	0,65×0,04×0,85	−0,05 → 0,80	trong
KS-01	Bộ xô - gáo - chậu WC BoXoGauChau_WC		6,95	19,60	1,10×0,42×0,42	0,00 → 0,42	trong
KS-02	Dép tổ ong DepToong_Fix		4,95	20,55	0,33×0,30×0,05	0,00 → 0,05	15°
KS-03	Thảm chùi chân ThamChuiChan		4,20	20,90	0,40×0,60×0,02	0,00 → 0,02	→ phải
KS-04	Xỉ bet XiBet_Tron		7,29	21,20	0,38×0,62×0,81	0,00 → 0,81	← trái
KS-05	Xô gáo úp XoGao_Up		5,35	21,45	0,29×0,23×0,32	0,00 → 0,32	20°
KS-06	Cọ bốn cầu ChoiCauBonCau		7,40	21,60	0,13×0,13×0,48	0,00 → 0,48	trong
KS-07	Ghế đầu gỗ GheDau_Go		6,60	22,70	0,32×0,32×0,44	0,00 → 0,44	-20°
KS-08	Chống thùng carton ThungCarton_Chong		3,00	23,30	1,09×0,54×0,97	0,00 → 0,97	25°
KS-09	Chậu nhựa úp ChauNhua_Up		5,30	23,30	0,42×0,20×0,41	0,00 → 0,41	trong
KS-10	Ghế đầu nhựa GheDau_Nhua		6,10	23,30	0,30×0,30×0,30	0,00 → 0,30	trong
KS-11	Chống thùng carton ThungCarton_Chong		1,20	23,90	1,09×0,54×0,97	0,00 → 0,97	10°
KS-12	Tầu nhựa quần áo Thau_Nhua_QuanAo		5,85	23,90	0,70×0,70×0,32	0,00 → 0,32	15°
KS-13	Bể giặt xi măng BeGiat		7,09	23,87	1,00×0,70×1,11	0,00 → 1,11	ra đường
KS-14	Chống thùng carton ThungCarton_Chong		2,49	24,05	1,09×0,54×0,97	0,00 → 0,97	-8°
KS-15	Thùng nước có nắp ThungNuoc_Nap		4,20	24,20	0,61×0,61×0,82	0,00 → 0,82	trong
KS-16	Bàn chải cọ + xà phòng BanChaiCo_XaPhong		6,80	24,27	0,23×0,04×0,04	0,00 → 0,04	170°
KS-17	Bao bột giặt, xà phòng BaoBotGiat_XaPhong		7,20	24,30	0,38×0,13×0,25	0,00 → 0,25	trong
ĐỒ ĐẶT TRÊN BÀN / KỆ / GIƯỜNG							
KS-18	Móc áo + khăn tắm MocAo_KhanTam		6,02	19,25	0,58×0,10×0,41	1,23 → 1,64	trong
KS-19	Kệ xà phòng WC KeXaPhong_WC		6,40	21,73	0,50×0,14×0,18	1,19 → 1,37	ra đường
KS-20	Cuộn giấy vệ sinh treo GiayVeSinh_Treo		7,25	21,72	0,12×0,16×0,16	0,60 → 0,76	ra đường
KS-21	Khăn + móc nhựa (WC) Khan_Ru		5,05	21,80	1,00×1,00×1,00	1,10 → 2,10	ra đường
TREO TƯỜNG / TREO TRẦN							
KS-22	Vòi sen VoiSen		5,61	21,80	0,15×0,08×0,64	1,08 → 1,73	ra đường
DIỆN - ĐÈN - QUẠT							
KS-23	Đèn tuýp máng 0,6 m DenTuyyp_60		6,10	20,50	0,62×0,07×0,06	3,14 → 3,20	→ phải
CỬA, CỔNG, CỬA SỔ, RÈM							
KS-24	Khung cửa WC tầng 1 KhungCuaWC_T1		4,65	20,55	0,80×0,06×1,95	0,00 → 1,95	← trái
KS-25	Cửa WC tầng 1 CuaWC_T1 (m[])		5,00	20,90	0,70×0,10×1,90	0,00 → 1,90	ra đường
KẾT CẤU PHỤ / CỐ ĐỊNH							
GT-04	Máy bơm nước (giếng trời) MayBom_NuocGiengTroai		2,40	16,85	0,40×0,32×3,40	−0,05 → 3,35	trong
GT-05	Ổng nước mưa (giếng trời) ongNuocMua_GiengTroai		7,43	18,50	0,15×0,38×9,65	−0,05 → 9,60	← trái

Hầm (−2,30) · 8 vật trong H

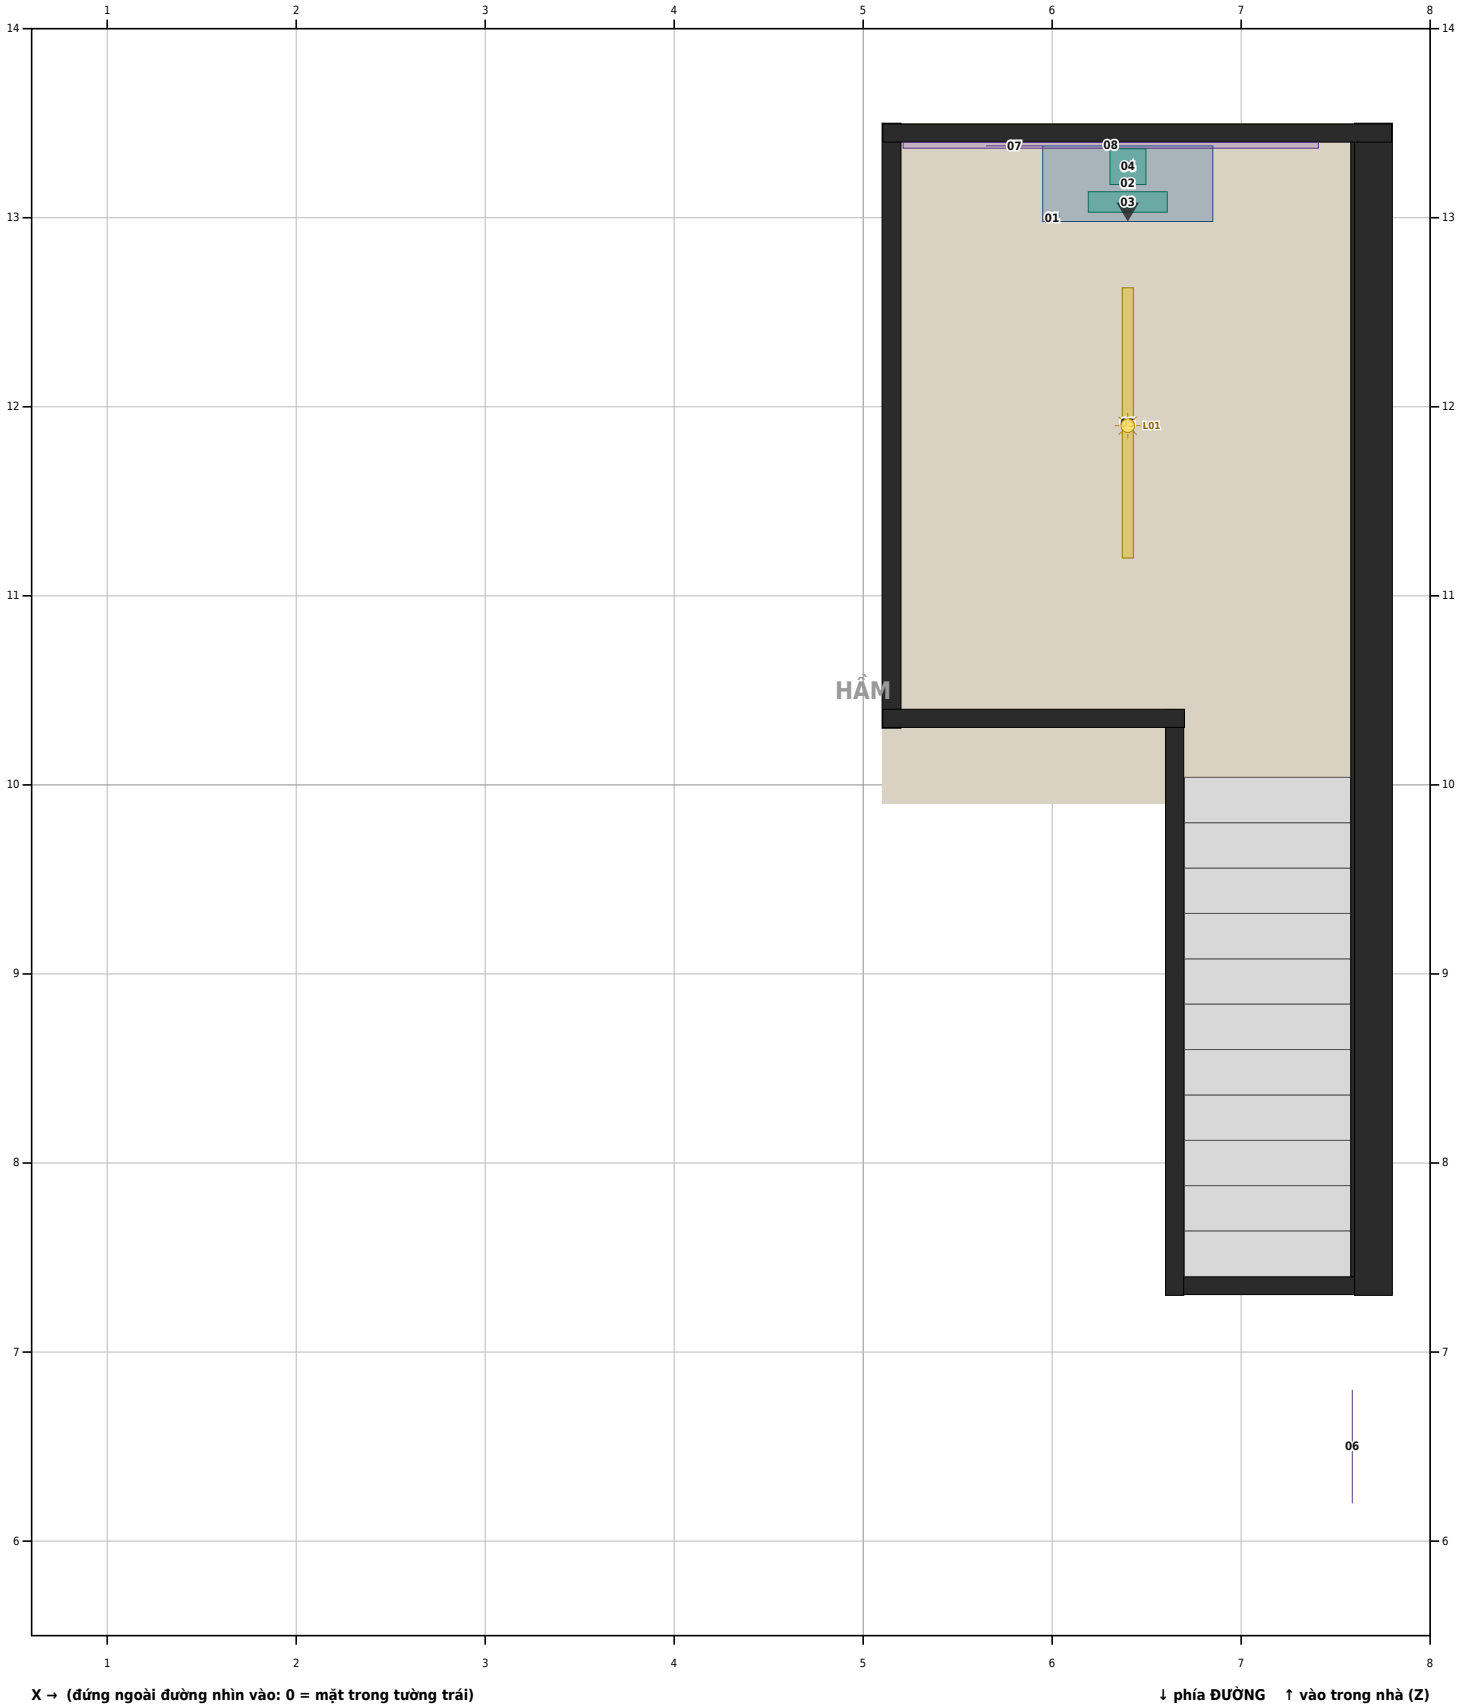

CHÚ GIẢI

- Đồ đặt trên sàn

Điện - đèn - quạt

Tường (cắt ở 1,5 m)

Cổng tắc / ổ cắm (CT..)

Đ1: chỉ có ở Đèn 1
- Đồ đặt trên bàn / kệ / giường

Cửa, cổng, cửa sổ, rèm

Bậu / tường thấp

Nguồn sáng (L..)

Đ2: chỉ có ở Đèn 2
- Treo tường / treo trần

Kết cấu phụ / cố định

Kính

▲ mặt trước của vật

Đ3: chỉ có ở Đèn 3

Mã	Tên (tên trong Unity)	Đêm	Tâm X	Tâm Z	Rộng×Sâu×Cao (m)	Y đáy → đỉnh	Hướng
ĐỒ ĐẶT TRÊN SÀN							
H-01	Giấy kê chân (hầm) GiayKeChan		6,00	13,00	0,07×0,05×0,01	−2,30 → −2,29	trong
H-02	Bàn thờ hầm BanThoHam		6,40	13,18	0,90×0,40×0,68	−2,30 → −1,62	ra đường
ĐỒ ĐẶT TRÊN BÀN / KỆ / GIƯỜNG							
H-03	Năm chén nước trên đế (bàn thờ hắ... Bo_Chen_Tren_De		6,40	13,08	0,11×0,42×0,08	−1,62 → −1,54	→ phải
H-04	Bát nhang (đủ bộ) BatNhang_FullAssembly		6,40	13,27	0,19×0,19×0,19	−1,61 → −1,43	ra đường
ĐIỆN - ĐÈN - QUẠT							
H-05	Đèn hầm — bóng dây tóc (đủ bộ) DenHam_FullAssembly		6,40	11,91	0,06×1,43×0,64	−0,84 → −0,20	trong
KẾT CẤU PHỤ / CỐ ĐỊNH							
H-06	Chữ sơn đỏ "BẬT ĐIỆN" Decal_ChuaBatDien		7,59	6,50	0,60×0,00×0,16	1,37 → 1,53	← trái
H-07	Decal bong vôi Decal_BongVoi_A		5,80	13,38	0,30×0,00×0,40	−0,60 → −0,20	ra đường
H-08	Tường dán kín bùa (hầm) TuongBuaMau		6,31	13,38	2,20×0,03×1,42	−1,73 → −0,30	ra đường

Tầng 2 (+3,40) · 70 vật trong BM



Mã	Tên (tên trong Unity)	Đềm	Tầm X	Tầm Z	Rộng×Sâu×Cao (m)	Y đáy → đỉnh	Hướng
ĐỒ ĐẶT TRÊN SÀN							
BM-01	Bàn gỗ (đồ học cũ) BanCohoc_Go		1,30	0,27	1,00×0,50×0,75	3,40 → 4,15	trong
BM-02	Tủ đầu giường TuDauGiuong		7,37	0,54	0,42×0,45×0,50	3,40 → 3,90	← trái
BM-03	Ghế tựa + áo sơ mi của bố GheTua_AoBo_Fix		2,17	0,60	0,44×0,49×0,91	3,40 → 4,31	ra đường
BM-04	Giường đôi (bộ) GiuongDoi_Bo		6,46	1,70	1,87×2,27×1,80	3,40 → 5,20	→ phải
BM-05	Thảm đỏ 1,2 m Tham_Do_1m2		3,50	2,40	0,92×1,37×0,01	3,40 → 3,41	→ phải
BM-06	Bộ bàn trang điểm (+ gương) BanTrangDiem_Bo		0,21	2,45	0,90×0,42×1,61	3,40 → 5,01	→ phải
BM-07	Đôn ngồi trang điểm DonTrangDiem		0,75	2,45	0,32×0,32×0,35	3,40 → 3,75	trong
BM-08	Tủ đầu giường TuDauGiuong		7,37	2,86	0,42×0,45×0,50	3,40 → 3,90	← trái
BM-09	Kệ sách hồ sơ gỗ KeSachHoSo_Go		0,17	3,95	0,85×0,32×1,52	3,40 → 4,92	→ phải
BM-10	Mắc áo đứng MacAoDung		0,25	4,95	0,34×0,34×1,62	3,41 → 5,03	trong
BM-11	Giỏ quần áo GioQuanAo		3,85	5,00	0,63×0,55×0,42	3,40 → 3,82	10°
BM-12	Tủ quần áo găm hờ (kết sắt dưới gá... TuQuanAo_GamHo		1,20	5,12	1,26×0,60×1,94	3,40 → 5,34	ra đường
BM-13	Rổ nhựa quần áo bẩn RoNhua_QuanAoBan		4,95	5,10	0,54×0,53×0,54	3,40 → 3,94	trong
BM-14	Xí bệt XiBet_Tron		7,15	5,09	0,38×0,62×0,81	3,40 → 4,21	ra đường
BM-15	Kết sắt khoá số KetSat_KhoaSo		1,18	5,15	0,40×0,38×0,24	3,40 → 3,64	ra đường
BM-16	Cọ bốn cầu ChoiCauBonCau		6,78	5,28	0,13×0,13×0,48	3,40 → 3,88	trong
ĐỒ ĐẶT TRÊN BÀN / KỆ / GIƯỜNG							
BM-17	Nhật ký (đóng) NhatKy_Dong		1,30	0,30	0,16×0,22×0,02	4,15 → 4,17	trong
BM-18	Lọ thuốc nam của bố ThuocBo_LoThuocNam		7,38	0,50	0,30×0,11×0,14	3,90 → 4,04	← trái
BM-19	Đồng hồ báo thức để bàn DongHoDeBan_BaoThuc		7,51	0,50	0,11×0,05×0,13	3,90 → 4,03	trong
BM-20	Đồ trên tủ đầu giường (bố) DoTuDauGiuong_Bo		6,50	0,95	0,24×0,30×0,06	3,87 → 3,93	trong
BM-21	Chăn mền bông gấp gọn ChanMenBong_GapGon		5,75	1,70	0,92×0,63×0,35	4,01 → 4,36	→ phải
BM-22	Túi xách của mẹ (vi) TuiXachMe_ViTien		0,75	2,45	0,49×0,13×0,35	3,75 → 4,10	20°
BM-23	Hộp kim chỉ của mẹ HopKimChi_Me		0,20	2,60	0,20×0,20×0,10	4,13 → 4,23	trong
BM-24	Đồ trên tủ đầu giường (mẹ) DoTuDauGiuong_Me		7,37	2,69	0,22×0,25×0,04	3,90 → 3,94	← trái
BM-25	Điện thoại di động đồ chuông Nokia_DoChuong		7,31	2,85	0,16×0,13×0,02	4,17 → 4,20	-160°
BM-26	Móc áo + khăn tắm MocAo_KhanTam		6,42	3,65	0,58×0,10×0,41	4,63 → 5,04	trong
BM-27	Cốc bàn chải (người lớn) CocBanChai_NguoiLon		7,51	4,05	0,07×0,06×0,22	4,29 → 4,51	trong
BM-28	Kệ kính đồ dùng (WC bố mẹ) KeKinh_DoBoMe		7,55	4,10	0,42×0,04×0,11	4,29 → 4,40	← trái
BM-29	Vải che gương — WC VaiChePhuGuong_WC		7,58	4,10	0,47×0,05×0,47	4,32 → 4,79	← trái
BM-30	Cuộn giấy vệ sinh treo GiayVeSinh_Treo		7,52	5,05	0,12×0,17×0,16	4,00 → 4,16	← trái
BM-31	Kệ xà phòng WC KeXaPhong_WC		6,40	5,33	0,50×0,14×0,18	4,69 → 4,87	ra đường
TREO TƯỜNG / TREO TRẦN							
BM-32	Tranh chữ "Phúc" (quốc ngữ) TranhThuPhap_Phuc		0,02	1,55	0,42×0,05×0,62	4,95 → 5,57	→ phải
BM-33	Ảnh cưới bố mẹ (khung treo) AnhCuoi_Tex		7,59	1,70	0,50×0,02×0,70	5,05 → 5,75	← trái
BM-34	Lavabo Lavabo		7,42	4,10	0,45×0,35×0,15	4,07 → 4,22	← trái

Vật thứ 35 → 70 / 70

Mã	Tên (tên trong Unity)	Đêm	Tâm X	Tâm Z	Rộng×Sâu×Cao (m)	Y đáy → đỉnh	Hướng
BM-35	Kệ kính KeKinh		7,55	4,10	0,30×0,10×0,02	4,27 → 4,29	← trái
BM-36	Gương WC GuongWC		7,59	4,10	0,40×0,02×0,40	4,35 → 4,75	← trái
BM-37	Bình nóng lạnh BinhNongLanh		7,42	4,75	0,77×0,35×0,35	5,35 → 5,70	← trái
BM-38	Áo mưa của bố treo cửa AoMuaBo_TreoCua		3,95	5,34	0,56×0,12×0,91	4,24 → 5,15	ra đường
ĐIỆN - ĐÈN - QUẠT							
BM-39	Đèn ốp trần DenOpTran		3,40	2,70	0,30×0,30×0,11	6,29 → 6,40	trong
BM-40	Đèn ngủ đầu giường bố mẹ DenNgu_BoMe		7,38	2,92	0,20×0,20×0,32	3,90 → 4,22	trong
BM-41	Quạt cây đứng QuatCayDung		0,55	3,15	0,49×0,48×1,32	3,41 → 4,73	109°
BM-42	Ổ cắm đôi OCam_Doi		7,59	3,20	0,01×0,07×0,07	3,90 → 3,97	← trái
BM-43	Quạt treo tường QuatTreoTuong_Fix		0,15	3,80	0,46×0,30×0,57	5,41 → 5,98	→ phải
BM-44	Đèn tuýp máng 0,6 m DenTuyp_60		6,70	4,50	0,62×0,07×0,06	6,34 → 6,40	→ phải
CỬA, CỔNG, CỬA SỔ, RÈM							
BM-45	Cửa sổ phòng bố mẹ (trái) CuaSo_BoMe_Trai		1,02	−0,05	0,55×0,05×1,40	4,30 → 5,70	ra đường
BM-46	Cửa sổ phòng bố mẹ (phải) CuaSo_BoMe_Phai		1,57	−0,05	0,55×0,05×1,40	4,30 → 5,70	trong
BM-47	Cửa sổ phòng bố mẹ (trái) CuaSo_BoMe_Trai		5,83	−0,05	0,55×0,05×1,40	4,30 → 5,70	ra đường
BM-48	Cửa sổ phòng bố mẹ (phải) CuaSo_BoMe_Phai		6,38	−0,05	0,55×0,05×1,40	4,30 → 5,70	trong
BM-49	Bậu cửa sổ granito — bố mẹ BauCuaSo_Granito_BoMe		1,30	0,01	1,10×0,08×0,03	4,27 → 4,30	trong
BM-50	Song sắt hoa cửa sổ bố mẹ SongSatHoa_BoMe		1,30	0,04	1,05×0,01×1,35	4,33 → 5,67	trong
BM-51	Bậu cửa sổ granito — bố mẹ BauCuaSo_Granito_BoMe		6,10	0,01	1,10×0,08×0,03	4,27 → 4,30	trong
BM-52	Song sắt hoa cửa sổ bố mẹ SongSatHoa_BoMe		6,11	0,04	1,05×0,01×1,35	4,33 → 5,67	trong
BM-53	Rèm voan — phòng bố mẹ Rem_Voan_BoMe		1,30	0,07	1,20×0,04×1,65	4,20 → 5,85	trong
BM-54	Thanh treo rèm ThanhRem		1,30	0,07	1,33×0,03×0,03	5,85 → 5,88	trong
BM-55	Thanh treo rèm ThanhRem		6,10	0,07	1,33×0,03×0,03	5,85 → 5,88	trong
BM-56	Rèm voan — phòng bố mẹ Rem_Voan_BoMe		6,10	0,07	1,20×0,04×1,65	4,20 → 5,85	trong
BM-57	Thanh treo rèm ThanhRem		1,30	0,16	1,33×0,03×0,03	5,85 → 5,88	trong
BM-58	Rèm vải — phòng bố mẹ Rem_Vai_BoMe_Buong		1,30	0,16	1,20×0,06×1,65	4,20 → 5,85	trong
BM-59	Thanh treo rèm ThanhRem		6,10	0,16	1,33×0,03×0,03	5,85 → 5,88	trong
BM-60	Rèm vải — phòng bố mẹ Rem_Vai_BoMe_Buong		6,10	0,16	1,20×0,06×1,65	4,20 → 5,85	trong
BM-61	Khung ảnh cưới nhỏ KhungAnh_CuoINho		0,90	0,27	0,24×0,19×0,18	4,15 → 4,33	10°
BM-62	Kính lão + hộp kính KinhLao_HopKinh		1,75	0,30	0,36×0,16×0,04	4,15 → 4,19	20°
BM-63	Cánh cửa ban công (trái) CanhBanCong_Trai		3,20	0,33	0,60×0,05×2,20	3,40 → 5,60	→ phải
BM-64	Cánh cửa ban công (phải) CanhBanCong_Phai		4,40	0,33	0,60×0,05×2,20	3,40 → 5,60	→ phải
BM-65	Khung cửa WC bố mẹ KhungCuaWC_BoMe		5,75	4,25	0,80×0,06×1,95	3,40 → 5,35	← trái
BM-66	Cửa WC phòng bố mẹ CuaWC_BoMe (m[])		6,10	4,60	0,70×0,10×1,90	3,40 → 5,30	ra đường


Mã	Tên (tên trong Unity)	Đêm	Tâm X	Tâm Z	Rộng×Sâu×Cao (m)	Y đáy → đỉnh	Hướng
KẾT CẤU PHỤ / CỐ ĐỊNH							
BM-67	Lan can sắt ban công LanCan_BanCong		1,70	−1,18	3,80×0,04×1,02	3,48 → 4,50	trong
BM-68	Gờ bê tông ban công GoBanCong		1,75	−1,18	3,90×0,14×0,10	3,38 → 3,48	trong
BM-69	Lan can sắt ban công LanCan_BanCong		5,50	−1,18	3,80×0,04×1,02	3,48 → 4,50	trong
BM-70	Gờ bê tông ban công GoBanCong		5,55	−1,18	3,90×0,14×0,10	3,38 → 3,48	trong

Tầng 2 (+3,40) · 32 vật trong S2




Mã	Tên (tên trong Unity)	Đệm	Tâm X	Tâm Z	Rộng×Sâu×Cao (m)	Y đáy → đỉnh	Hướng
ĐỒ ĐẶT TRÊN SÀN							
S2-01	Tủ thấp sảnh TuThap_Sanh		0,19	6,22	0,80×0,36×0,65	3,40 → 4,04	→ phải
S2-02	Chậu lưới hồ ChauLuoaiHo		0,22	6,85	0,24×0,24×0,48	3,40 → 3,88	trong
S2-03	Chậu cây kiếng lá to ChauCayKieng-LaTo		2,73	11,60	0,74×0,78×1,17	3,40 → 4,57	trong
S2-04	Thảm / chiếu hoa Tham_Chieu_Hoa		1,55	12,30	0,92×1,37×0,01	3,40 → 3,41	trong
S2-05	Tủ đứng (rương chân màn) TuDung_RuongChanMan		0,33	13,25	2,32×0,65×1,80	3,40 → 5,20	→ phải
S2-06	Kệ giày dép gỗ KeGiayDep_Go		0,20	14,81	0,81×0,30×0,65	3,40 → 4,05	→ phải
S2-07	Chống thùng carton ThungCarton_Chong		0,35	15,82	1,09×0,54×0,97	3,40 → 4,37	80°
S2-08	Kệ sách hồ sơ gỗ KeSachHoSo_Go		1,50	16,20	0,85×0,32×1,52	3,40 → 4,92	ra đường
ĐỒ ĐẶT TRÊN BÀN / KỆ / GIƯỜNG							
S2-09	Vải che gương — sảnh VaiChePhuGuong_Sanh		0,02	6,22	0,52×0,05×0,64	4,56 → 5,20	→ phải
S2-10	Móc áo + khăn tắm MocAo_KhanTam		3,05	15,42	0,59×0,10×0,41	4,63 → 5,04	← trái
TREO TƯỜNG / TREO TRẦN							
S2-11	Gương treo sảnh GuongTreo_Sanh		0,01	6,22	0,45×0,00×0,55	4,60 → 5,15	→ phải
S2-12	Tranh nhỏ hành lang TranhNho_HanhLang		3,10	11,20	0,22×0,00×0,17	4,93 → 5,10	← trái
S2-13	Tranh sơn thủy (khung) TranhSonThuy_Khung		0,02	11,50	0,66×0,05×0,46	4,95 → 5,41	→ phải
ĐIỆN - ĐÈN - QUẠT							
S2-14	Chuông điện (chuông) ChuongDien_Chuong		3,02	7,70	0,16×0,15×0,16	5,52 → 5,68	← trái
S2-15	Bóng đèn compact BongCompact		2,50	13,00	0,04×0,03×0,13	6,27 → 6,40	trong
KẾT CẤU PHỤ / CỐ ĐỊNH							
S2-16	Mũi bậc bo tròn (mòn) MuiBac_Mon		1,45	7,59	0,90×0,02×0,02	3,56 → 3,58	trong
S2-17	Trụ đầu thang gỗ tiện TruDauThang		1,87	7,60	0,14×0,14×0,95	3,40 → 4,35	trong
S2-18	Mũi bậc bo tròn (mòn) MuiBac_Mon		1,45	7,84	0,90×0,02×0,02	3,73 → 3,76	trong
S2-19	Mũi bậc bo tròn (mòn) MuiBac_Mon		0,45	7,86	0,90×0,02×0,02	6,40 → 6,42	ra đường
S2-20	Mũi bậc bo tròn (mòn) MuiBac_Mon		0,45	8,11	0,90×0,02×0,02	6,22 → 6,25	ra đường
S2-21	Mũi bậc bo tròn (mòn) MuiBac_Mon		1,45	8,09	0,90×0,02×0,02	3,91 → 3,93	trong
S2-22	Mũi bậc bo tròn (mòn) MuiBac_Mon		1,45	8,34	0,90×0,02×0,02	4,09 → 4,11	trong
S2-23	Mũi bậc bo tròn (mòn) MuiBac_Mon		0,45	8,36	0,90×0,02×0,02	6,04 → 6,07	ra đường
S2-24	Mũi bậc bo tròn (mòn) MuiBac_Mon		0,45	8,61	0,90×0,02×0,02	5,87 → 5,89	ra đường
S2-25	Mũi bậc bo tròn (mòn) MuiBac_Mon		1,45	8,59	0,90×0,02×0,02	4,27 → 4,29	trong
S2-26	Mũi bậc bo tròn (mòn) MuiBac_Mon		1,45	8,84	0,90×0,02×0,02	4,45 → 4,47	trong
S2-27	Mũi bậc bo tròn (mòn) MuiBac_Mon		0,45	8,86	0,90×0,02×0,02	5,69 → 5,71	ra đường
S2-28	Mũi bậc bo tròn (mòn) MuiBac_Mon		0,45	9,11	0,90×0,02×0,02	5,51 → 5,53	ra đường
S2-29	Mũi bậc bo tròn (mòn) MuiBac_Mon		1,45	9,09	0,90×0,02×0,02	4,62 → 4,65	trong
S2-30	Mũi bậc bo tròn (mòn) MuiBac_Mon		1,45	9,34	0,90×0,02×0,02	4,80 → 4,82	trong
S2-31	Mũi bậc bo tròn (mòn) MuiBac_Mon		0,45	9,36	0,90×0,02×0,02	5,33 → 5,36	ra đường
S2-32	Mũi bậc bo tròn (mòn) MuiBac_Mon		0,45	9,61	0,90×0,02×0,02	5,16 → 5,18	ra đường

Tầng 2 (+3,40) · 9 vật trong LV

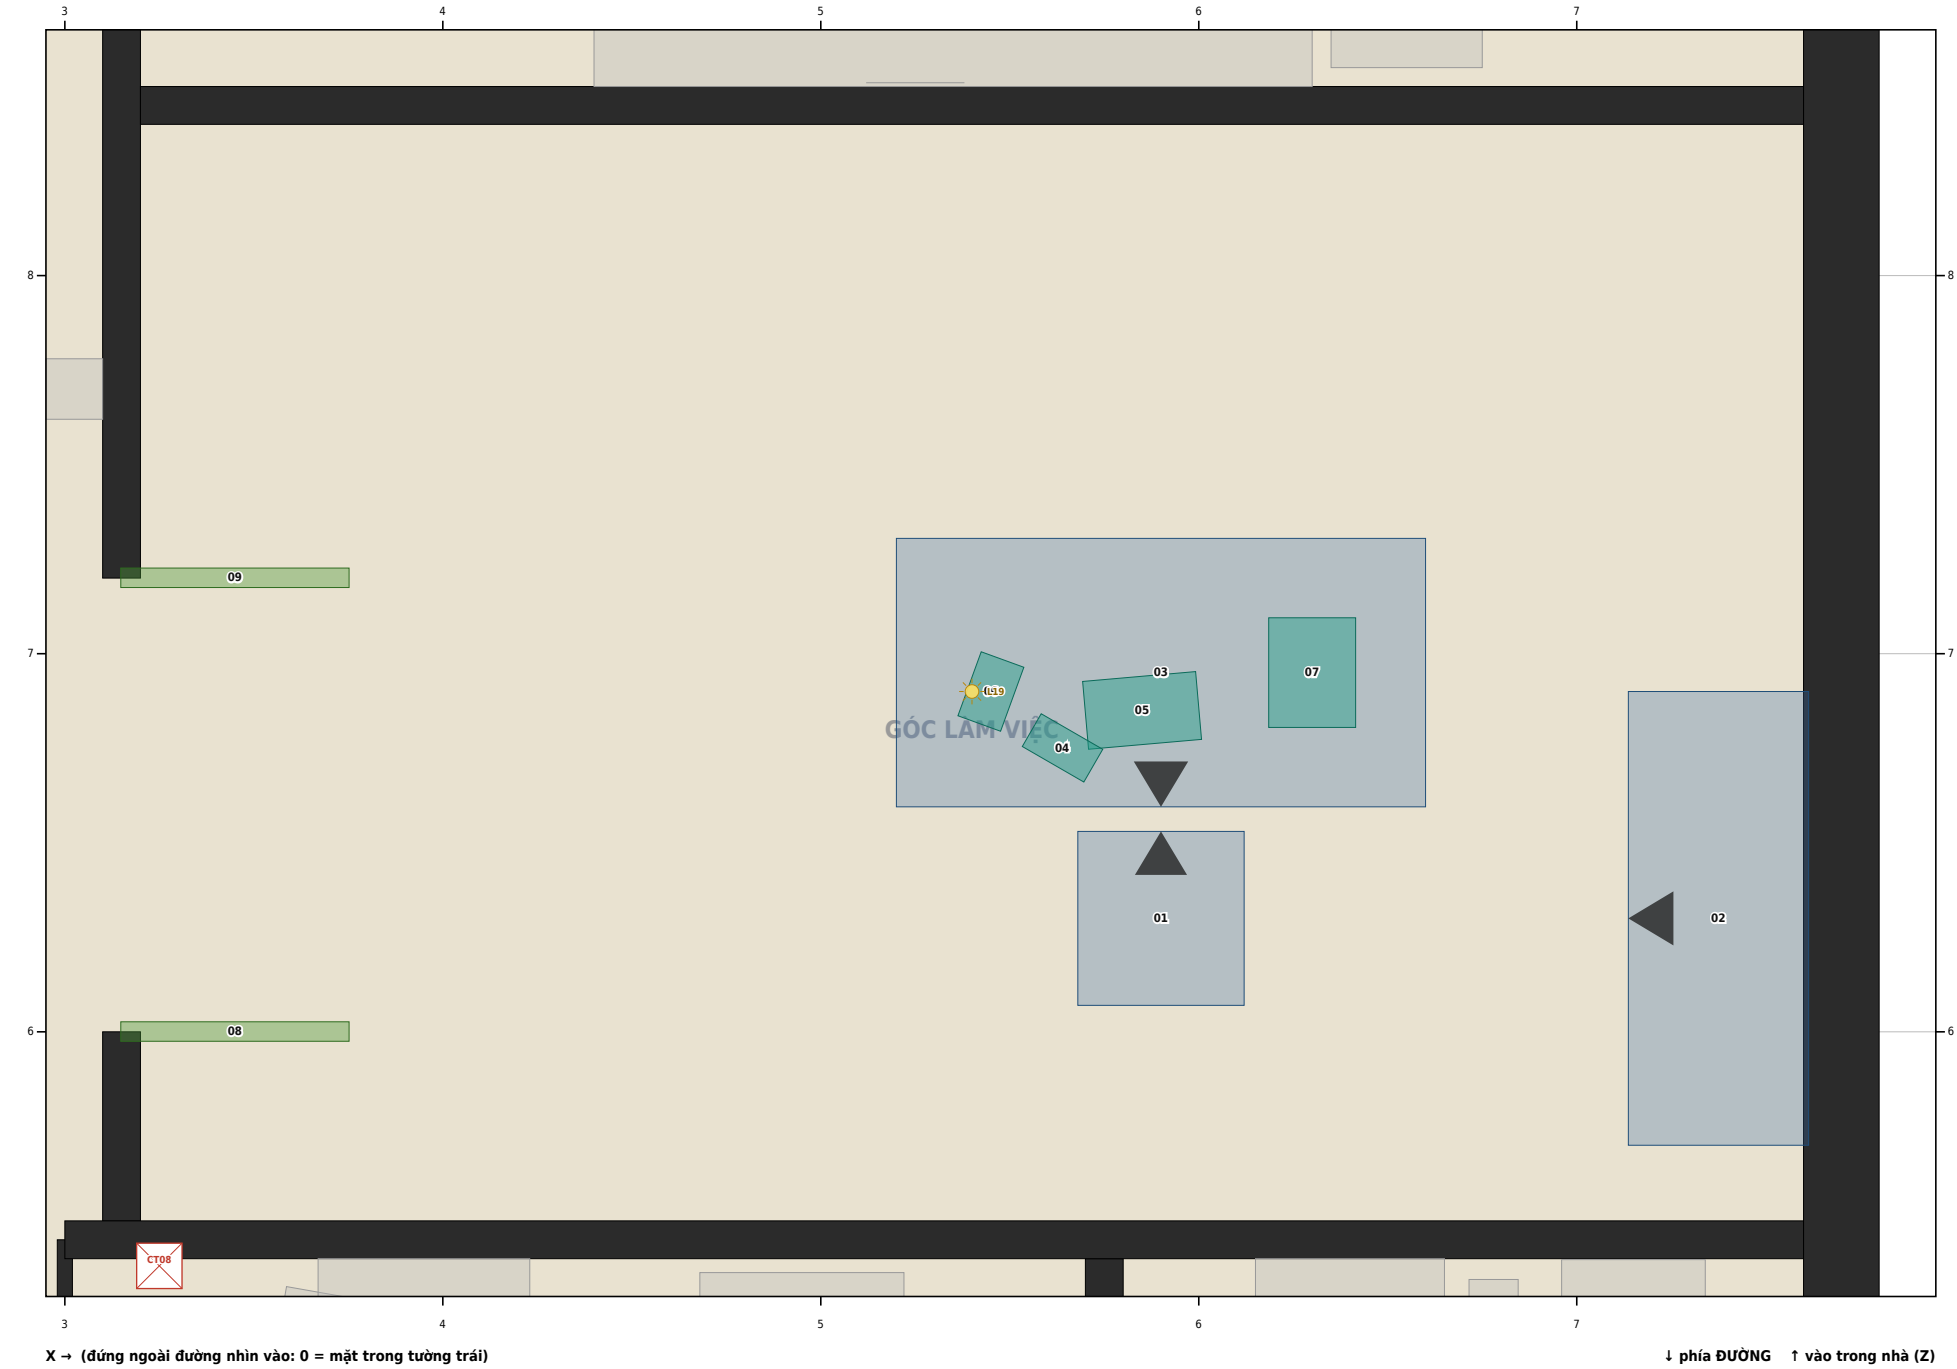

Mã	Tên (tên trong Unity)	Đêm	Tâm X	Tâm Z	Rộng×Sâu×Cao (m)	Y đáy → đỉnh	Hướng
ĐỒ ĐẶT TRÊN SÀN							
LV-01	Ghế bàn giấy GheBanGiay		5,90	6,30	0,44×0,46×0,85	3,40 → 4,25	trong
LV-02	Tủ hồ sơ sắt TuHoSo_Sat		7,38	6,30	1,20×0,48×1,70	3,40 → 5,10	← trái
LV-03	Bàn giấy gỗ BanGiay_Go		5,90	6,95	1,40×0,71×0,75	3,40 → 4,15	ra đường
ĐỒ ĐẶT TRÊN BÀN / KỆ / GIƯỜNG							
LV-04	Con dấu + hộp mực ConDau_HopMuc		5,64	6,75	0,19×0,10×0,09	4,15 → 4,24	30°
LV-05	Bàn tính gỗ BanTinh_Go		5,85	6,85	0,30×0,18×0,06	4,15 → 4,21	175°
LV-06	Máy tính bỏ túi MayTinhBoTui		5,45	6,90	0,12×0,18×0,02	4,15 → 4,17	20°
LV-07	Chống sổ sách cũ ChongSoSach_Cu		6,30	6,95	0,23×0,29×0,28	4,15 → 4,43	trong
CỬA, CỔNG, CỬA SỔ, RÈM							
LV-08	Cửa góc làm việc — cánh trái CuaLamViec_Trai (m[])		3,45	6,00	0,60×0,05×2,20	3,40 → 5,60	ra đường
LV-09	Cửa góc làm việc — cánh phải CuaLamViec_Phai (m[])		3,45	7,20	0,60×0,05×2,20	3,40 → 5,60	ra đường

Tầng 2 (+3,40) · 22 vật trong NH

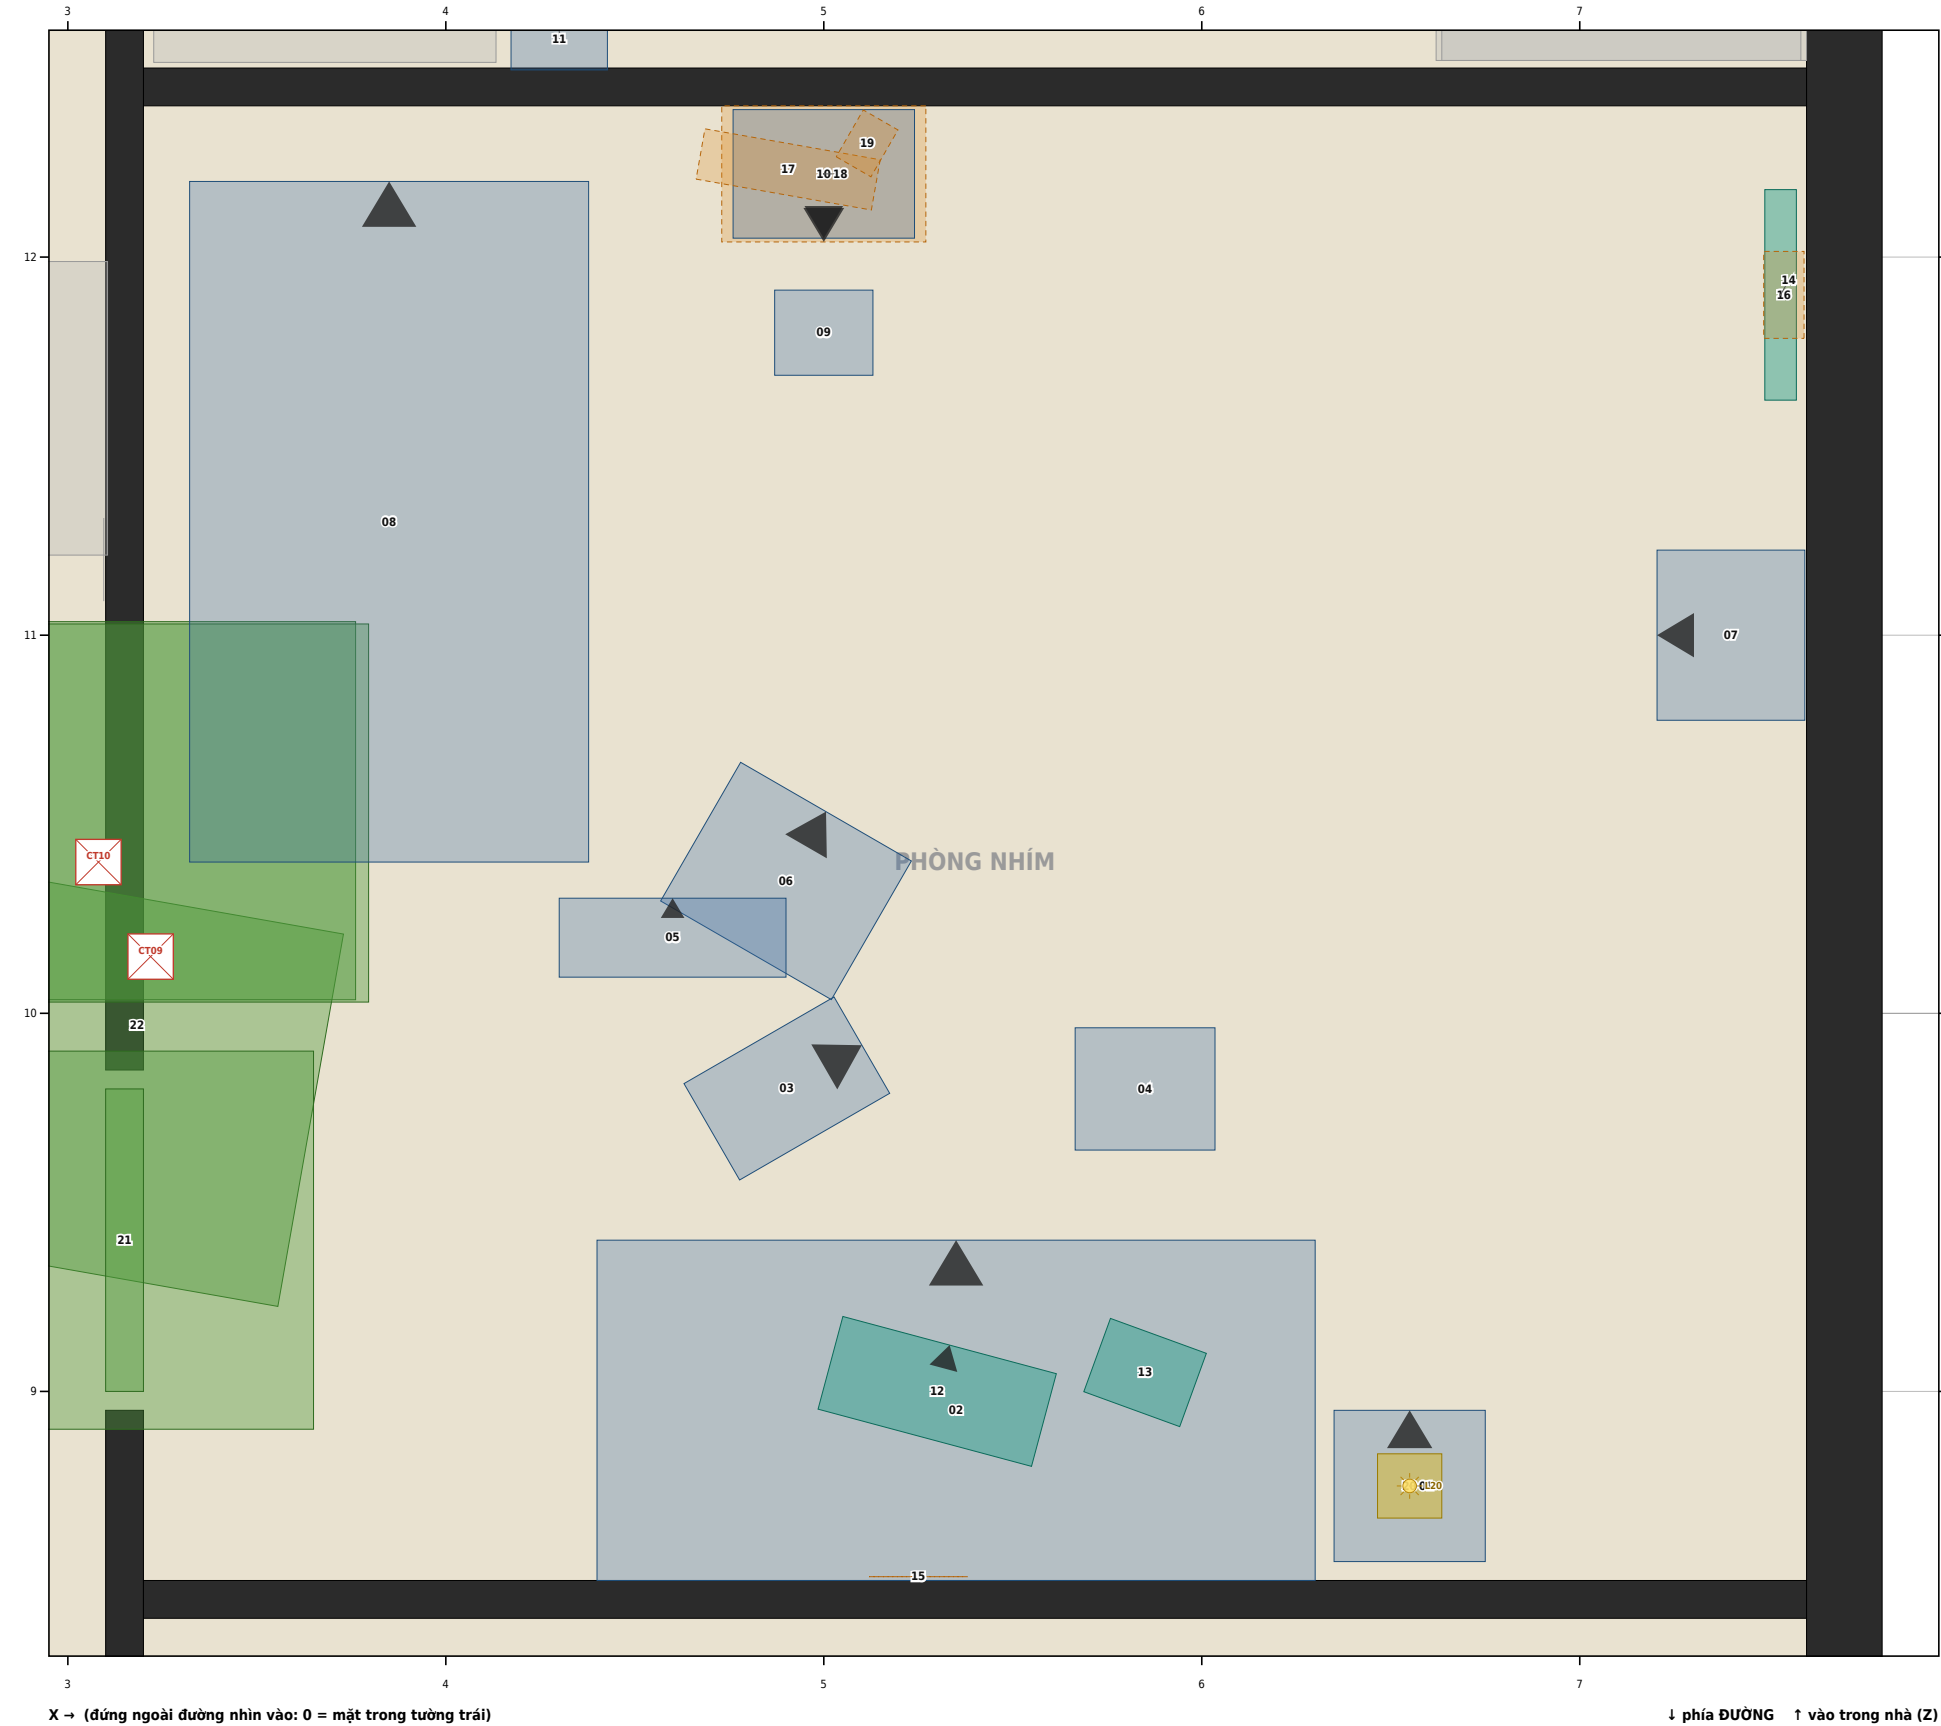

- CHÚ GIẢI**

 - Đồ đặt trên sàn
 - Điện - đèn - quạt
 - Tường (cắt ở 1,5 m)
 - Công tắc / ổ cắm (CT..)
 - Đ1: chỉ có ở Đêm 1
- Đồ đặt trên bàn / kệ / giường
 - Cửa, cổng, cửa sổ, rèm
 - Bậu / tường thấp
 - Nguồn sáng (L..)
 - Đ2: chỉ có ở Đêm 2
- Treo tường / treo trần
 - Kết cấu phụ / cố định
 - Kính
 - ▲ mặt trước của vật
 - Đ3: chỉ có ở Đêm 3


Mã	Tên (tên trong Unity)	Đêm	Tâm X	Tâm Z	Rộng×Sâu×Cao (m)	Y đáy → đỉnh	Hướng
ĐỒ ĐẶT TRÊN SÀN							
NH-01	Bàn cạnh giường (thuốc) BanCanhGiuong_Thuoc		6,55	8,75	0,40×0,40×0,72	3,40 → 4,12	trong
NH-02	Giường Nhím + chiếu + chăn GiuongNhim_ChieuChan		5,35	8,95	1,90×0,90×0,85	3,40 → 4,25	trong
NH-03	Búp bê nhựa cũ BupBe_NhuaCu		4,90	9,80	0,29×0,46×0,13	3,40 → 3,53	60°
NH-04	Chậu nước + khăn ướt (Nhím) ChauNuoc_KhanUot		5,85	9,80	0,37×0,32×0,09	3,40 → 3,49	trong
NH-05	Đồ chơi lớn (Nhím) DoChoi_Lon		4,60	10,20	0,60×0,21×0,12	3,40 → 3,52	trong
NH-06	Sách truyện tranh SachTruyenTranh		4,90	10,35	0,52×0,42×0,02	3,40 → 3,42	30°
NH-07	Tủ nhựa ghép cửa Nhím TuNhua_Nhim		7,40	11,00	0,45×0,39×1,18	3,40 → 4,58	← trái
NH-08	Giường xếp (khách) GiuongXep_CoTam		3,85	11,30	1,06×1,80×0,46	3,40 → 3,85	trong
NH-09	Ghế nhựa của Nhím GheNhua_Nhim		5,00	11,80	0,26×0,23×0,26	3,40 → 3,66	trong
NH-10	Bàn học của Nhím BanHoc_Nhim		5,00	12,22	0,48×0,34×0,45	3,40 → 3,85	ra đường
NH-11	Cặp sách tiểu học CapSach_TieuHoc		4,30	12,64	0,30×0,25×0,42	3,40 → 3,81	→ phải
ĐỒ ĐẶT TRÊN BÀN / KỆ / GIƯỜNG							
NH-12	Băng bột tay gây (Nhím) BangTayGay		5,30	9,00	0,58×0,25×0,08	3,73 → 3,81	15°
NH-13	Gấu bông cũ GauBong_Cu		5,85	9,05	0,27×0,21×0,33	3,67 → 4,00	-160°
NH-14	Đồng phục Nhím treo móc DongPhuc_Treo		7,53	11,90	0,56×0,08×0,78	4,04 → 4,82	← trái
TREO TƯỜNG / TREO TRẦN							
NH-15	Tranh sắp màu "cả nhà" của Nhím TranhSap_Nhim		5,25	8,51	0,26×0,00×0,20	4,50 → 4,70	trong
NH-16	Móc treo đồng phục MocDongPhuc		7,54	11,90	0,23×0,11×0,47	4,43 → 4,90	← trái
NH-17	Hộp bút + thuốc kẻ HopBut_ThuocKe		4,91	12,23	0,47×0,14×0,06	4,04 → 4,11	10°
NH-18	Đồ học trên bàn của Nhím DoHoc_Nhim		5,00	12,22	0,54×0,36×0,20	3,85 → 4,04	ra đường
NH-19	Bình nước học sinh BinhNuocHocSinh		5,12	12,30	0,11×0,14×0,23	4,04 → 4,28	30°
ĐIỆN - ĐÈN - QUẠT							
NH-20	Đèn ngủ của Nhím DenNgu_Nhim		6,55	8,75	0,17×0,17×0,24	3,95 → 4,19	trong
CỬA, CỔNG, CỬA SỔ, RÈM							
NH-21	Ô thoáng bông gió OThoang_BongGio		3,15	9,40	0,80×0,10×0,30	5,55 → 5,85	→ phải
NH-22	Cửa phòng Nhím (đủ bộ) CuaPhongNhim_FullAssembly		3,18	9,97	1,22×2,14×2,00	2,90 → 4,90	ra đường

Tầng 2 (+3,40) · 25 vật trong KH



Mã	Tên (tên trong Unity)	Đêm	Tâm X	Tâm Z	Rộng×Sâu×Cao (m)	Y đáy → đỉnh	Hướng
ĐỒ ĐẶT TRÊN SÀN							
KH-01	Tủ áo của Khôi TuAo_Khoi		3,68	12,88	0,91×0,73×1,80	3,40 → 5,20	trong
KH-02	Giường đơn của Khôi GiuongDon_Khoi		7,11	13,52	0,95×2,00×0,60	3,40 → 4,00	ra đường
KH-03	Ghế bàn học gỗ GheBanHoc_Go		5,70	15,50	0,42×0,42×0,87	3,40 → 4,27	trong
KH-04	Hành lý của Khôi (túi vải) HanhlLyKhoi_TuiVai		3,58	15,75	0,67×0,34×0,40	3,40 → 3,80	30°
KH-05	Bộ bàn học của Khôi BanHoc_Khoi_Bo		5,70	16,10	1,10×0,56×0,73	3,40 → 4,13	ra đường
KH-06	Đàn guitar cũ Guitar		7,45	16,22	0,32×0,05×0,88	3,40 → 4,28	← trái
KH-07	Ba lô của Khôi (xanh lá) BaLoKhoi_XanhLa	Đ2	6,43	12,80	0,30×0,28×0,55	3,40 → 3,95	20°
KH-08	Ba lô của Khôi (xanh lá) BaLoKhoi_XanhLa	Đ3	6,43	12,80	0,30×0,28×0,55	3,40 → 3,95	20°
ĐỒ ĐẶT TRÊN BÀN / KỆ / GIƯỜNG							
KH-09	Tấm nilon phủ bụi TamNilon_PhuBui		7,11	13,52	0,98×2,00×0,08	3,86 → 3,94	trong
KH-10	Giấy báo nhập học GiayBaoNhapHoc		5,18	16,01	0,49×0,33×0,00	4,13 → 4,13	15°
KH-11	Máy nghe băng + băng cũ Walkman_BangCu		6,10	16,00	0,45×0,17×0,06	4,13 → 4,19	-170°
KH-12	Đèn bàn học DenBanHoc		5,25	16,15	0,48×0,15×0,32	4,13 → 4,45	ra đường
TREO TƯỜNG / TREO TRẦN							
KH-13	Lịch tờ năm 2000 LichTo_2000		7,59	13,20	0,30×0,00×0,19	4,81 → 5,00	← trái
KH-14	Poster ban nhạc (bìa) Poster_BanNhac		7,59	14,00	0,34×0,00×0,24	4,81 → 5,05	← trái
KH-15	Giá sách (bộ) GiaSach_Bo		7,50	15,40	0,70×0,20×0,85	4,40 → 5,25	← trái
KH-16	Giấy khen của Khôi GiayKhen_Khoi		4,40	16,39	0,24×0,00×0,17	4,93 → 5,10	ra đường
ĐIỆN - ĐÈN - QUẠT							
KH-17	Quả bóng đá xẹp BongDa_Xep		7,10	14,00	0,19×0,19×0,12	3,40 → 3,52	trong
CỬA, CỔNG, CỬA SỔ, RÈM							
KH-18	Rèm vải — phòng Khôi Rem_Vai_Khoi_Buong		5,70	16,24	1,30×0,06×1,65	4,20 → 5,85	ra đường
KH-19	Thanh treo rèm ThanhRem		5,70	16,24	1,33×0,03×0,03	5,85 → 5,88	ra đường
KH-20	Rèm voan — phòng Khôi Rem_Voan_Khoi		5,70	16,33	1,30×0,04×1,65	4,20 → 5,85	ra đường
KH-21	Thanh treo rèm ThanhRem		5,70	16,33	1,33×0,03×0,03	5,85 → 5,88	ra đường
KH-22	Cửa sổ phòng Khôi (phải) CuaSo_Khoi_Phai		5,40	16,45	0,60×0,05×1,40	4,30 → 5,70	ra đường
KH-23	Song sắt hoa cửa sổ Khôi SongSatHoa_Khoi		5,70	16,36	1,15×0,01×1,35	4,33 → 5,67	ra đường
KH-24	Bậu cửa sổ granito — Khôi BauCuaSo_Granito_Khoi		5,70	16,39	1,20×0,08×0,03	4,27 → 4,30	ra đường
KH-25	Cửa sổ phòng Khôi (trái) CuaSo_Khoi_Trai		6,00	16,45	0,60×0,05×1,40	4,30 → 5,70	trong

Tầng 3 (+6,60) · 57 vật trong SP, PT

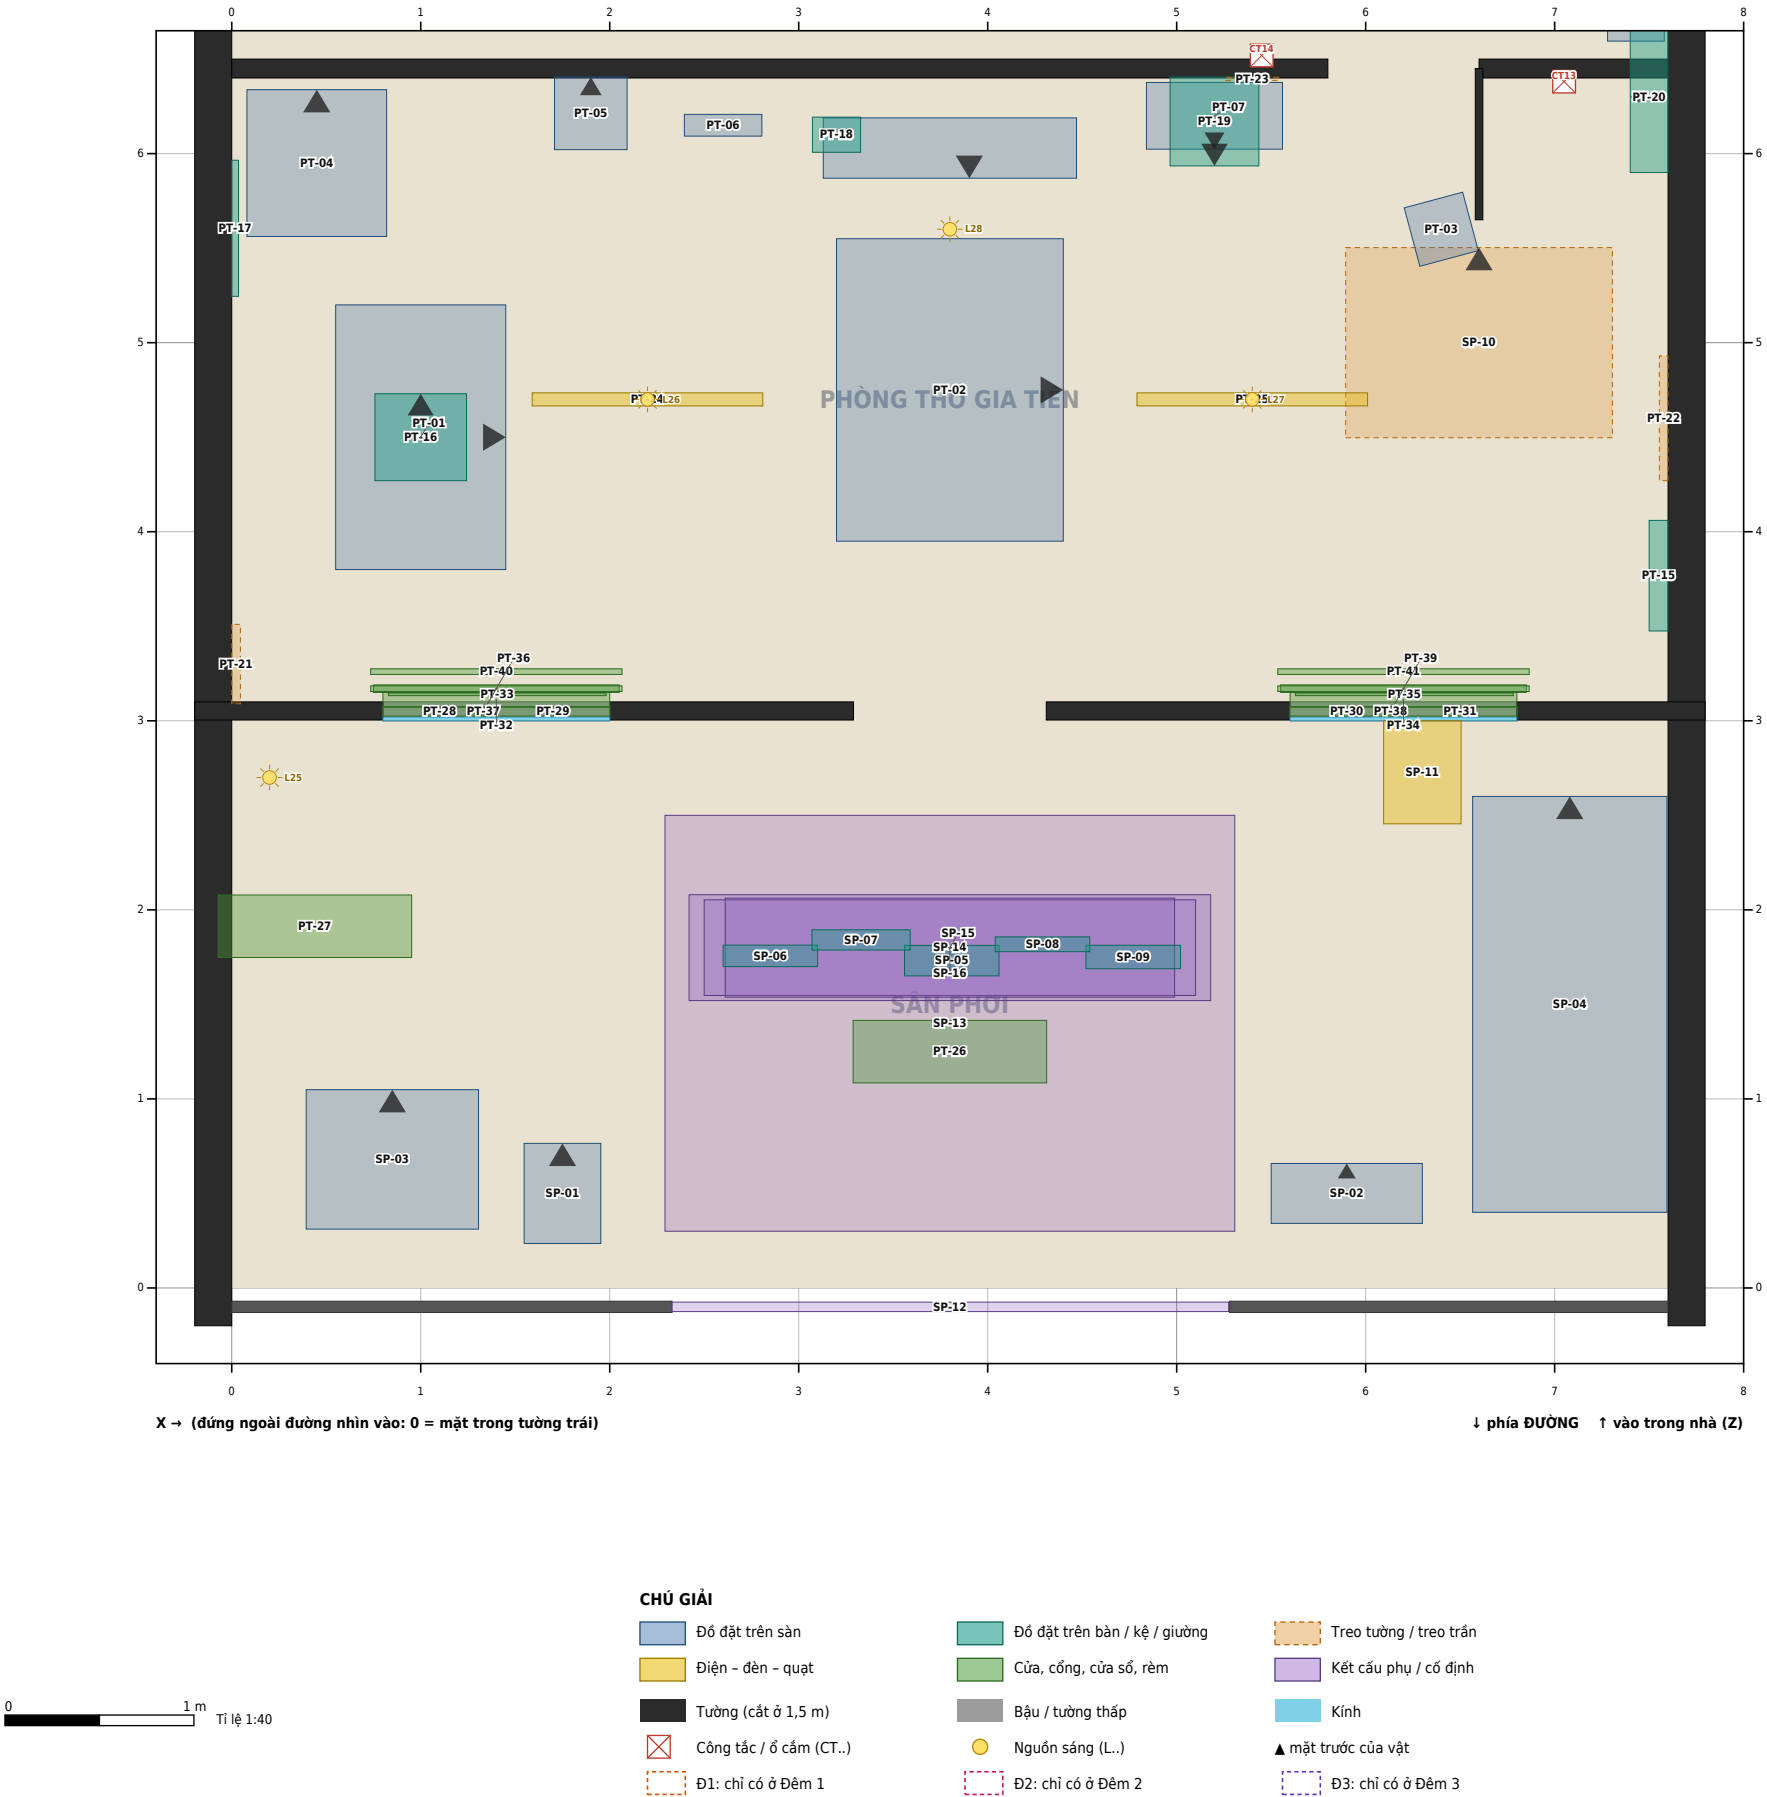


Mã	Tên (tên trong Unity)	Đềm	Tầm X	Tầm Z	Rộng×Sâu×Cao (m)	Y đáy → đỉnh	Hướng
ĐỒ ĐẶT TRÊN SÀN							
SP-01	Chậu nhựa ChauNhua		1,75	0,50	0,41×0,53×0,27	6,60 → 6,87	trong
SP-02	Chậu cây sân phơi ChauCay_SanPhoi		5,90	0,50	0,80×0,32×0,39	6,60 → 6,99	trong
SP-03	Bể nước có nắp BeNuc_Nap		0,85	0,68	0,91×0,74×0,82	6,60 → 7,42	trong
SP-04	Bồn hoa xây sân phơi BonHoa_SanPhoi		7,08	1,50	1,03×2,20×0,77	6,60 → 7,37	trong
PT-01	Sập gỗ thấp SapGo		1,00	4,50	1,40×0,90×0,36	6,60 → 6,96	→ phải
PT-02	Chiếu cỏi phòng thờ ChieuCoi_PhongTho		3,80	4,75	1,60×1,20×0,01	6,60 → 6,61	→ phải
PT-03	Ghế đầu gỗ GheDau_Go		6,40	5,60	0,32×0,32×0,44	6,60 → 7,04	-15°
PT-04	Chậu cây kiếng lá to ChauCayKiemg_LaTo		0,45	5,95	0,74×0,78×1,17	6,60 → 7,77	trong
PT-05	Bình hoa gốm lớn BinhHoaLon_Gom		1,90	6,21	0,38×0,38×0,80	6,60 → 7,40	trong
PT-06	Hương, nền dự trữ HuongMen_DuTru		2,60	6,15	0,41×0,11×0,30	6,60 → 6,90	trong
PT-07	Tủ đồ thờ TuDoTho_Fix		5,20	6,20	0,72×0,35×0,85	6,60 → 7,45	ra đường
PT-08	Bàn thờ gia tiên (cả bộ) BanThoGiaTien_Set		3,90	7,03	1,76×2,32×3,97	6,60 → 10,57	ra đường
PT-09	Kệ giày dép gỗ KeGiayDep_Go		7,43	7,00	0,81×0,30×0,66	6,60 → 7,25	← trái
PT-10	Chậu cây kiếng lá to ChauCayKiemg_LaTo		6,89	7,30	0,74×0,78×1,17	6,60 → 7,77	trong
PT-11	Hũ / bình ngâm rượu HuBinhNgamRuou		2,35	7,95	0,56×0,48×0,48	6,60 → 7,08	trong
PT-12	Giá phơi đồ xếp GiaPhoiDo_Xep		3,40	8,90	0,95×0,47×1,01	6,60 → 7,61	→ phải
PT-13	Chống thùng carton ThungCarton_Chong		3,67	10,45	1,09×0,54×0,97	6,60 → 7,57	8°
PT-14	Rổ nhựa quần áo bẩn RoNhua_QuanAoBan		6,90	10,40	0,54×0,53×0,54	6,60 → 7,14	trong
ĐỒ ĐẶT TRÊN BÀN / KỆ / GIƯỜNG							
SP-05	Áo tang phơi #3 AoTang_Phoi_03		3,81	1,73	0,50×0,16×0,94	7,31 → 8,25	trong
SP-06	Áo tang phơi #1 AoTang_Phoi_01		2,85	1,76	0,50×0,11×0,80	7,45 → 8,25	trong
SP-07	Áo tang phơi #2 AoTang_Phoi_02		3,33	1,84	0,52×0,11×0,71	7,55 → 8,25	trong
SP-08	Áo tang phơi #4 AoTang_Phoi_04		4,29	1,82	0,50×0,08×0,79	7,46 → 8,25	trong
SP-09	Áo tang phơi #5 AoTang_Phoi_05		4,77	1,75	0,50×0,12×0,77	7,49 → 8,25	trong
PT-15	Móc áo + khăn tắm MocAo_KhanTam		7,55	3,77	0,58×0,10×0,41	7,83 → 8,24	← trái
PT-16	Áo tang gấp (trên sạp) AoTangGap		1,00	4,50	0,48×0,46×0,19	6,96 → 7,15	trong
PT-17	Cụm ảnh cũ treo tường CumAnhCu_TreoTuong		0,02	5,61	0,72×0,04×0,75	7,84 → 8,60	→ phải
PT-18	Bình hoa bàn thờ BinhHoaTho		3,20	6,10	0,25×0,19×0,64	7,93 → 8,57	trong
PT-19	Mâm đồng hoa quả (thờ) MamDong_HoaQuaTho		5,20	6,17	0,47×0,47×0,12	7,45 → 7,56	ra đường
PT-20	Kệ gỗ treo tường KeGo_TreoTuong		7,50	6,30	0,80×0,20×0,67	7,98 → 8,65	← trái
TREO TƯỜNG / TREO TRẦN							
SP-10	Ăng-ten TV chữ Y trên mái AntenTV_MaiNha		6,60	5,00	1,41×1,01×2,00	9,80 → 11,80	trong
PT-21	Tranh chữ "Phúc" (quốc ngữ) TranhThuPhap_Phuc		0,02	3,30	0,42×0,05×0,62	8,25 → 8,87	→ phải
PT-22	Tranh hoa sen (khung) TranhHoaSen_Khung		7,58	4,60	0,66×0,05×0,46	8,25 → 8,71	← trái
PT-23	Lịch âm treo tường LichAm_TreoTuong		5,40	6,39	0,28×0,02×0,44	8,06 → 8,50	ra đường

Vật thứ 34 → 57 / 57

Mã	Tên (tên trong Unity)	Đêm	Tâm X	Tâm Z	Rộng×Sâu×Cao (m)	Y đáy → đỉnh	Hướng
ĐIỆN - ĐÈN - QUẠT							
SP-11	Bóng đèn chao tôn sân phơi + dây điện BongDenSan_DayDien		6,30	2,73	0,41×0,54×0,71	8,31 → 9,03	ra đường
PT-24	Đèn tuýp máng 1,2 m DenTuy_p_128		2,20	4,70	1,22×0,07×0,06	9,54 → 9,60	trong
PT-25	Đèn tuýp máng 1,2 m DenTuy_p_128		5,40	4,70	1,22×0,07×0,06	9,54 → 9,60	trong
CỬA, CỔNG, CỬA SỔ, RÈM							
PT-26	Cửa ra sân phơi (hé 0,25 m) CuaSanPhoi		3,80	1,25	1,02×0,33×2,16	6,60 → 8,76	ra đường
PT-27	Cửa ra sân phơi (hé 0,25 m) CuaSanPhoi		0,44	1,91	1,02×0,33×2,16	−0,00 → 2,16	trong
PT-28	Cửa sổ phòng Khôi (trái) CuaSo_Khoi_Trai		1,10	3,05	0,60×0,05×1,40	7,50 → 8,90	ra đường
PT-29	Cửa sổ phòng Khôi (phải) CuaSo_Khoi_Phai		1,70	3,05	0,60×0,05×1,40	7,50 → 8,90	trong
PT-30	Cửa sổ phòng Khôi (trái) CuaSo_Khoi_Trai		5,90	3,05	0,60×0,05×1,40	7,50 → 8,90	ra đường
PT-31	Cửa sổ phòng Khôi (phải) CuaSo_Khoi_Phai		6,50	3,05	0,60×0,05×1,40	7,50 → 8,90	trong
PT-32	Bậu cửa sổ granito — Khôi BauCuaSo_Granito_Khoi		1,40	3,11	1,20×0,08×0,03	7,47 → 7,50	trong
PT-33	Song sắt hoa cửa sổ Khôi SongSatHoa_Khoi		1,41	3,14	1,15×0,01×1,35	7,53 → 8,87	trong
PT-34	Bậu cửa sổ granito — Khôi BauCuaSo_Granito_Khoi		6,20	3,11	1,20×0,08×0,03	7,47 → 7,50	trong
PT-35	Song sắt hoa cửa sổ Khôi SongSatHoa_Khoi		6,21	3,14	1,15×0,01×1,35	7,53 → 8,87	trong
PT-36	Rèm voan trắng — phòng thờ Rem_Voan_PhongTho		1,40	3,17	1,30×0,04×1,65	7,40 → 9,05	trong
PT-37	Thanh treo rèm ThanhRem		1,40	3,17	1,33×0,03×0,03	9,05 → 9,08	trong
PT-38	Thanh treo rèm ThanhRem		6,20	3,17	1,33×0,03×0,03	9,05 → 9,08	trong
PT-39	Rèm voan trắng — phòng thờ Rem_Voan_PhongTho		6,20	3,17	1,30×0,04×1,65	7,40 → 9,05	trong
PT-40	Thanh treo rèm ThanhRem		1,40	3,26	1,33×0,03×0,03	9,05 → 9,08	trong
PT-41	Thanh treo rèm ThanhRem		6,20	3,26	1,33×0,03×0,03	9,05 → 9,08	trong
KẾT CẤU PHỤ / CỐ ĐỊNH							
SP-12	Lan can sân phơi (mô-đun) LanCanSanPhoi		3,80	−0,10	2,95×0,05×1,10	6,70 → 7,80	trong
SP-13	Nền sân phơi NenSanPhoi		3,80	1,40	3,02×2,20×0,05	6,60 → 6,65	trong
SP-14	Kẹp phơi KepPhoi		3,80	1,80	2,38×0,52×0,12	8,20 → 8,32	trong
SP-15	Dây phơi DayPhoi		3,80	1,80	2,60×0,51×0,06	8,19 → 8,25	trong
SP-16	Cột phơi CotPhoi		3,80	1,80	2,76×0,56×1,80	6,64 → 8,44	trong

Tầng 3 (+6,60) · 7 vật trong GK

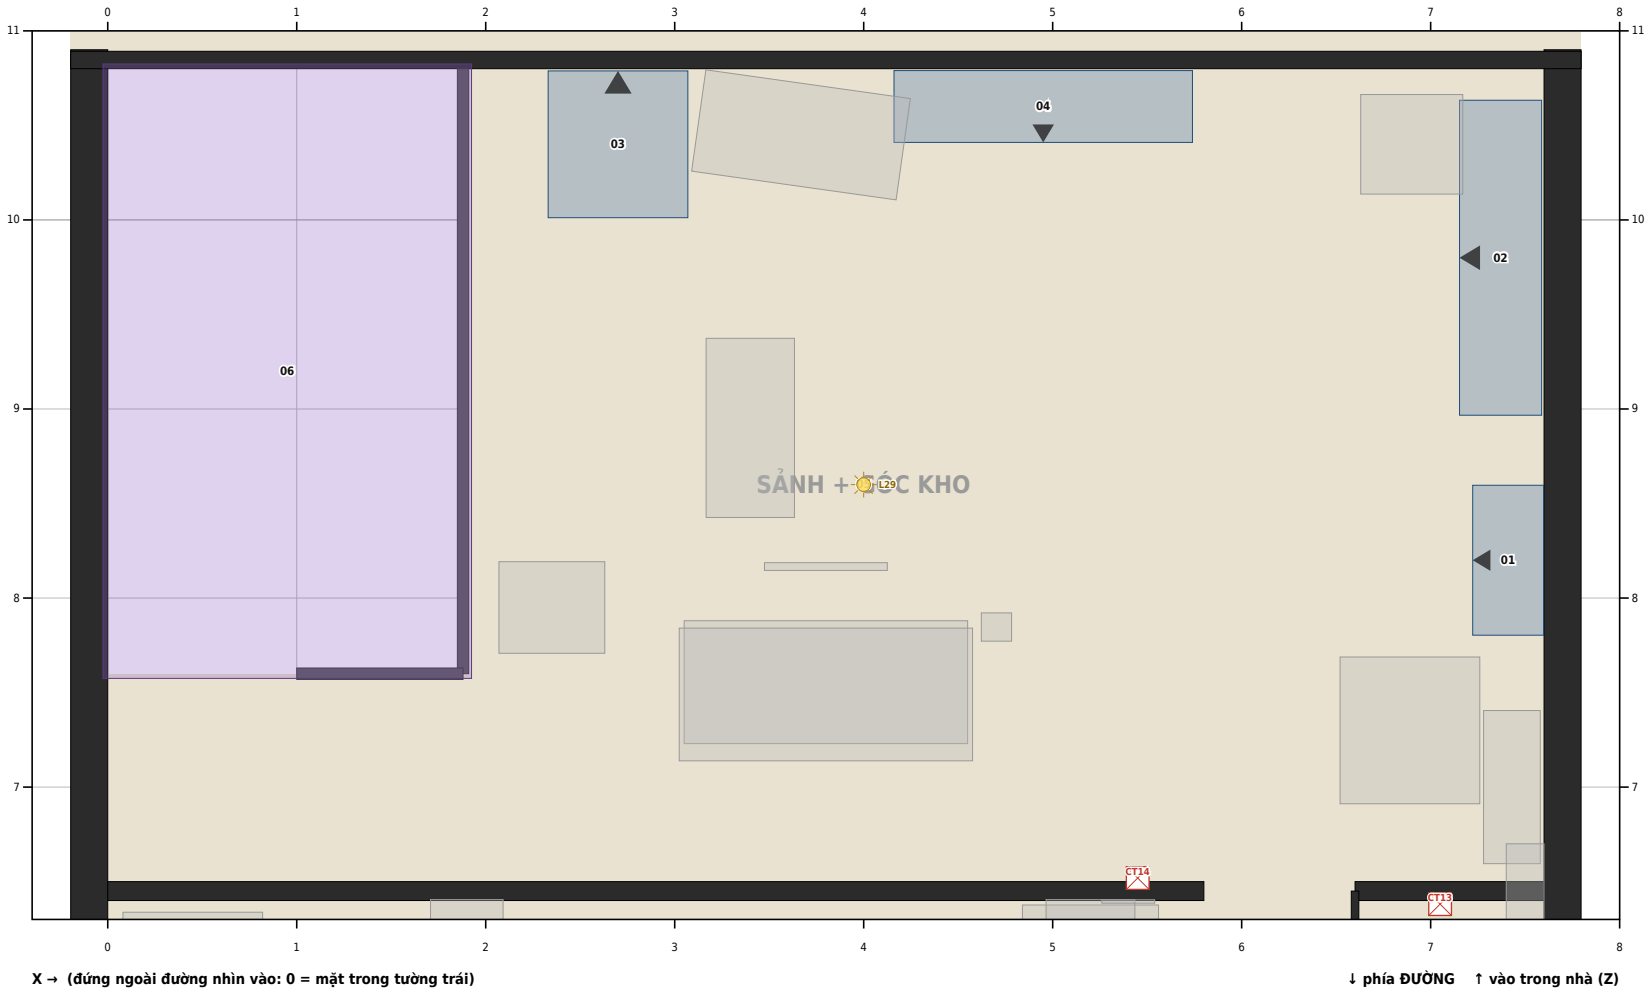

Mã	Tên (tên trong Unity)	Đêm	Tâm X	Tâm Z	Rộng×Sâu×Cao (m)	Y đáy → đỉnh	Hướng
ĐỒ ĐẶT TRÊN SÀN							
GK-01	Góc kho: đồ Tết (mai giả, đèn ông ... <i>GocKho_DoTet_Fix</i>		7,41	8,20	0,79×0,38×0,68	6,60 → 7,28	← trái
GK-02	Góc kho: đồ gỗ (nồi đồng, thùng, ... <i>GocKho_DoGio_Fix</i>		7,37	9,80	1,67×0,43×0,29	6,60 → 6,89	← trái
GK-03	Chậu cây kiếng lá to <i>ChauCayKieng-LaTo</i>		2,70	10,40	0,74×0,78×1,17	6,60 → 7,77	trong
GK-04	Góc kho: quạt gậy, chiếu cuộn, mả... <i>GocKho_DoNha_Fix</i>		4,95	10,60	1,58×0,38×1,06	6,60 → 7,66	ra đường
ĐIỆN - ĐÈN - QUẠT							
GK-05	Bóng đèn compact <i>BongCompact</i>		4,00	8,60	0,04×0,03×0,13	9,47 → 9,60	trong
KẾT CẤU PHỤ / CỐ ĐỊNH							
GK-06	Giếng trời (mái lấy sáng) <i>GiengTroai</i>		0,95	9,20	1,95×3,25×0,26	9,60 → 9,86	trong
GK-07	Bồn nước mái <i>BonNuocMai</i>		5,30	13,50	1,47×0,96×1,56	6,60 → 8,16	trong

Mỗi cụm = mặt nhựa + phím + đèn neon + biểu tượng (LocCongTac) · tâm cụm đo ở mặt tường

Mã	Cụm (tên trong scene)	Tầng	Tâm X	Tâm Z	Y đáy → đỉnh	Gắn trên tường	Số khối
CT01	CongTac_Hien	Tầng 1 (±0,00)	2,10	0,02	1,33 → 1,57	vuông góc trục Z (tường trước/sau)	12
CT02	CongTac_Ham	Tầng 1 (±0,00)	7,58	6,90	1,33 → 1,57	vuông góc trục X (tường trái/phải)	7
CT03	CongTac_PhongKhach	Tầng 1 (±0,00)	5,30	7,38	1,33 → 1,57	vuông góc trục Z (tường trước/sau)	22
CT04	CongTac_SanhSau	Tầng 1 (±0,00)	4,75	10,88	1,33 → 1,57	vuông góc trục Z (tường trước/sau)	12
CT05	CongTac_Bep_Cua	Tầng 1 (±0,00)	4,75	11,02	1,33 → 1,57	vuông góc trục Z (tường trước/sau)	12
CT06	CongTac_Bep_GiengTroi	Tầng 1 (±0,00)	3,10	16,38	1,33 → 1,57	vuông góc trục Z (tường trước/sau)	7
CT07	CongTac_WC_T1	Tầng 1 (±0,00)	4,58	21,30	1,33 → 1,57	vuông góc trục X (tường trái/phải)	7
CT08	CongTac_BoMe	Tầng 2 (+3,40)	3,25	5,38	4,73 → 4,97	vuông góc trục Z (tường trước/sau)	12
CT09	CongTac_PhongNhim	Tầng 2 (+3,40)	3,22	10,15	4,73 → 4,97	vuông góc trục X (tường trái/phải)	7
CT10	CongTac_HanhLang_ChieuNghì	Tầng 2 (+3,40)	3,08	10,40	4,73 → 4,97	vuông góc trục X (tường trái/phải)	12
CT11	CongTac_HanhLang_Khoi	Tầng 2 (+3,40)	3,08	13,00	4,73 → 4,97	vuông góc trục X (tường trái/phải)	7
CT12	CongTac_PhongKhoi	Tầng 2 (+3,40)	3,22	14,45	4,73 → 4,97	vuông góc trục X (tường trái/phải)	12
CT13	CongTac_PhongTho	Tầng 3 (+6,60)	7,05	6,38	7,93 → 8,17	vuông góc trục Z (tường trước/sau)	12
CT14	CongTac_Sanh_T3	Tầng 3 (+6,60)	5,45	6,52	7,93 → 8,17	vuông góc trục Z (tường trước/sau)	7

Ghi chú: toàn bộ công tắc đặt ở tâm cao 1,45 m (1,33 → 1,57) — vừa tầm mắt 1,65 m, theo yêu cầu "công tắc phải rõ ràng, vừa tầm mắt" (29/9). CongTac_Ham ở tường phải hãm (X 7,56–7,60).

Đèn điểm Unity (Point Light) · màu, tầm chiếu và cường độ như trong scene (chưa tính ánh sáng bake)

Mã	Tên trong scene	Tầng	X	Z	Y (cao)	Màu	Tầm (m)	Cường độ
L01	Den_BongDayToc_Ham	Hầm (−2,30)	6,40	11,90	−0,50	#FF9A3C	4,0	1,00
L02	Den_Rap_Trai	Tầng 1 (±0,00)	1,90	−2,60	2,40	#FFD27A	6,0	2,00
L03	Den_Rap_Phai	Tầng 1 (±0,00)	5,70	−2,60	2,40	#FFD27A	6,0	2,00
L04	Den_PhongKhach_Tuyp	Tầng 1 (±0,00)	3,00	1,00	3,00	#DDEBFF	7,0	1,10
L05	Den_NenDien_BanTho	Tầng 1 (±0,00)	0,80	3,70	1,15	#FF5A3C	1,8	0,80
L06	Den_PhongKhach_Chum	Tầng 1 (±0,00)	3,00	3,70	2,45	#FFD9A0	7,0	1,20
L07	Den_Tiem_Kho	Tầng 1 (±0,00)	−2,30	4,30	3,20	#FFE9C8	5,0	0,50
L08	Den_PhongKhach_Sau	Tầng 1 (±0,00)	4,50	6,40	3,00	#DDEBFF	5,0	0,60
L09	Den_SanhSau	Tầng 1 (±0,00)	4,10	9,20	3,00	#FFF1D6	5,0	0,70
L10	Den_ChieuNghì_T1	Tầng 1 (±0,00)	0,95	10,30	2,90	#FFF1D6	4,0	0,60
L11	Den_Bep	Tầng 1 (±0,00)	3,80	13,70	3,00	#DDEBFF	7,0	1,20
L12	Den_GiengTroi	Tầng 1 (±0,00)	0,20	17,80	2,60	#FFE9B8	5,0	0,50
L13	Den_WC_T1	Tầng 1 (±0,00)	6,10	20,50	3,00	#FFF1D6	3,0	0,40
L14	Den_Kho	Tầng 1 (±0,00)	1,80	21,90	3,00	#FFF1D6	5,0	0,50
L15	Den_Giat	Tầng 1 (±0,00)	5,60	23,30	3,00	#FFF1D6	4,0	0,40
L16	Den_Tiem_BanHang	Tầng 2 (+3,40)	−2,30	−2,00	3,35	#DDEBFF	6,0	0,90
L17	Den_BoMe_OpTran	Tầng 2 (+3,40)	3,40	2,70	6,30	#FFE3B0	7,0	1,00
L18	Den_Sanh_T2	Tầng 2 (+3,40)	1,50	6,50	6,30	#FFE3B0	5,0	0,70
L19	Den_LamViec	Tầng 2 (+3,40)	5,40	6,90	6,30	#FFE3B0	4,0	0,40
L20	Den_DenNgu_Nhim	Tầng 2 (+3,40)	6,55	8,75	4,35	#FFB36B	4,5	0,90
L21	Den_ChieuNghì_T2	Tầng 2 (+3,40)	0,95	10,20	6,20	#FFF1D6	4,0	0,60
L22	Den_HanhLang_T2	Tầng 2 (+3,40)	2,50	13,00	6,30	#FFE3B0	5,0	0,60
L23	Den_Khoi_Tran	Tầng 2 (+3,40)	5,40	14,40	6,30	#FFE3B0	5,0	0,35
L24	Den_DenBan_Khoi	Tầng 2 (+3,40)	5,30	15,90	4,60	#FFD08A	3,5	0,90
L25	Den_SanPhoi	Tầng 3 (+6,60)	0,20	2,70	8,60	#FFE9B8	5,0	0,70
L26	Den_PhongTho_1	Tầng 3 (+6,60)	2,20	4,70	9,40	#FFF6E0	6,0	1,30
L27	Den_PhongTho_2	Tầng 3 (+6,60)	5,40	4,70	9,40	#FFF6E0	6,0	1,30
L28	Den_NenDien_GiaTien	Tầng 3 (+6,60)	3,80	5,60	7,90	#FF5A3C	1,5	0,60
L29	Den_Sanh_T3	Tầng 3 (+6,60)	4,00	8,60	9,50	#FFF6E0	6,0	0,90

64 decal · toạ độ tâm · kích thước w×h (mét) · "Đỉnh" = cao độ tâm

STT	Tên decal	Tầng	Tâm X	Tâm Z	Cao độ Y	Rộng × Cao (m)	Nhóm trong scene
1	T_BienHieu_BC	Tầng 1 (±0,00)	−2,30	−5,46	2,93	3,52 × 1,00	Tiem/VoNha
2	ToGiay_NghiBan	Tầng 1 (±0,00)	−2,30	−5,33	1,50	1,00 × 1,00	Tiem/VoNha
3	ChanTuong_Ban	Tầng 1 (±0,00)	0,00	0,90	0,20	1,60 × 1,00	Tang_1/PhongKhach
4	VetGheCoTuong	Tầng 1 (±0,00)	7,60	1,95	0,55	1,50 × 1,00	Tang_1/PhongKhach
5	KhoiAmTran	Tầng 1 (±0,00)	0,90	3,70	3,20	1,60 × 1,00	Tang_1/PhongKhach
6	ChanTuong_Ban	Tầng 1 (±0,00)	7,60	5,50	0,20	1,60 × 1,00	Tang_1/PhongKhach
7	VetTayCongTac	Tầng 1 (±0,00)	7,60	6,90	1,56	1,00 × 1,00	Ham
8	VetTayCongTac	Tầng 1 (±0,00)	5,30	7,39	1,56	1,00 × 1,00	Tang_1/PhongKhach
9	BacThang_Mon	Tầng 1 (±0,00)	0,45	7,72	3,23	1,00 × 1,00	Tang_1/VoNha
10	BacThang_Mon	Tầng 1 (±0,00)	1,45	7,72	0,17	1,00 × 1,00	Tang_1/VoNha
11	BacThang_Mon	Tầng 1 (±0,00)	0,45	7,97	3,06	1,00 × 1,00	Tang_1/VoNha
12	BacThang_Mon	Tầng 1 (±0,00)	1,45	7,97	0,34	1,00 × 1,00	Tang_1/VoNha
13	BacThang_Mon	Tầng 1 (±0,00)	0,45	8,22	2,89	1,00 × 1,00	Tang_1/VoNha
14	BacThang_Mon	Tầng 1 (±0,00)	1,45	8,22	0,51	1,00 × 1,00	Tang_1/VoNha
15	BacThang_Mon	Tầng 1 (±0,00)	0,45	8,47	2,72	1,00 × 1,00	Tang_1/VoNha
16	BacThang_Mon	Tầng 1 (±0,00)	1,45	8,47	0,68	1,00 × 1,00	Tang_1/VoNha
17	BacThang_Mon	Tầng 1 (±0,00)	0,45	8,72	2,55	1,00 × 1,00	Tang_1/VoNha
18	BacThang_Mon	Tầng 1 (±0,00)	1,45	8,72	0,85	1,00 × 1,00	Tang_1/VoNha
19	BacThang_Mon	Tầng 1 (±0,00)	0,45	8,97	2,38	1,00 × 1,00	Tang_1/VoNha
20	BacThang_Mon	Tầng 1 (±0,00)	1,45	8,97	1,02	1,00 × 1,00	Tang_1/VoNha
21	BacThang_Mon	Tầng 1 (±0,00)	0,45	9,22	2,21	1,00 × 1,00	Tang_1/VoNha
22	BacThang_Mon	Tầng 1 (±0,00)	1,45	9,22	1,19	1,00 × 1,00	Tang_1/VoNha
23	BacThang_Mon	Tầng 1 (±0,00)	0,45	9,47	2,04	1,00 × 1,00	Tang_1/VoNha
24	BacThang_Mon	Tầng 1 (±0,00)	1,45	9,47	1,36	1,00 × 1,00	Tang_1/VoNha
25	BacThang_Mon	Tầng 1 (±0,00)	0,45	9,72	1,87	1,00 × 1,00	Tang_1/VoNha
26	BacThang_Mon	Tầng 1 (±0,00)	1,45	9,72	1,53	1,00 × 1,00	Tang_1/VoNha
27	VetNuocTran	Tầng 1 (±0,00)	6,60	12,40	3,20	1,00 × 1,00	Tang_1/Bep
28	VetNuoc_San	Tầng 1 (±0,00)	0,90	15,30	0,00	1,00 × 1,00	Tang_1/Bep
29	ChanTuong_Ban	Tầng 1 (±0,00)	7,60	15,30	0,20	1,60 × 1,00	Tang_1/Bep
30	VetTayCongTac	Tầng 1 (±0,00)	3,10	16,39	1,56	1,00 × 1,00	Tang_1/Bep
31	NamMoc	Tầng 1 (±0,00)	3,00	16,50	2,70	1,00 × 1,00	Tang_1/GiengTroi
32	MangNhen	Tầng 1 (±0,00)	0,00	19,25	2,90	1,00 × 1,00	Tang_1/KhoiSau
33	NamMoc	Tầng 1 (±0,00)	4,71	20,30	2,48	1,00 × 1,00	Tang_1/KhoiSau
34	VetNuoc_San	Tầng 1 (±0,00)	6,60	21,40	0,00	1,00 × 1,00	Tang_1/KhoiSau

64 decal · toạ độ tâm · kích thước w×h (mét) · "Đỉnh" = cao độ tâm

STT	Tên decal	Tầng	Tâm X	Tâm Z	Cao độ Y	Rộng × Cao (m)	Nhóm trong scene
35	NamMoc	Tầng 1 (±0,00)	6,20	21,80	2,65	1,00 × 1,00	Tang_1/KhoiSau
36	NamMoc	Tầng 1 (±0,00)	3,60	22,30	2,65	1,00 × 1,00	Tang_1/KhoiSau
37	NamMoc	Tầng 1 (±0,00)	0,01	23,00	2,70	1,00 × 1,00	Tang_1/KhoiSau
38	VetAm_Ham	Hầm (−2,30)	5,20	12,00	−1,02	1,20 × 1,00	Ham
39	BacThang_Mon	Tầng 2 (+3,40)	0,45	7,72	6,42	1,00 × 1,00	Tang_2/VoNha
40	BacThang_Mon	Tầng 2 (+3,40)	1,45	7,72	3,58	1,00 × 1,00	Tang_2/VoNha
41	BacThang_Mon	Tầng 2 (+3,40)	0,45	7,97	6,25	1,00 × 1,00	Tang_2/VoNha
42	BacThang_Mon	Tầng 2 (+3,40)	1,45	7,97	3,76	1,00 × 1,00	Tang_2/VoNha
43	VetTreoAnh	Tầng 2 (+3,40)	3,10	8,05	5,03	1,00 × 1,00	Tang_2/SanhHanhLang
44	BacThang_Mon	Tầng 2 (+3,40)	0,45	8,22	6,07	1,00 × 1,00	Tang_2/VoNha
45	BacThang_Mon	Tầng 2 (+3,40)	1,45	8,22	3,94	1,00 × 1,00	Tang_2/VoNha
46	BacThang_Mon	Tầng 2 (+3,40)	0,45	8,47	5,89	1,00 × 1,00	Tang_2/VoNha
47	BacThang_Mon	Tầng 2 (+3,40)	1,45	8,47	4,11	1,00 × 1,00	Tang_2/VoNha
48	BacThang_Mon	Tầng 2 (+3,40)	0,45	8,72	5,71	1,00 × 1,00	Tang_2/VoNha
49	BacThang_Mon	Tầng 2 (+3,40)	1,45	8,72	4,29	1,00 × 1,00	Tang_2/VoNha
50	BacThang_Mon	Tầng 2 (+3,40)	0,45	8,97	5,54	1,00 × 1,00	Tang_2/VoNha
51	BacThang_Mon	Tầng 2 (+3,40)	1,45	8,97	4,47	1,00 × 1,00	Tang_2/VoNha
52	BacThang_Mon	Tầng 2 (+3,40)	0,45	9,22	5,36	1,00 × 1,00	Tang_2/VoNha
53	BacThang_Mon	Tầng 2 (+3,40)	1,45	9,22	4,65	1,00 × 1,00	Tang_2/VoNha
54	BacThang_Mon	Tầng 2 (+3,40)	0,45	9,47	5,18	1,00 × 1,00	Tang_2/VoNha
55	BacThang_Mon	Tầng 2 (+3,40)	1,45	9,47	4,83	1,00 × 1,00	Tang_2/VoNha
56	TranhSap_2	Tầng 2 (+3,40)	7,60	9,55	4,59	1,00 × 1,00	Tang_2/PhongNhim
57	VachChieuCao	Tầng 2 (+3,40)	3,21	9,98	4,33	1,00 × 1,00	Tang_2/PhongNhim
58	VetButSap	Tầng 2 (+3,40)	7,59	10,00	3,83	1,00 × 1,00	Tang_2/PhongNhim
59	Sticker_TuNhua	Tầng 2 (+3,40)	7,20	11,00	4,15	1,00 × 1,00	Tang_2/PhongNhim
60	MangNhen	Tầng 2 (+3,40)	3,20	12,55	6,25	1,00 × 1,00	Tang_2/PhongKhoi
61	VetNuocTran	Tầng 2 (+3,40)	2,00	12,60	6,38	1,10 × 1,00	Tang_2/SanhHanhLang
62	NamMoc	Tầng 2 (+3,40)	3,21	15,90	5,85	1,00 × 1,00	Tang_2/PhongKhoi
63	VetNuocTran	Tầng 3 (+6,60)	6,80	4,40	9,60	1,10 × 1,00	Tang_3/PhongTho
64	KhoiAmTran	Tầng 3 (+6,60)	3,80	6,00	9,60	2,00 × 1,00	Tang_3/PhongTho